


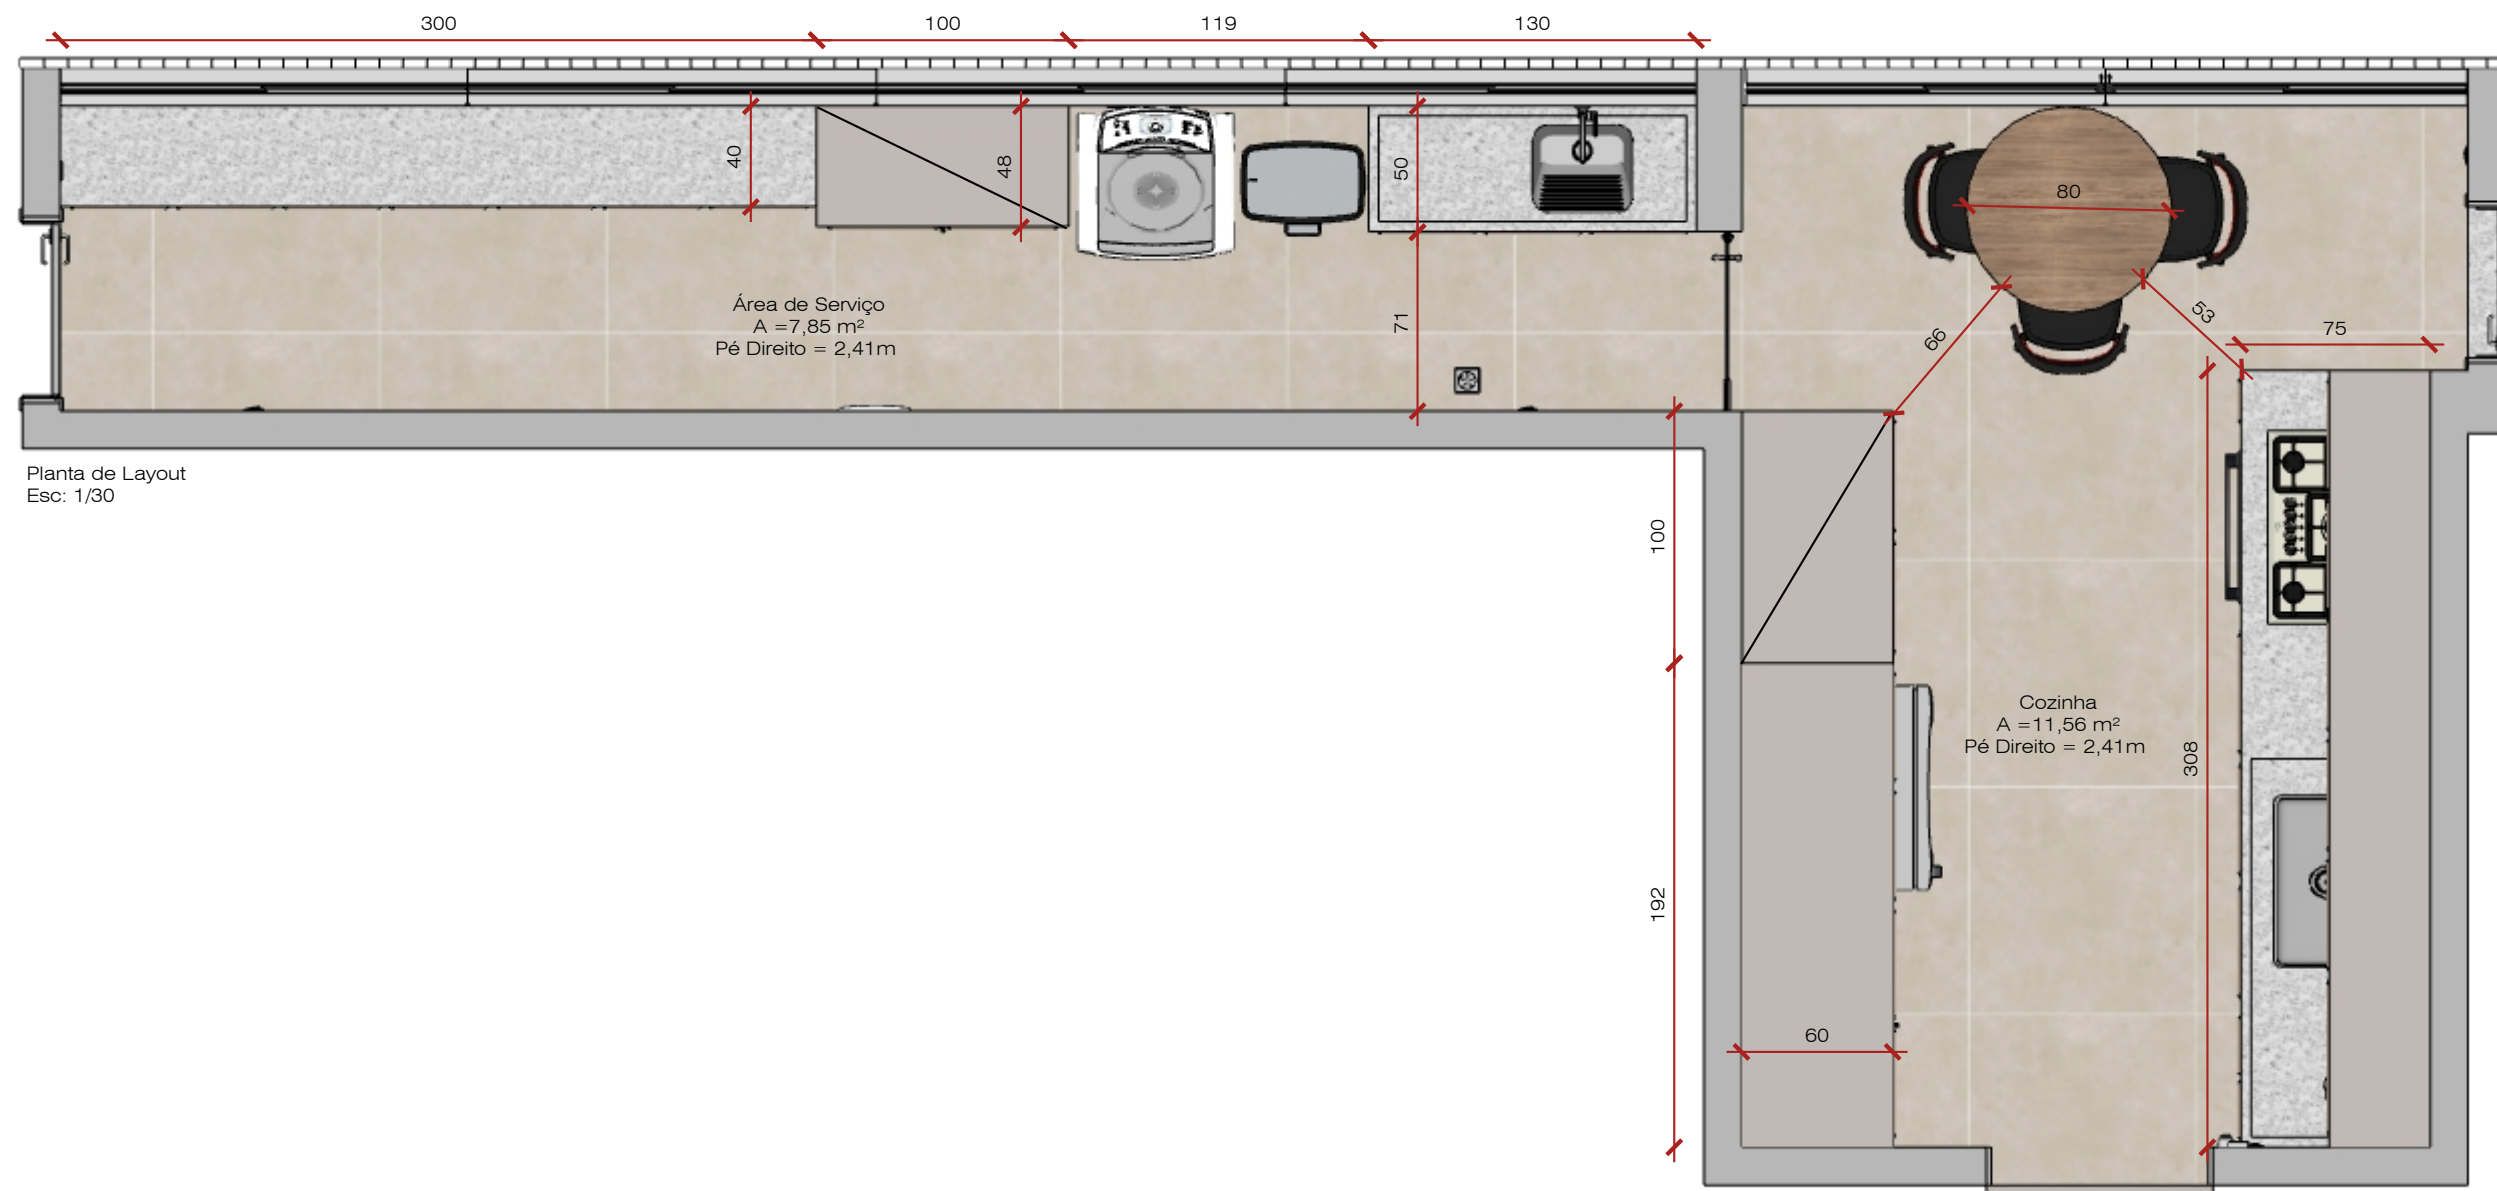

Cozinha e Área de Serviço

Desenhista: Nathália Rodrigues

As imagens 3D são meramente ilustrativa.
Seguir orientações conforme detalhamento executivo.

Todas as medidas devem ser conferidas no local antes da execução.

Clientes:
Silvana e Hélio

Endereço:
SQS 106 Bloco H, Apartamento 601.
Asa Sul

Data:
27.08.2026

Arquiteto coordenador

Alisson Correia
Celular (61) 98303-0582


Arquiteta responsável

Aline Coutinho Molina
CAU - A108129-2
Celular (61) 99606-5747

Obs: Todas as medidas em centímetros

10

Aline Molina
arquitetura de interiores

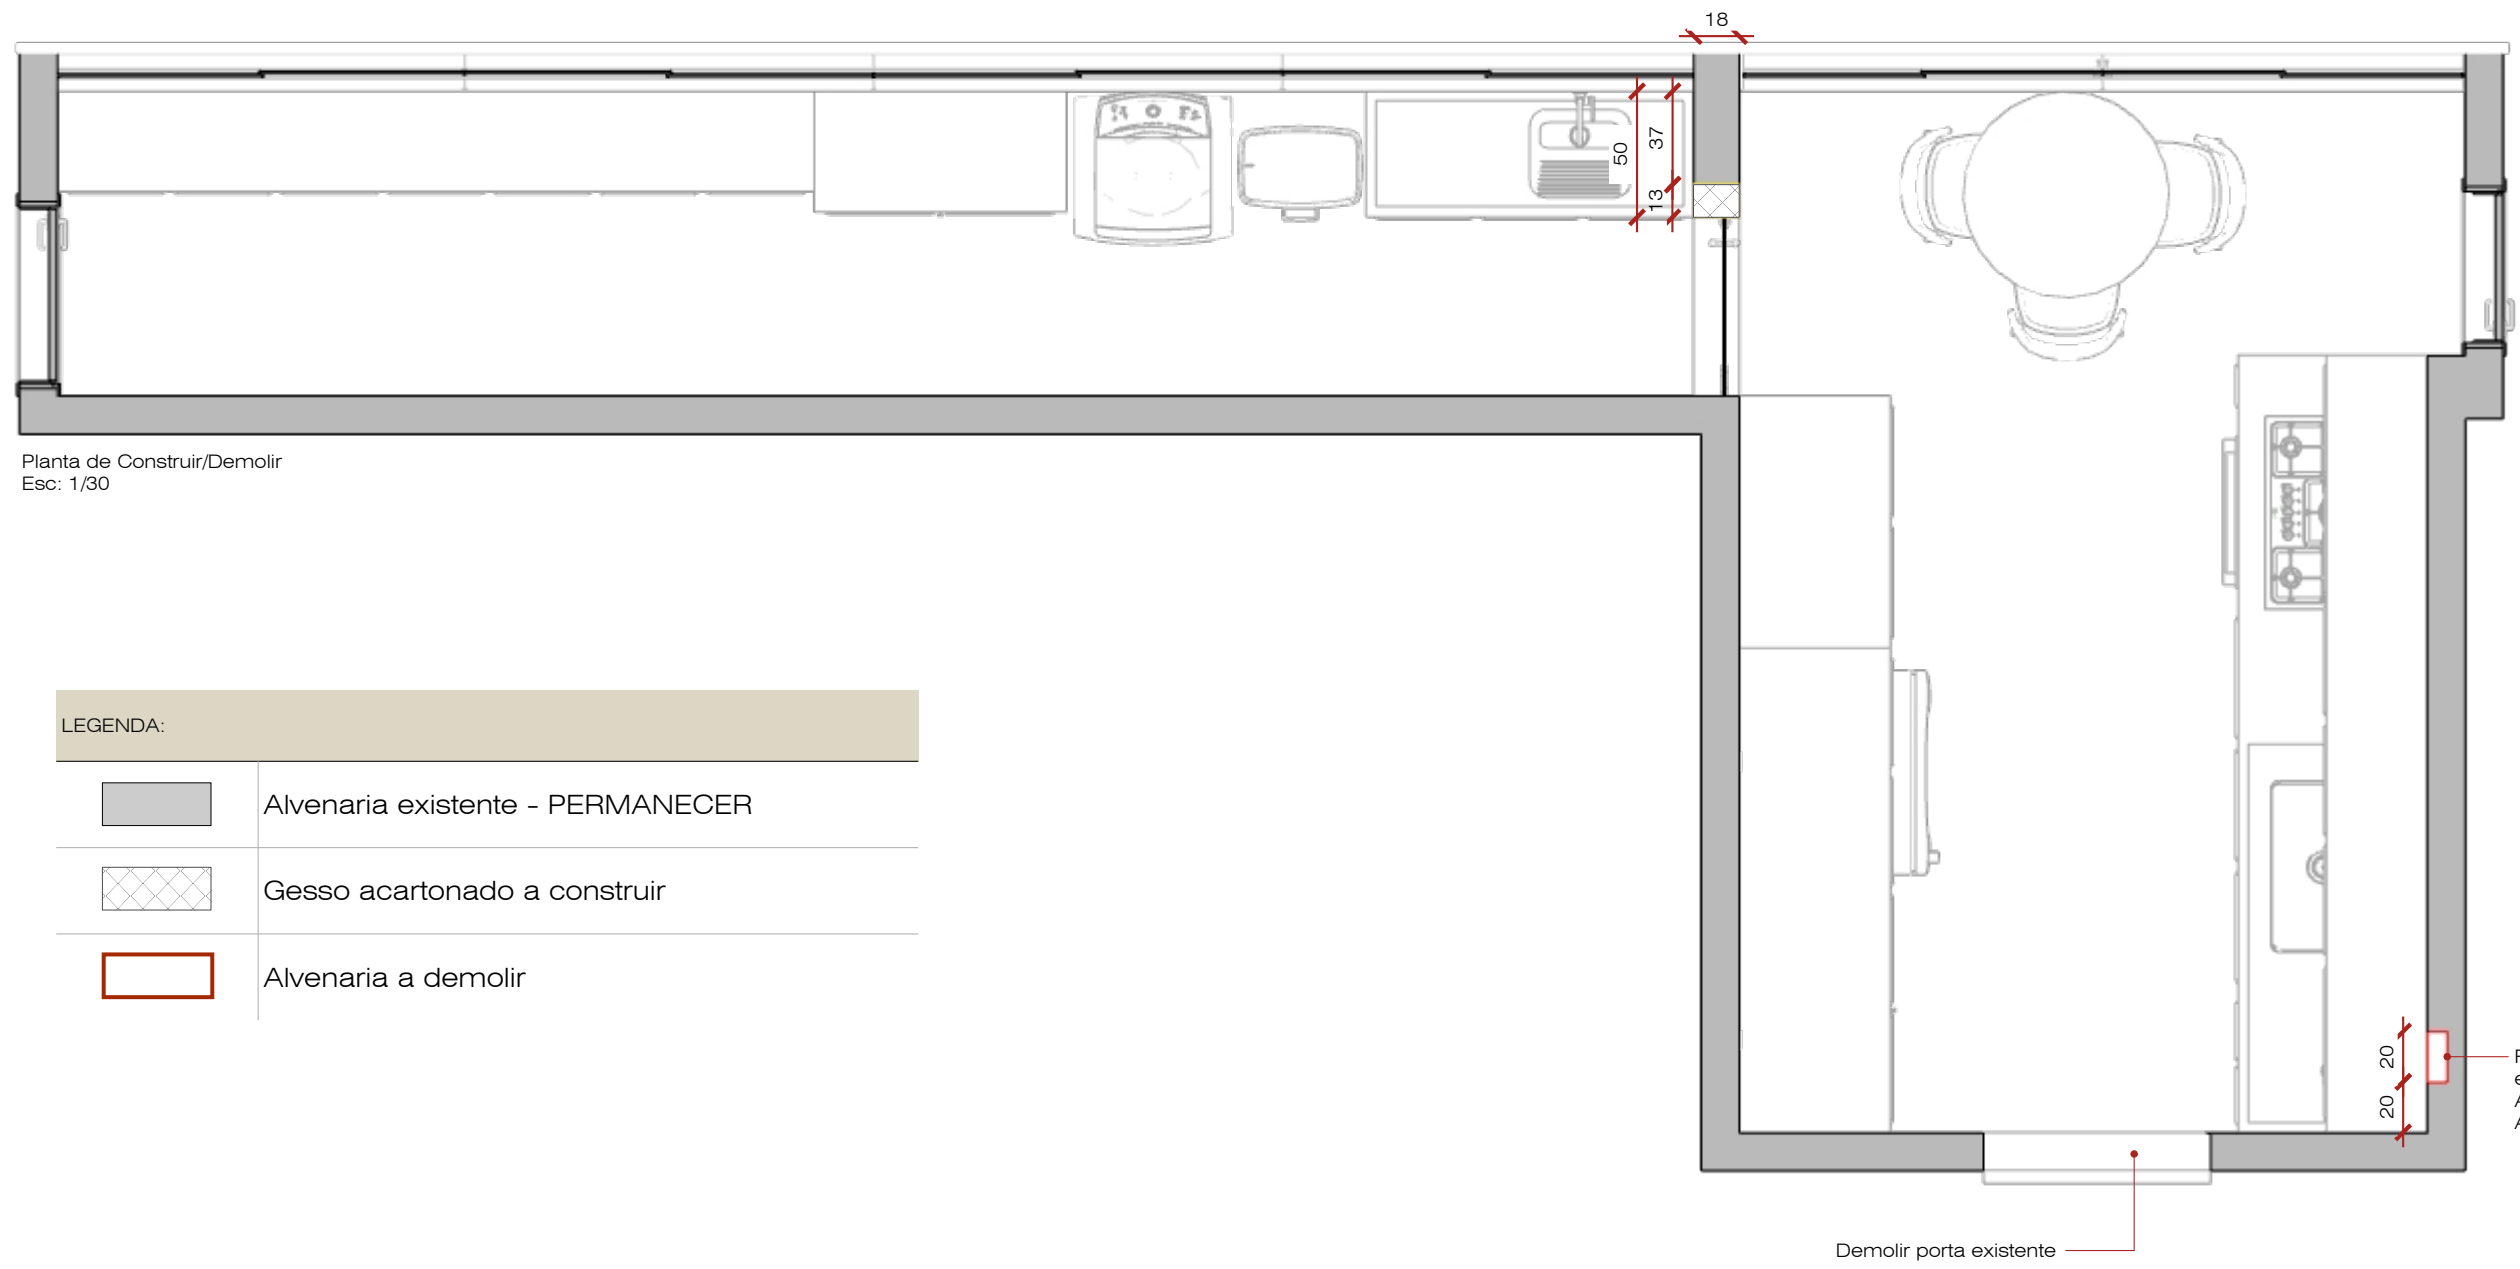

Planta de Construir/Demolir
Esc: 1/30

LEGENDA:

	Alvenaria existente - PERMANECER
	Gesso acartonado a construir
	Alvenaria a demolir

Cozinha e Área de Serviço

Desenhista: Nathália Rodrigues

As imagens 3D são meramente ilustrativa.
Seguir orientações conforme detalhamento executivo.

Todas as medidas devem ser conferidas no local antes da execução.

Clientes:
Silvana e Hélio

Endereço:
SQS 106 Bloco H, Apartamento 601.
Asa Sul

Data:
27.08.2026

Arquiteto coordenador

Alisson Correia
Celular (61) 98303-0582


Arquiteta responsável

Aline Coutinho Molina
CAU - A108129-2
Celular (61) 99606-5747

11

Aline Molina
arquitetura de interiores

Obs: Todas as medidas em centímetros

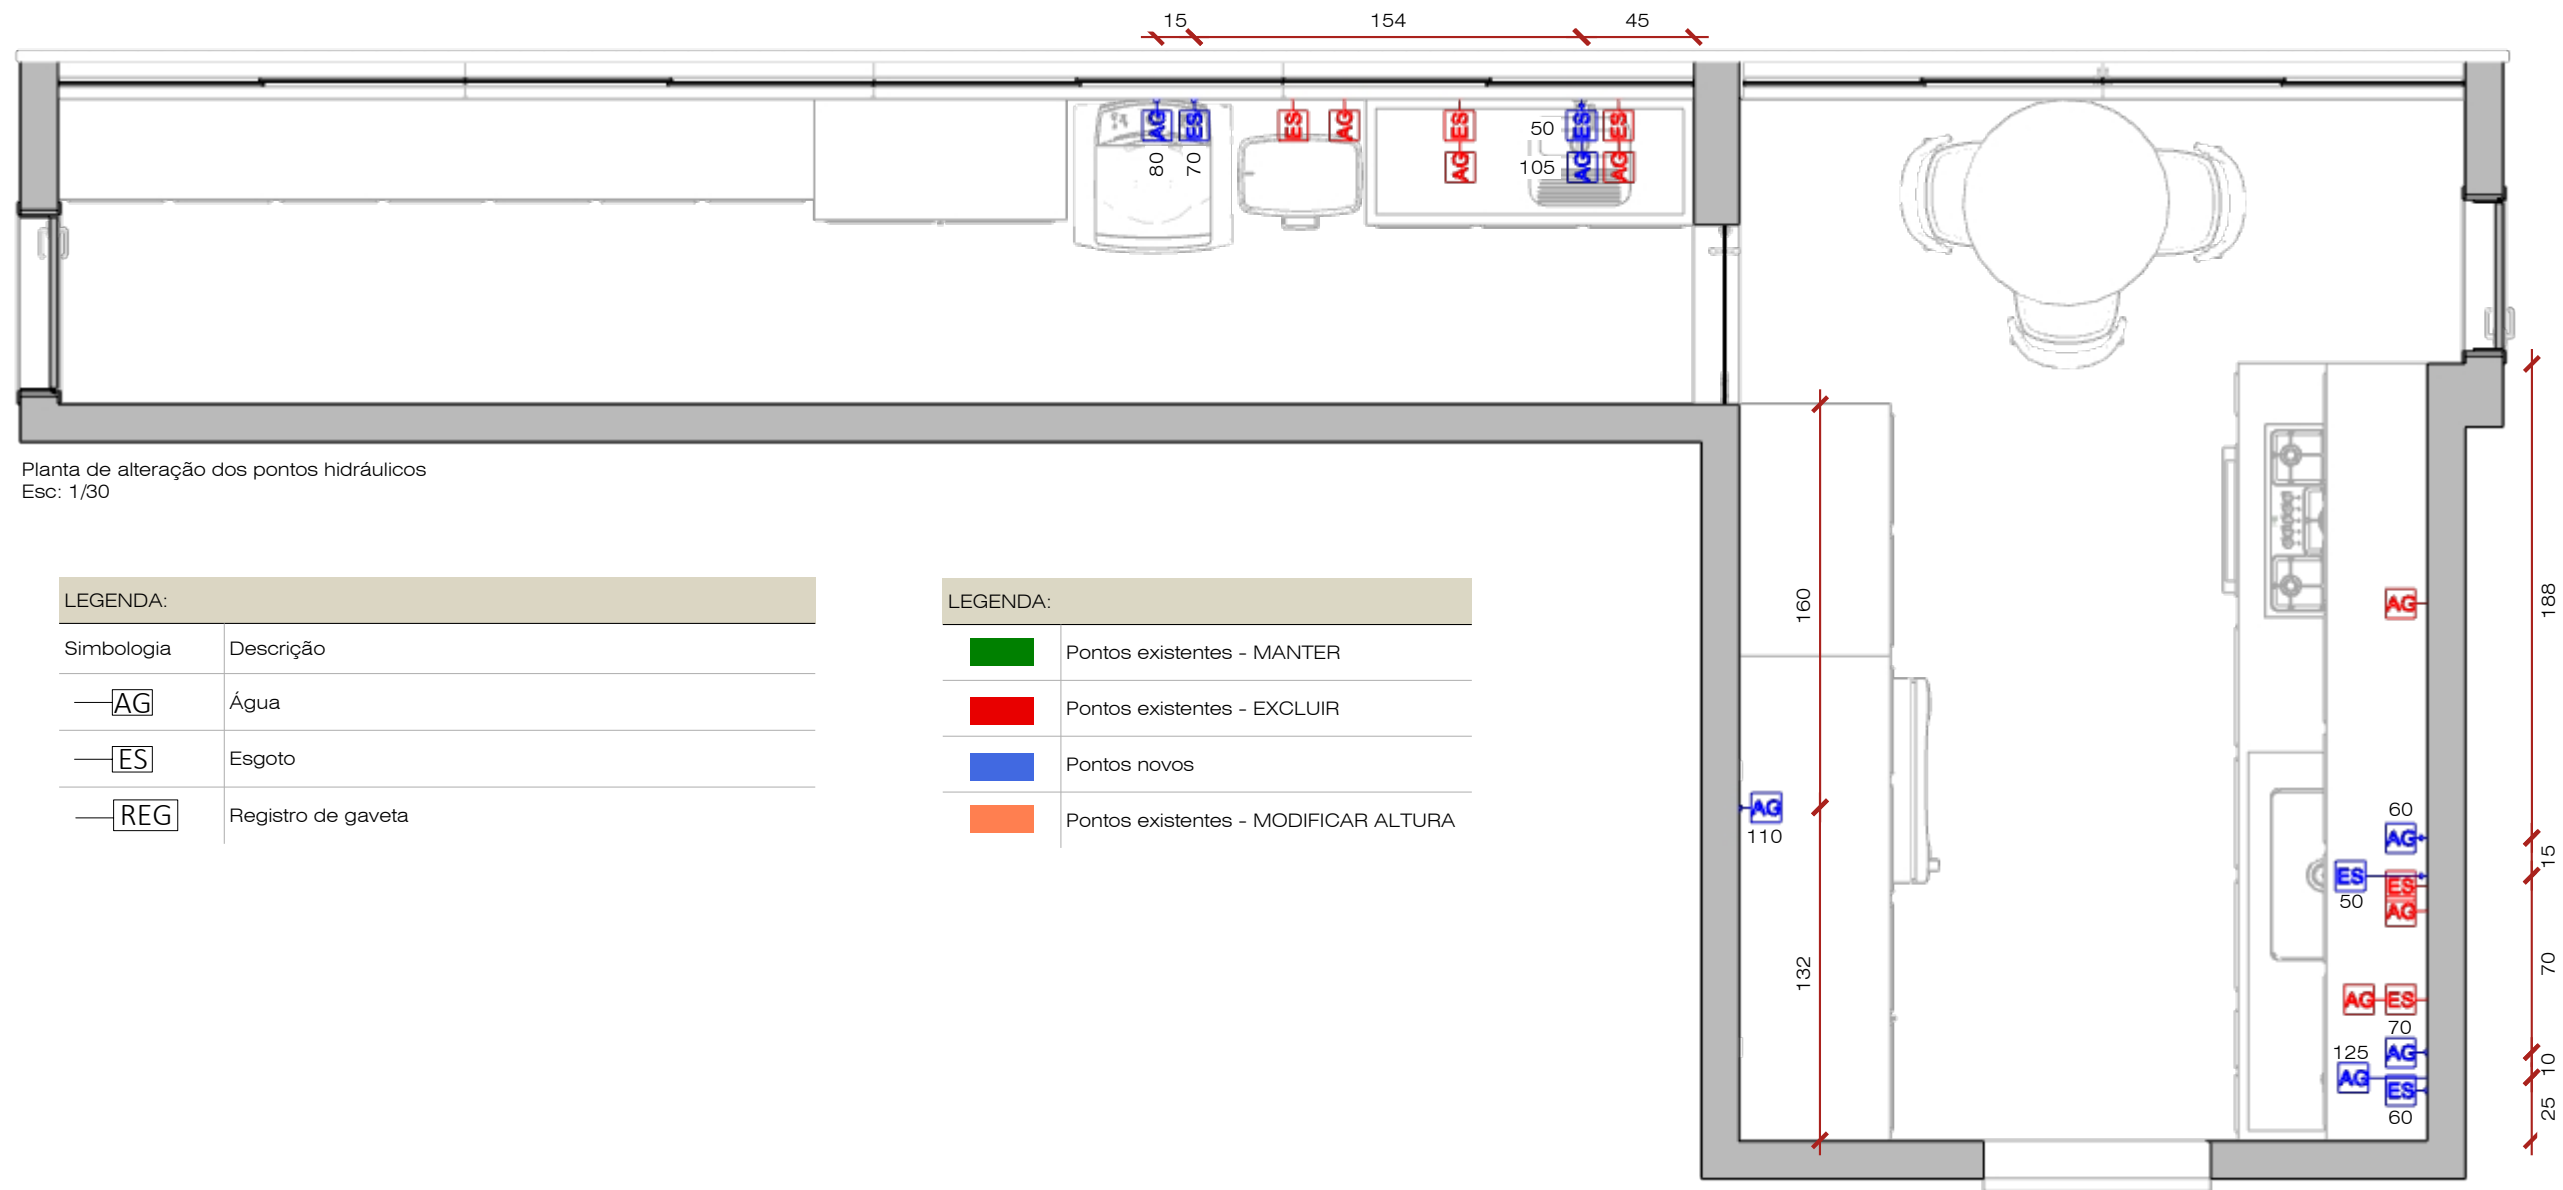

Planta de alteração dos pontos hidráulicos
Esc: 1/30

LEGENDA:	
Simbologia	Descrição
—AG	Água
—ES	Esgoto
—REG	Registro de gaveta

LEGENDA:	
	Pontos existentes - MANTER
	Pontos existentes - EXCLUIR
	Pontos novos
	Pontos existentes - MODIFICAR ALTURA

Cozinha e Área de Serviço

Desenhista: Nathália Rodrigues

As imagens 3D são meramente ilustrativa.
Seguir orientações conforme detalhamento executivo.

Todas as medidas devem ser conferidas no local antes da execução.

Clientes:
Silvana e Hélio

Endereço:
SQS 106 Bloco H, Apartamento 601.
Asa Sul

Data:
27.08.2026

Arquiteto coordenador

Alisson Correia
Celular (61) 98303-0582


Arquiteta responsável

Aline Coutinho Molina
CAU - A108129-2
Celular (61) 99606-5747

Obs: Todas as medidas em centímetros

12

Aline Molina
arquitetura de interiores

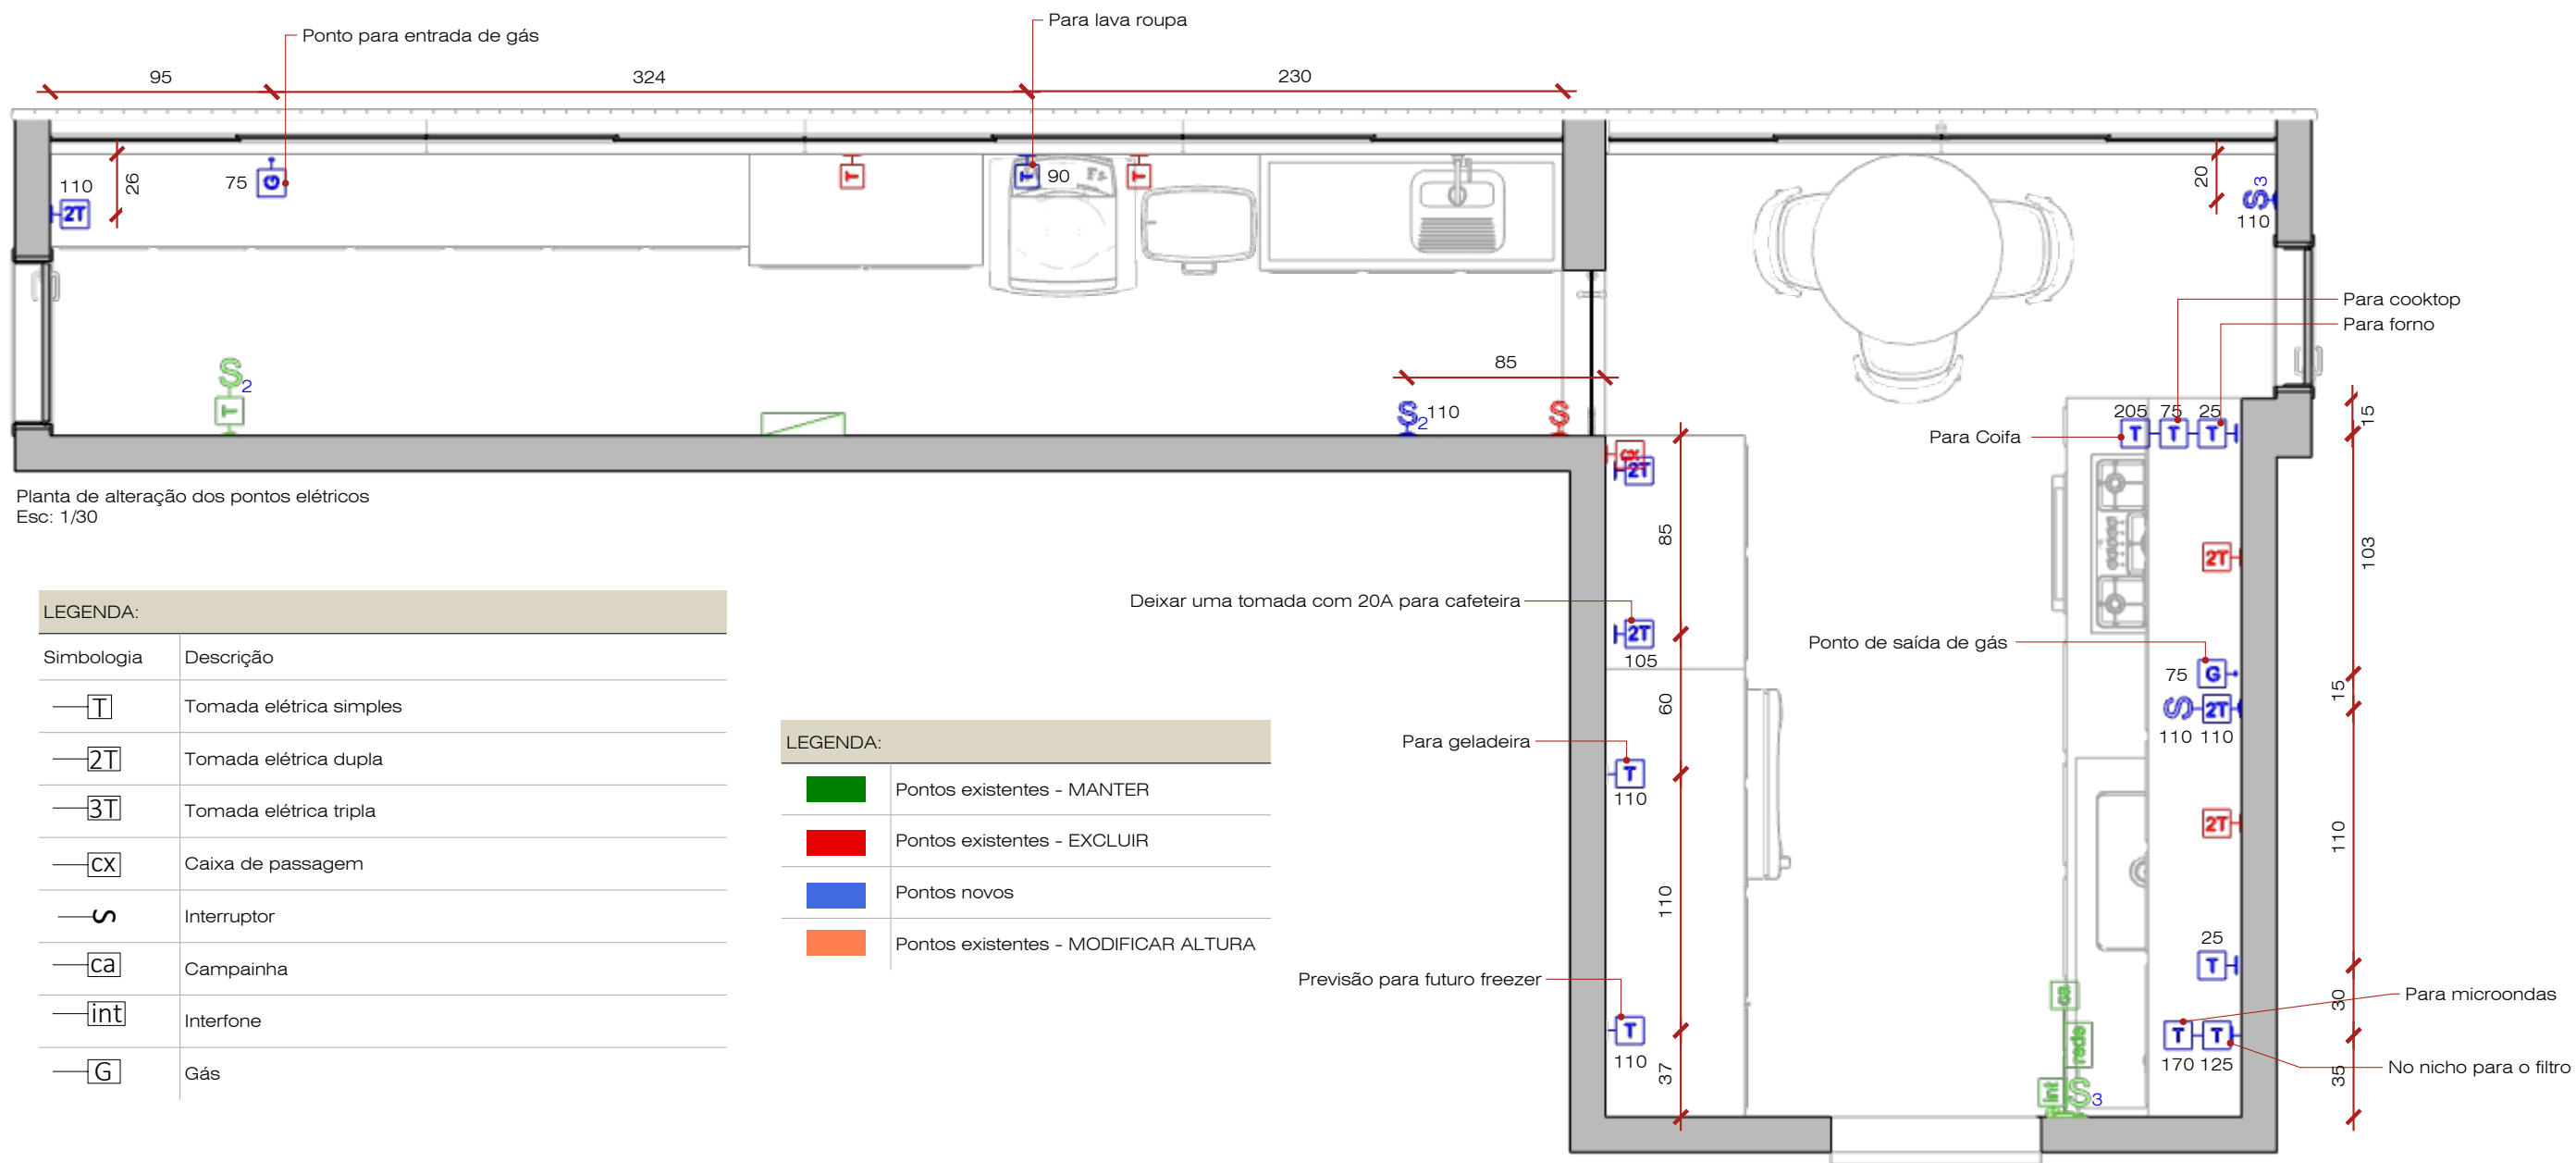

Planta de alteração dos pontos elétricos
Esc: 1/30

LEGENDA:	
Simbologia	Descrição
	Tomada elétrica simples
	Tomada elétrica dupla
	Tomada elétrica tripla
	Caixa de passagem
	Interruptor
	Campainha
	Interfone
	Gás

LEGENDA:	
	Pontos existentes - MANTER
	Pontos existentes - EXCLUIR
	Pontos novos
	Pontos existentes - MODIFICAR ALTURA

Cozinha e Área de Serviço

Desenhista: Nathália Rodrigues

As imagens 3D são meramente ilustrativa.
Seguir orientações conforme detalhamento executivo.

Todas as medidas devem ser conferidas no local antes da execução.

Clientes:
Silvana e Hélio

Endereço:
SQS 106 Bloco H, Apartamento 601.
Asa Sul

Data:
27.08.2026

Arquiteto coordenador

Alisson Correia
Celular (61) 98303-0582


Arquiteta responsável

Aline Coutinho Molina
CAU - A108129-2
Celular (61) 99606-5747

Obs: Todas as medidas em centímetros

13

Aline Molina
arquitetura de interiores

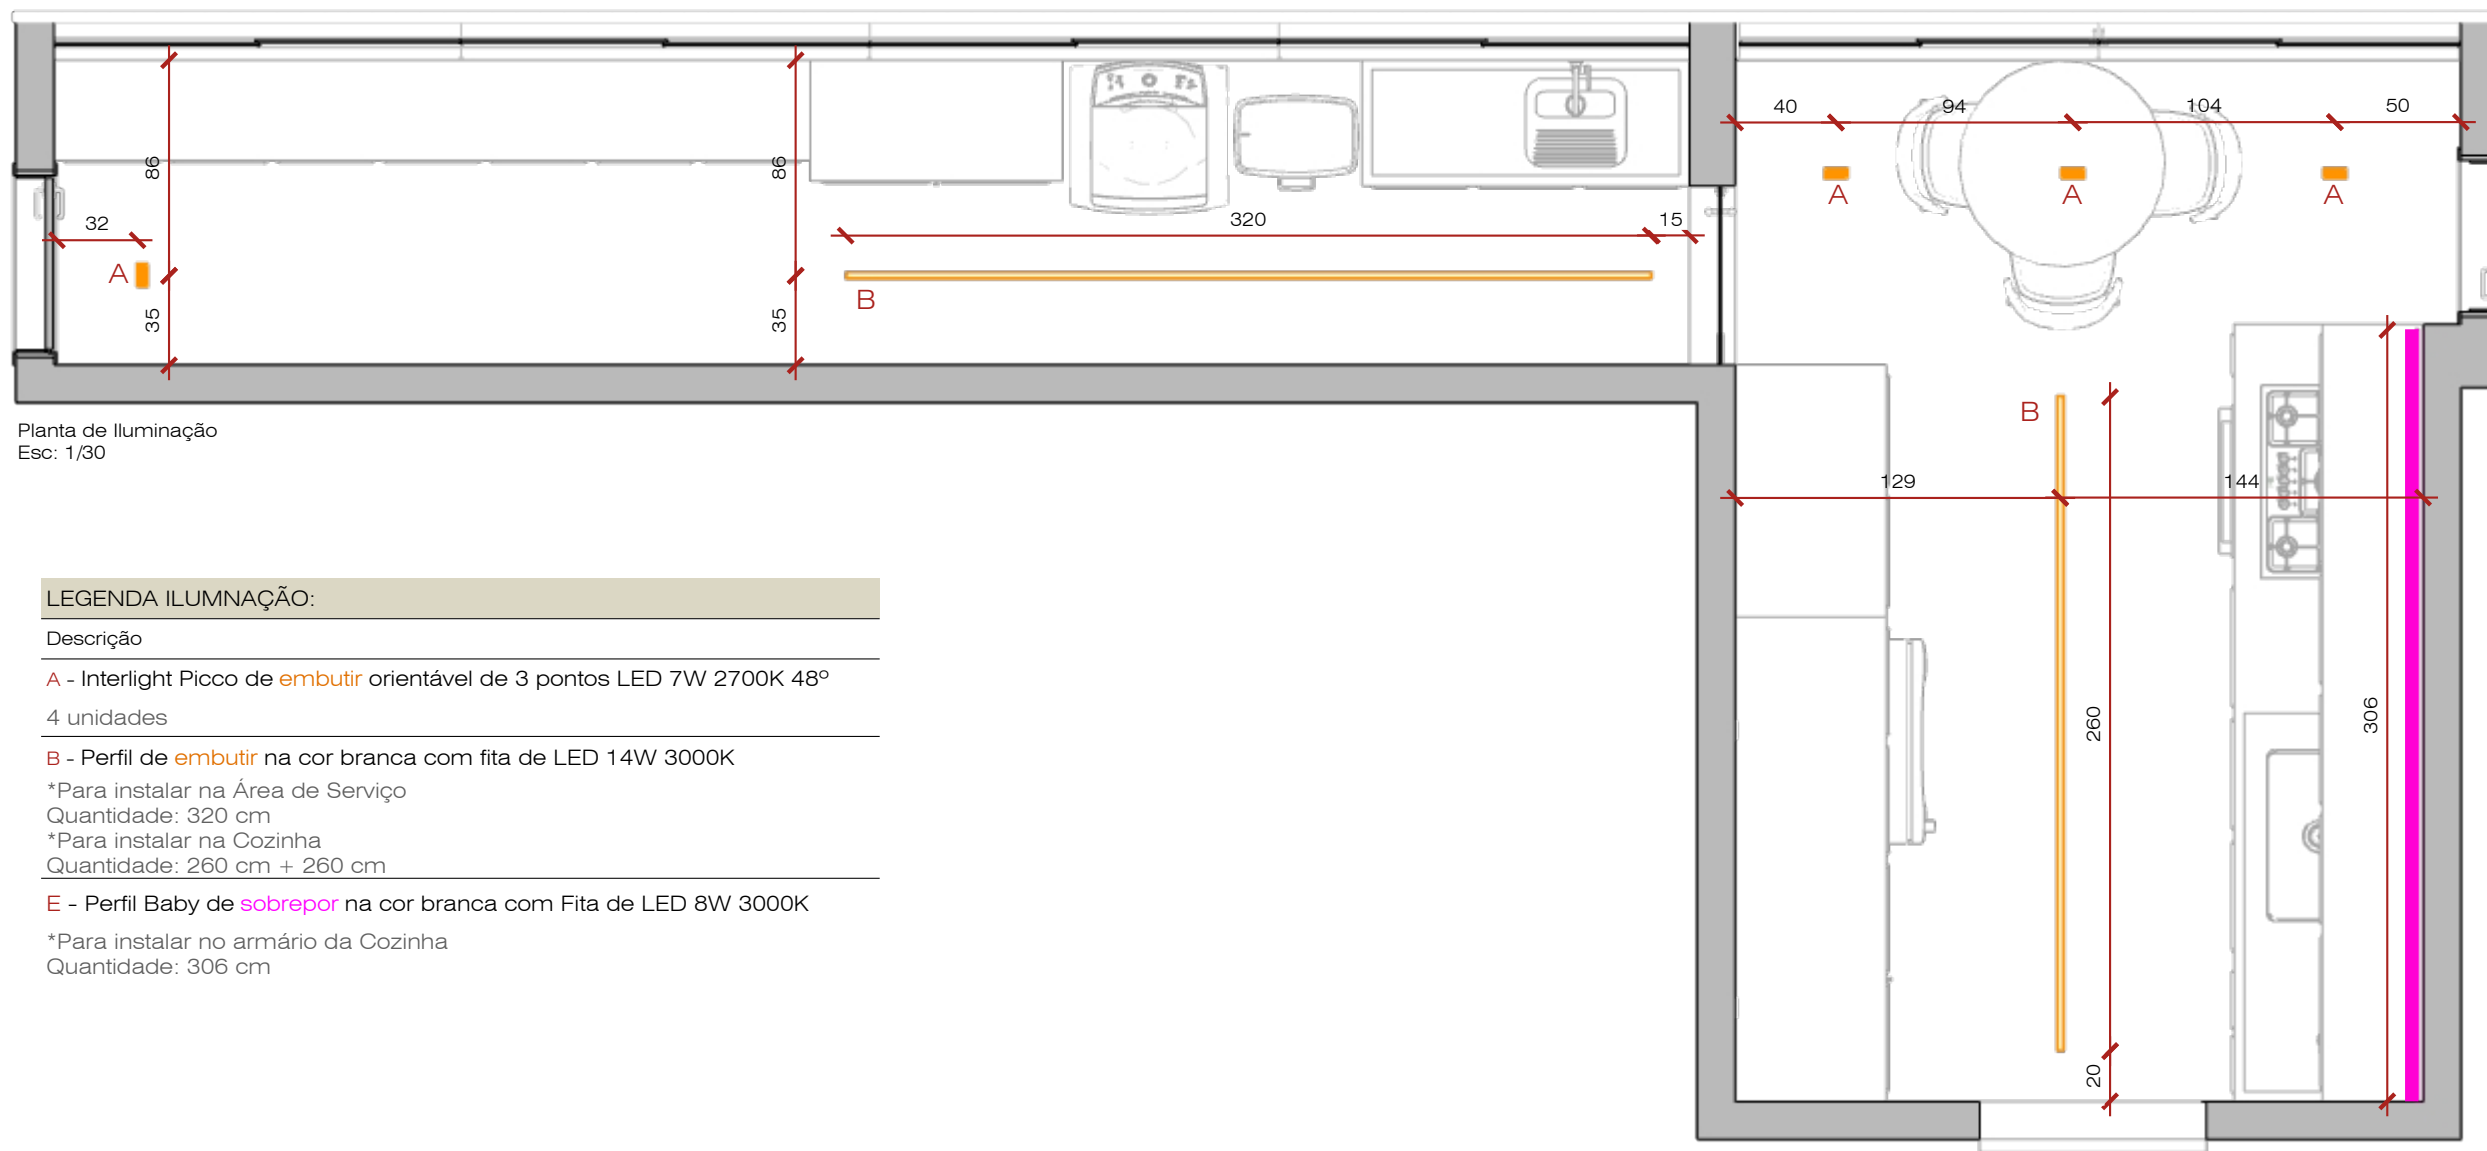

Planta de Iluminação
Esc: 1/30

LEGENDA ILUMNAÇÃO:

Descrição

A - Interlight Picco de **embutir** orientável de 3 pontos LED 7W 2700K 48°
4 unidades

B - Perfil de **embutir** na cor branca com fita de LED 14W 3000K
*Para instalar na Área de Serviço
Quantidade: 320 cm
*Para instalar na Cozinha
Quantidade: 260 cm + 260 cm

E - Perfil Baby de **sobrepôr** na cor branca com Fita de LED 8W 3000K
*Para instalar no armário da Cozinha
Quantidade: 306 cm

Cozinha e Área de Serviço

Desenhista: Nathália Rodrigues

As imagens 3D são meramente ilustrativa.
Seguir orientações conforme detalhamento executivo.

Todas as medidas devem ser conferidas no local antes da execução.

Clientes:
Silvana e Hélio

Endereço:
SQS 106 Bloco H, Apartamento 601.
Asa Sul

Data:
27.08.2026

Arquiteto coordenador

Alisson Correia
Celular (61) 98303-0582


Arquiteta responsável

Aline Coutinho Molina
CAU - A108129-2
Celular (61) 99606-5747


Obs: Todas as medidas em centímetros

14

Aline Molina
arquitetura de interiores

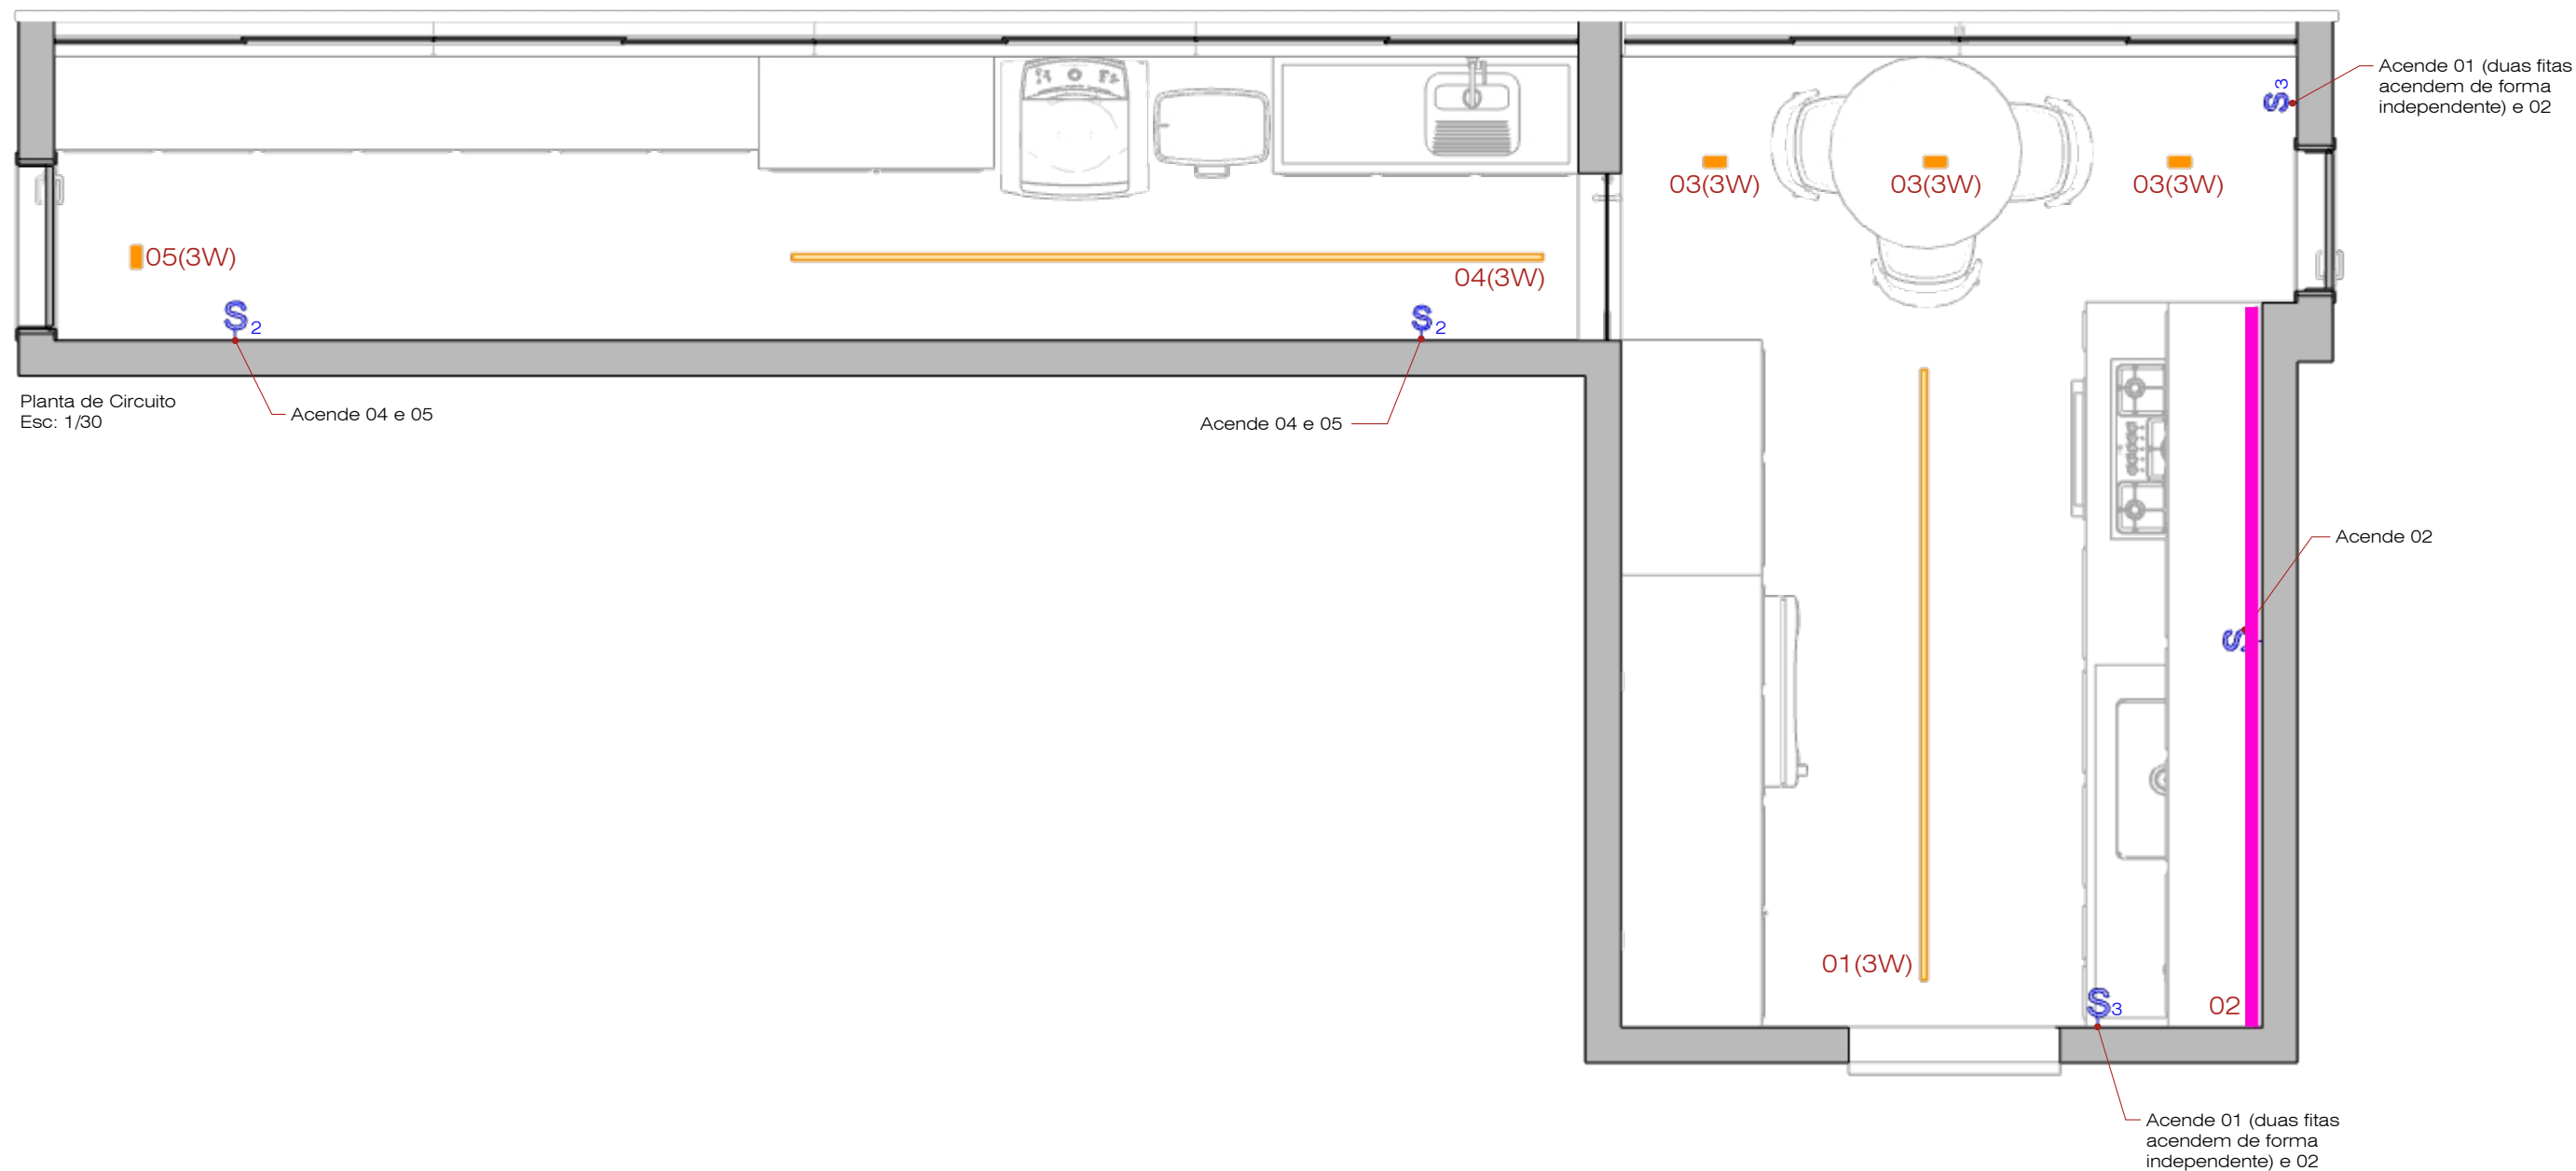

Cozinha e Área de Serviço

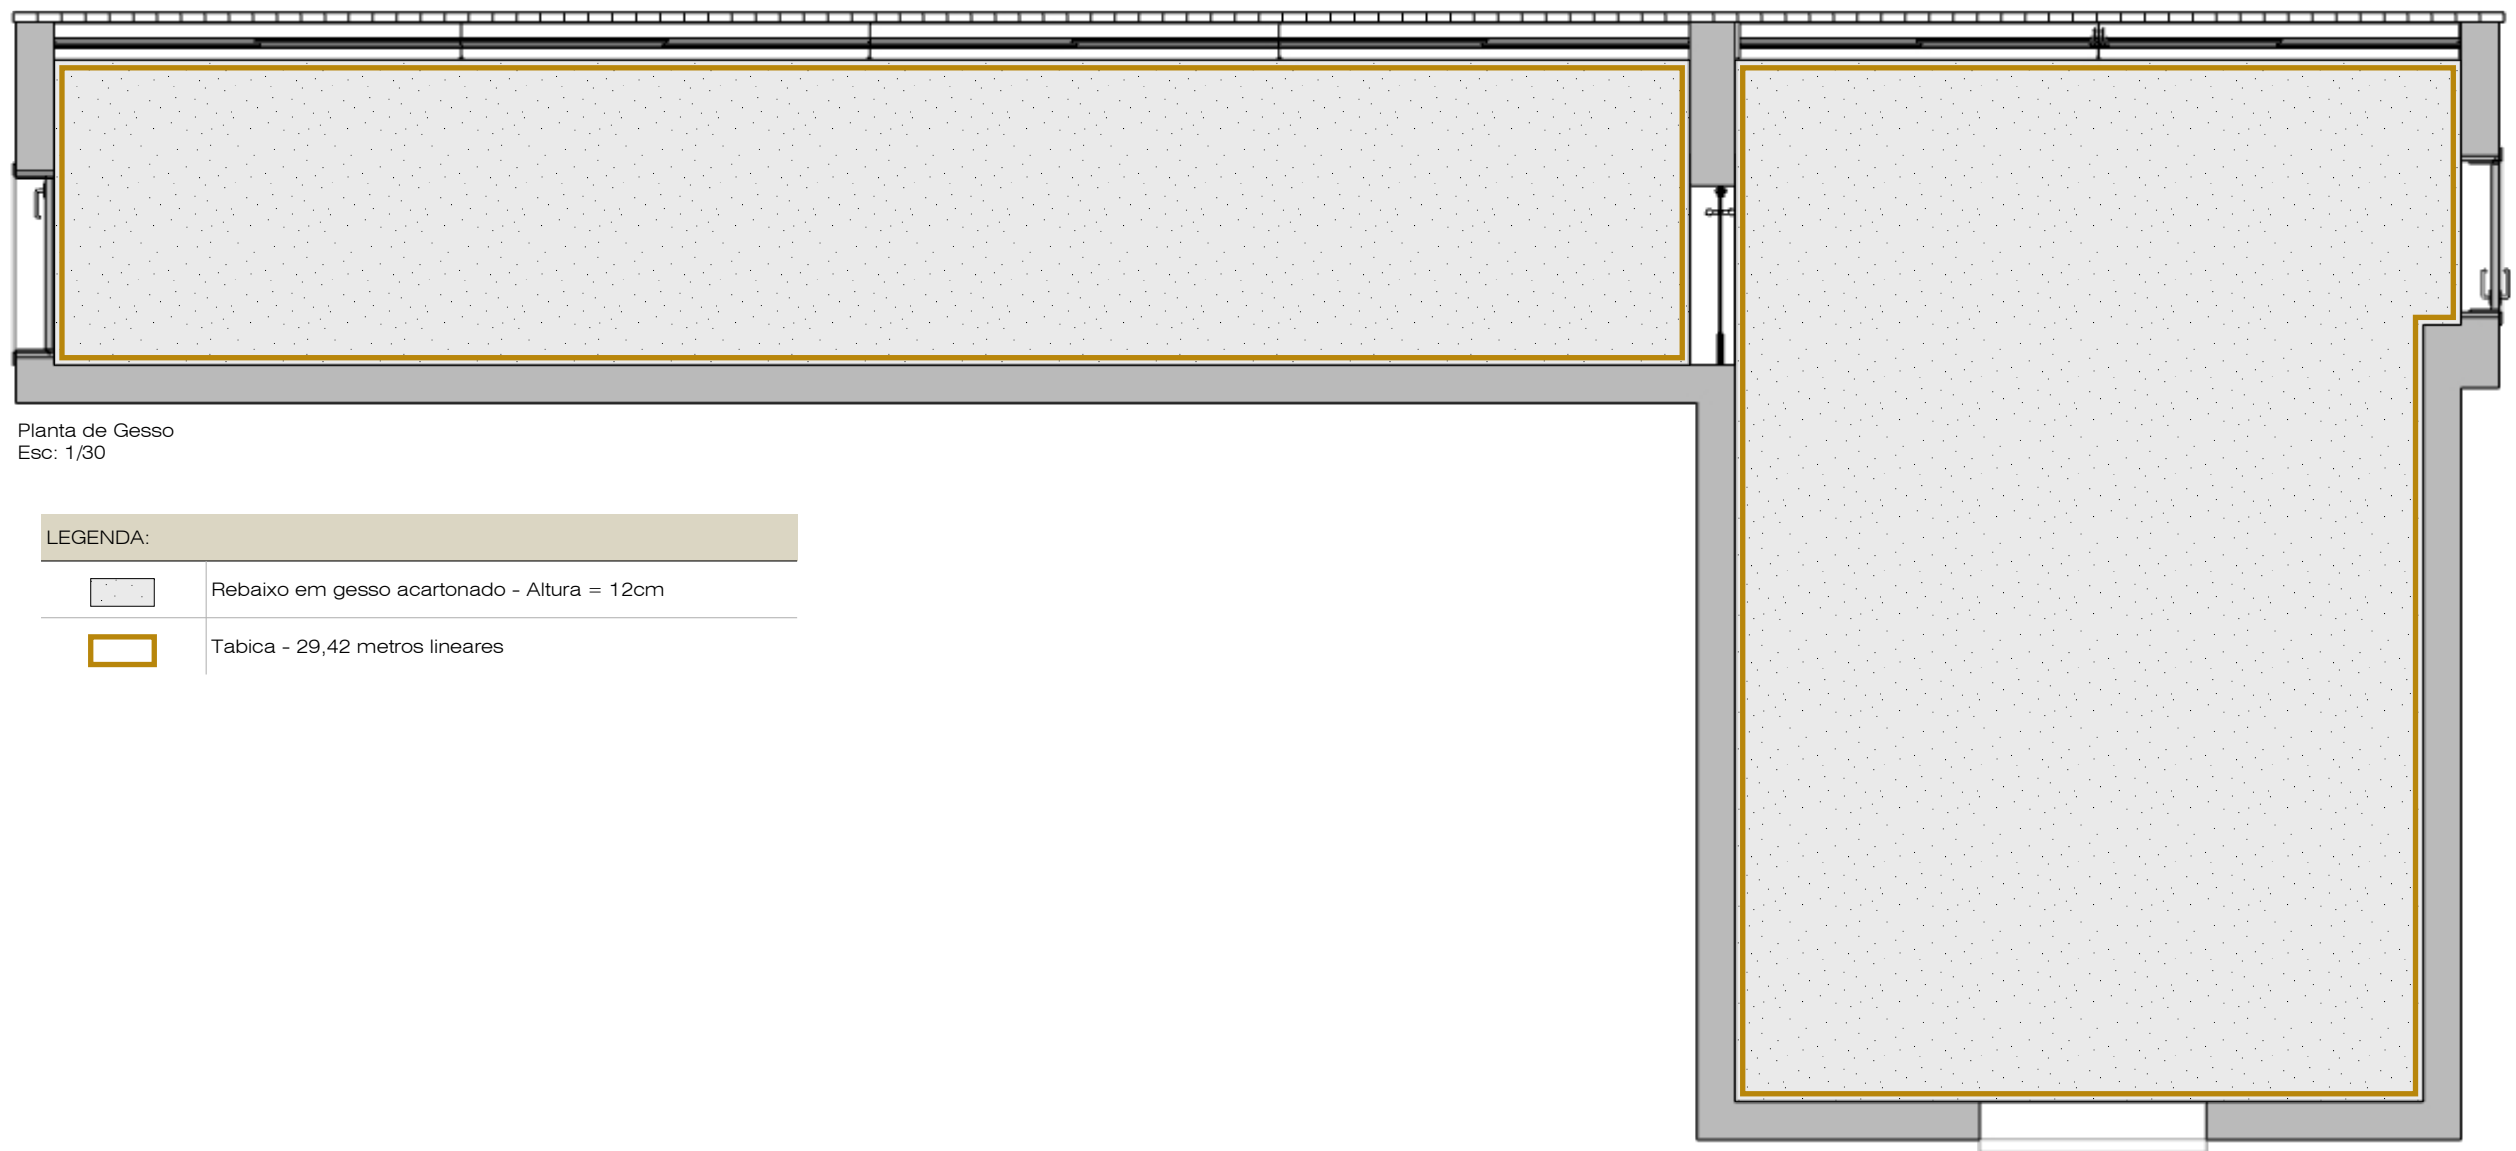

Planta de Gesso
Esc: 1/30

LEGENDA:



Rebaixo em gesso acartonado - Altura = 12cm



Tabica - 29,42 metros lineares

Cozinha e Área de Serviço

Desenhista: Nathália Rodrigues

As imagens 3D são meramente ilustrativa.
Seguir orientações conforme detalhamento executivo.

Todas as medidas devem ser conferidas no local antes da execução.

Clientes:
Silvana e Hélio

Endereço:
SQS 106 Bloco H, Apartamento 601.
Asa Sul

Data:
27.08.2026

Arquiteto coordenador

Alisson Correia
Celular (61) 98303-0582

Arquiteta responsável

Aline Coutinho Molina
CAU - A108129-2
Celular (61) 99606-5747

Obs: Todas as medidas em centímetros

16

Aline Molina
arquitetura de interiores

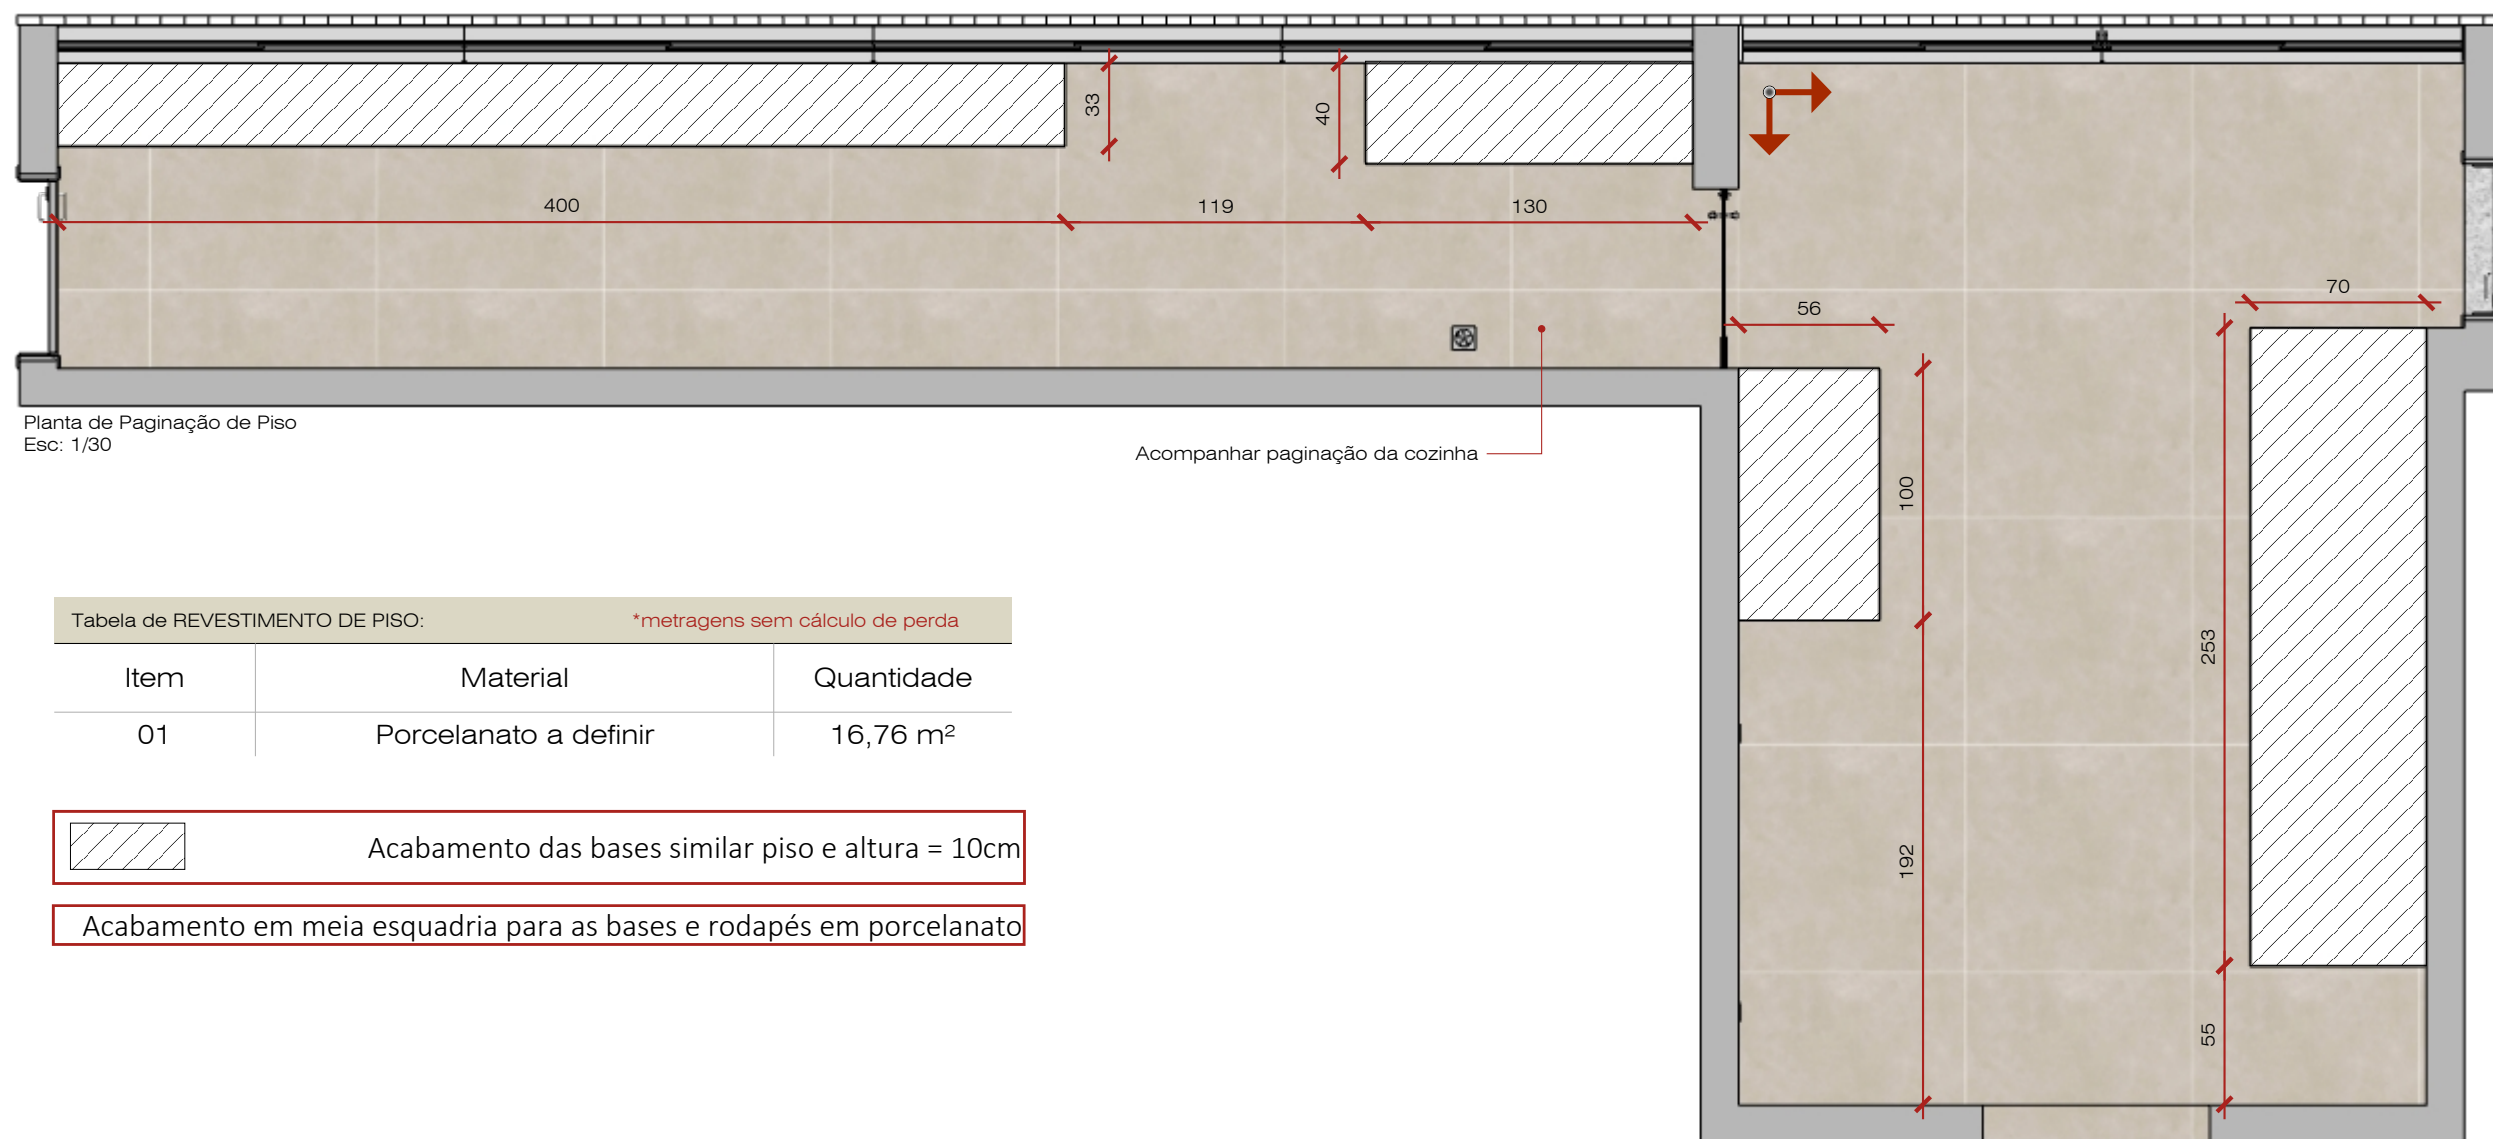


Tabela de REVESTIMENTO DE PISO: *metragens sem cálculo de perda

Item	Material	Quantidade
01	Porcelanato a definir	16,76 m²

Cozinha e Área de Serviço

Desenhista: Nathália Rodrigues

As imagens 3D são meramente ilustrativa.
Seguir orientações conforme detalhamento executivo.

Todas as medidas devem ser conferidas no local antes da execução.

Clientes:
Silvana e Hélio

Endereço:
SQS 106 Bloco H, Apartamento 601.
Asa Sul

Data:
27.08.2026

Arquiteto coordenador

Alisson Correia
Celular (61) 98303-0582


Arquiteta responsável

Aline Coutinho Molina
CAU - A108129-2
Celular (61) 99606-5747

Obs: Todas as medidas em centímetros

17

Aline Molina
arquitetura de interiores

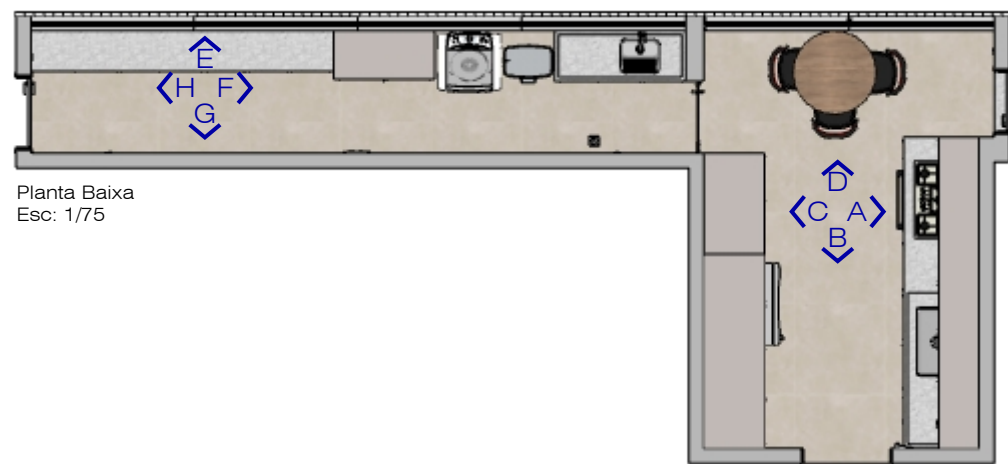


Planta Baixa
Esc: 1/75



Imagem 3D - Sem escala




Imagem de referência puxador New Facetatto

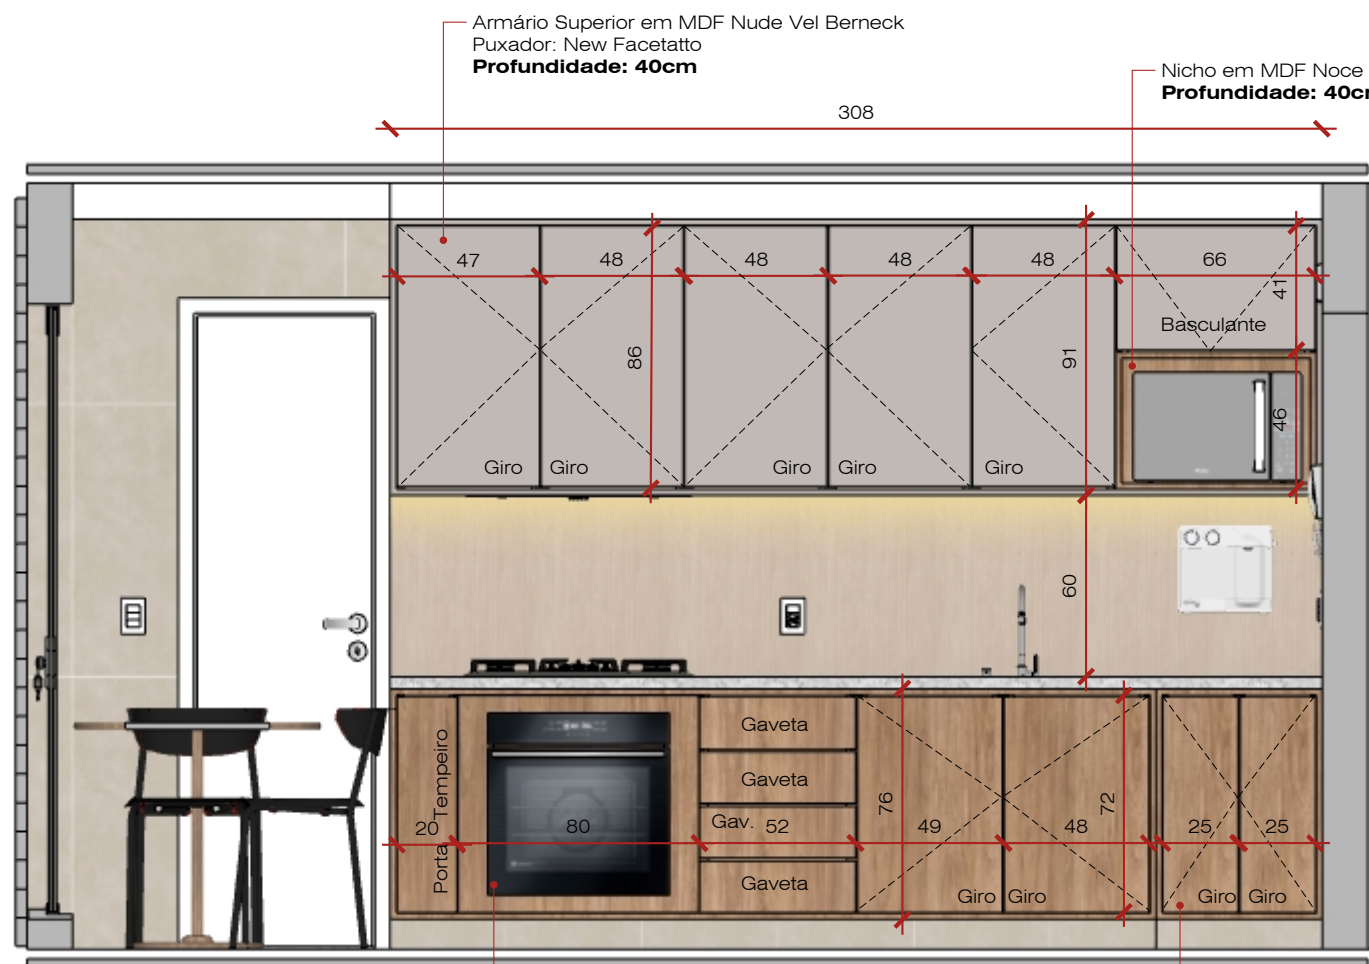

Vista A - Cozinha - Marcenaria Externa
Esc: 1/25

Armário Inferior em MDF Noce Amêndoa Duratex.
Puxador: New Facetatto
Profundidade: 75cm

Módulo separado para
que consiga retirar só
ele no futuro

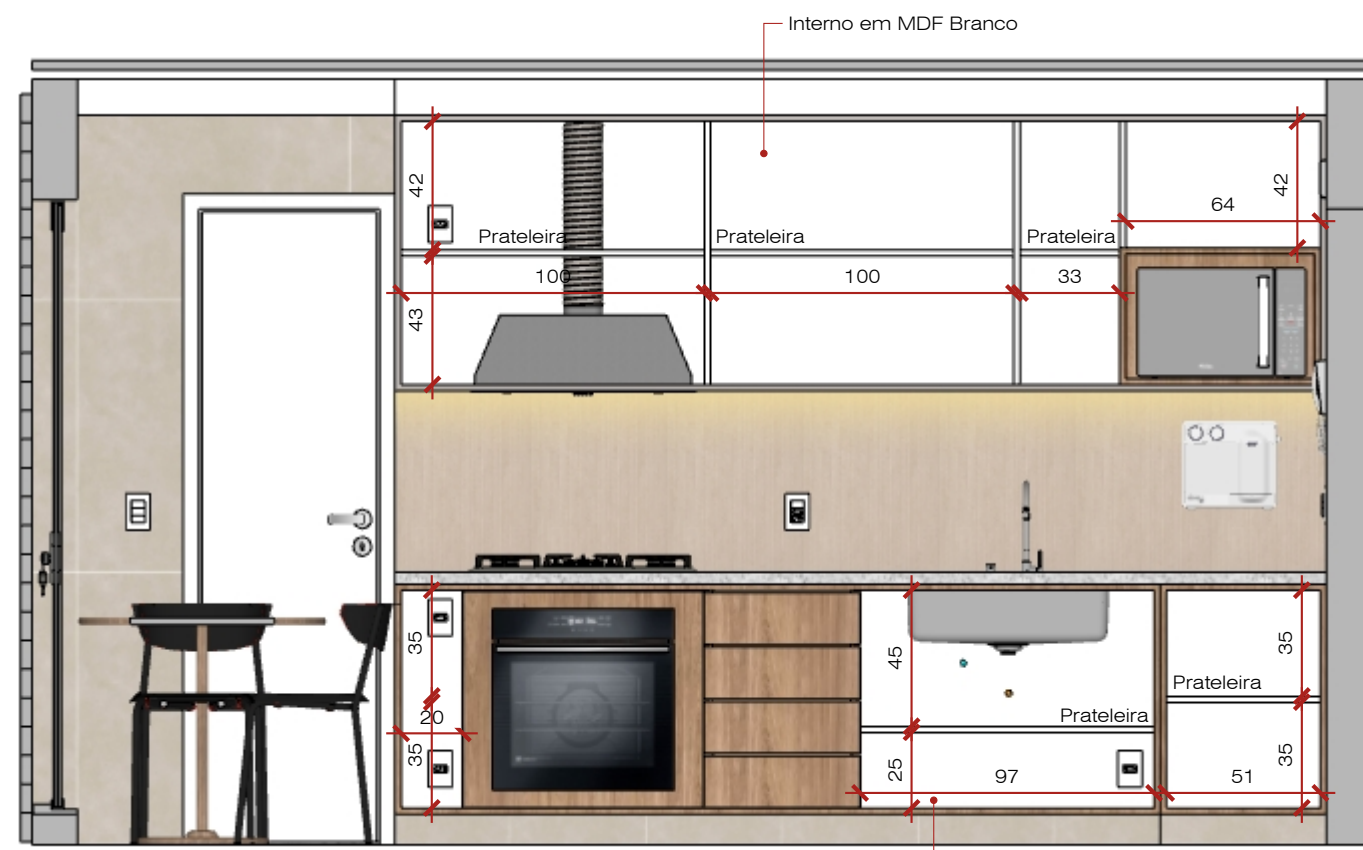

Vista A - Cozinha - Marcenaria Interna
Esc: 1/25

Interno em MDF Branco

Cozinha e Área de Serviço

Desenhista: Nathália Rodrigues

As imagens 3D são meramente ilustrativa.
Seguir orientações conforme detalhamento executivo.

Todas as medidas devem ser conferidas no local antes da execução.

Clientes:
Silvana e Hélio

Endereço:
SQS 106 Bloco H, Apartamento 601.
Asa Sul

Data:
27.08.2026

Arquiteto coordenador

Alisson Correia
Celular (61) 98303-0582


Arquiteta responsável

Aline Coutinho Molina
CAU - A108129-2
Celular (61) 99606-5747


18

Aline Molina
arquitetura de interiores


Obs: Todas as medidas em centímetros

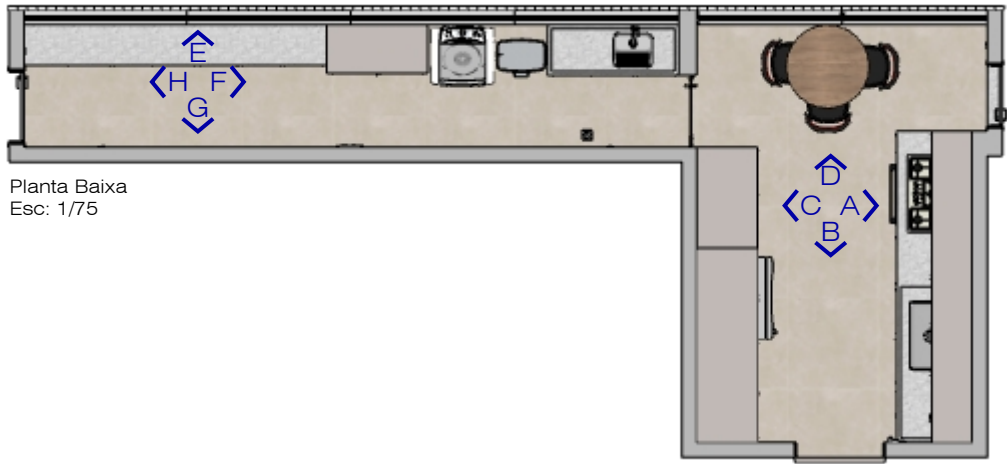


Planta Baixa
Esc: 1/75

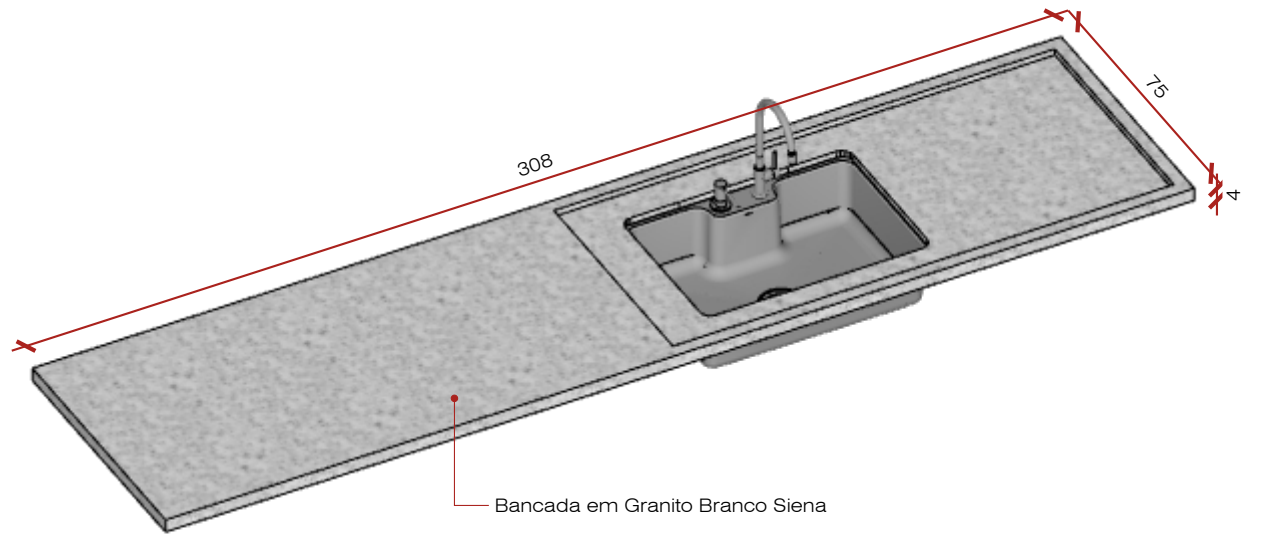

Vista A - Detalhe - Marmoraria
Esc: 1/25

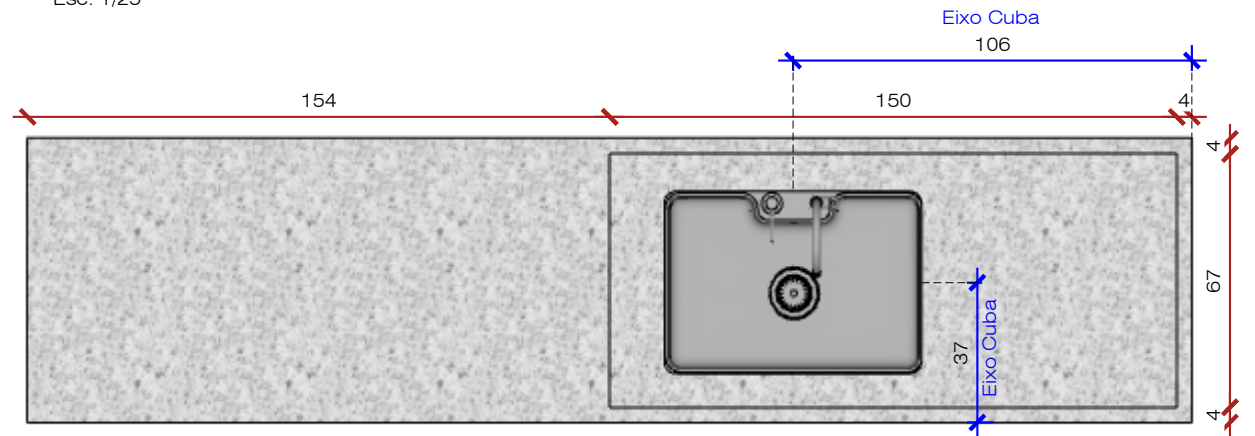

Vista A - Detalhe - Marmoraria
Esc: 1/25

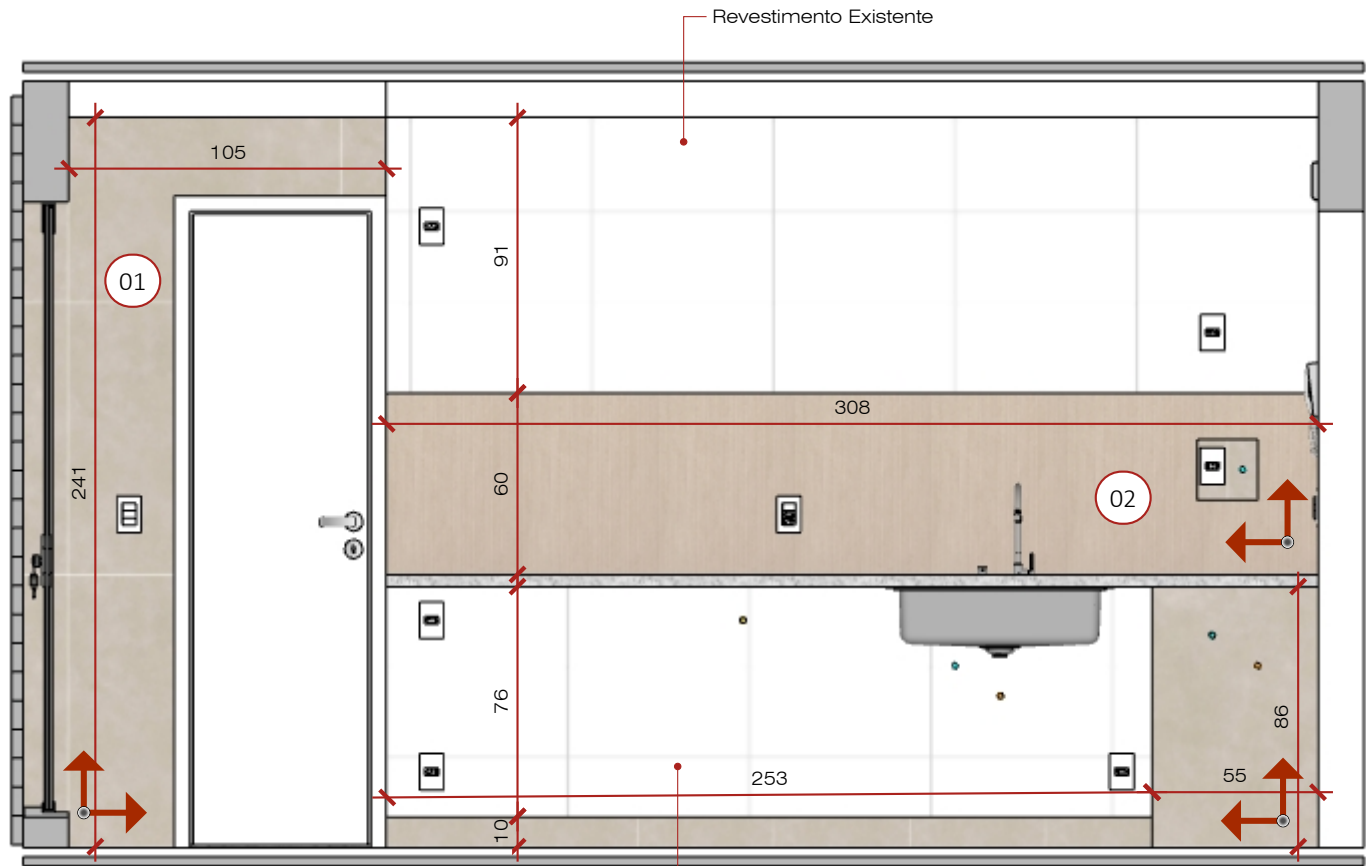

Vista A - Cozinha - Paginação
Esc: 1/25

Tabela de REVESTIMENTO DE PAREDE:

*metragens sem cálculo de perda

Item	Material	Quantidade
01	Porcelanato a definir	38,79 m²
02	Rev. Oasi Duna Ripa 45x120 Mate Retificado - Portobello	1,99 m²

Tabela de LOUÇAS E METAIS:

Item	Material	Ambiente
01	Cuba Inox de embutir 68x48 Docolmassima	Cozinha
02	Misturador Monocomado Cozinha Mesa Spice - Docol	Cozinha

Cozinha e Área de Serviço

Desenhista: Nathália Rodrigues

As imagens 3D são meramente ilustrativa.
Seguir orientações conforme detalhamento executivo.

Todas as medidas devem ser conferidas no local antes da execução.

Clientes:
Silvana e Hélio

Endereço:
SQS 106 Bloco H, Apartamento 601.
Asa Sul

Data:
27.08.2026

Arquiteto coordenador

Alisson Correia
Celular (61) 98303-0582


Arquiteta responsável

Aline Coutinho Molina
CAU - A108129-2
Celular (61) 99606-5747

Obs: Todas as medidas em centímetros

19

Aline Molina
arquitetura de interiores

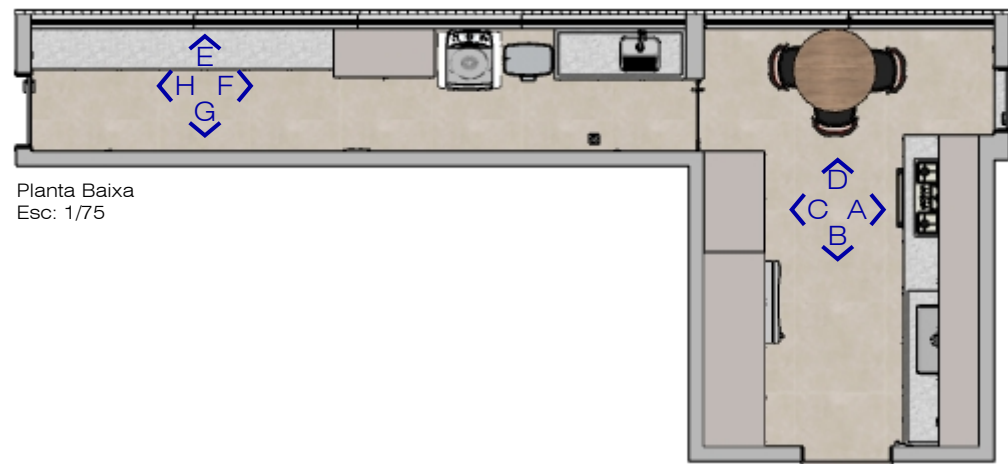

Planta Baixa
Esc: 1/75



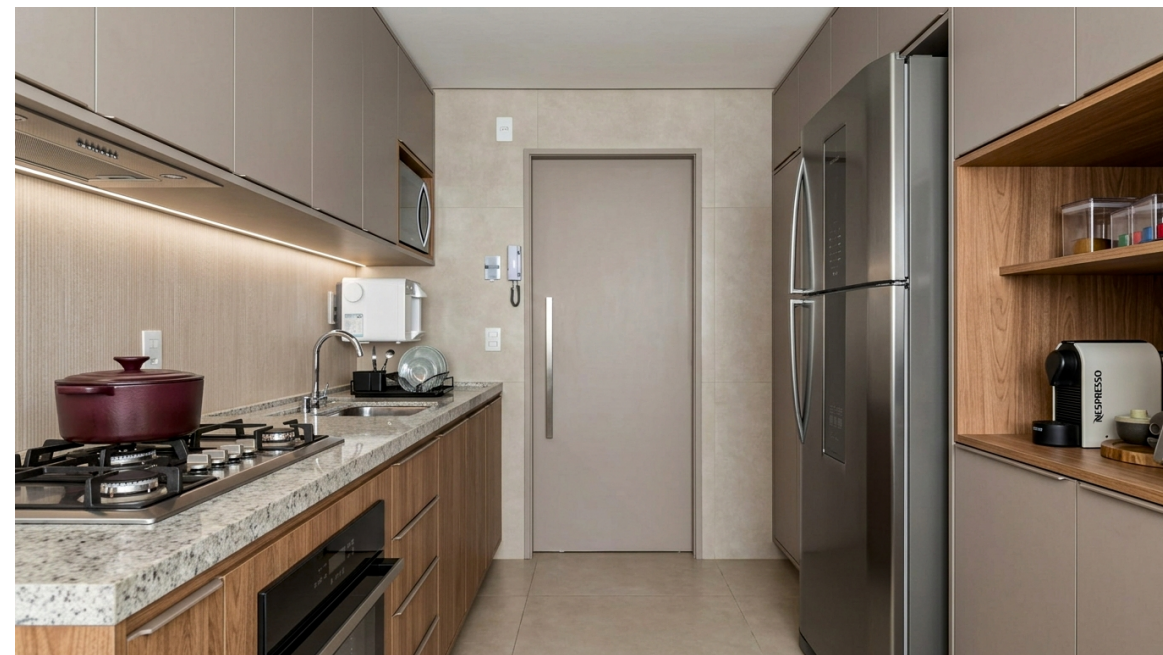


Imagem 3D - Sem escala

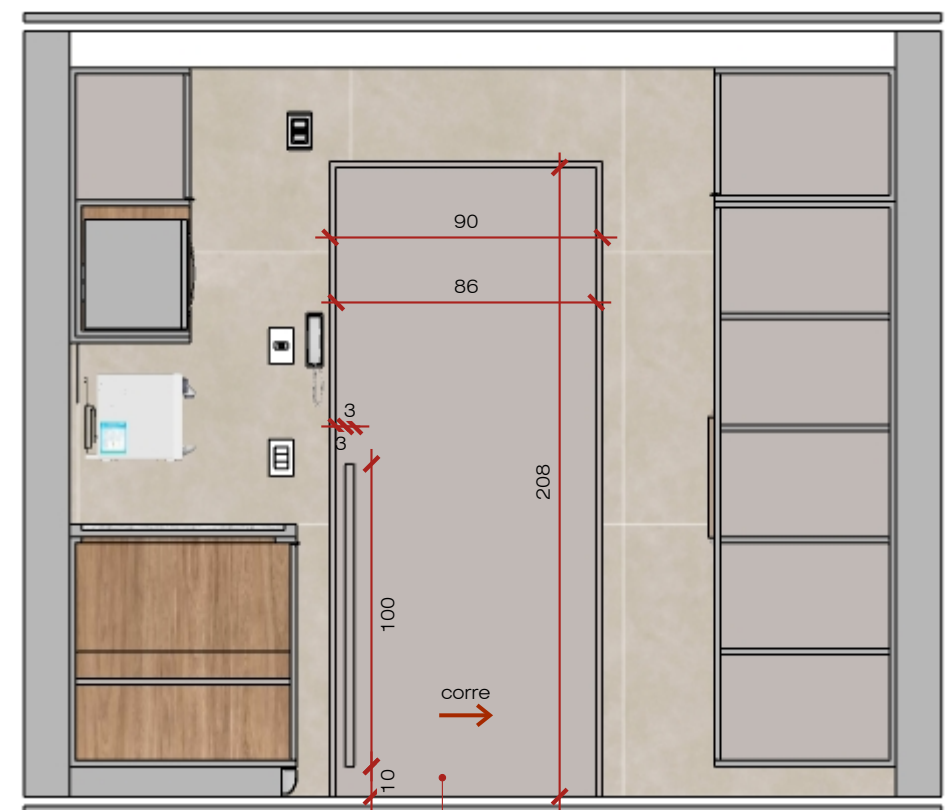

Vista B - Cozinha - Marcenaria
Esc: 1/25

Porta de correr (corre pelo lado do corredor) em MDF Nude Vel Berneck.
Puxador: Usinado na marcenaria

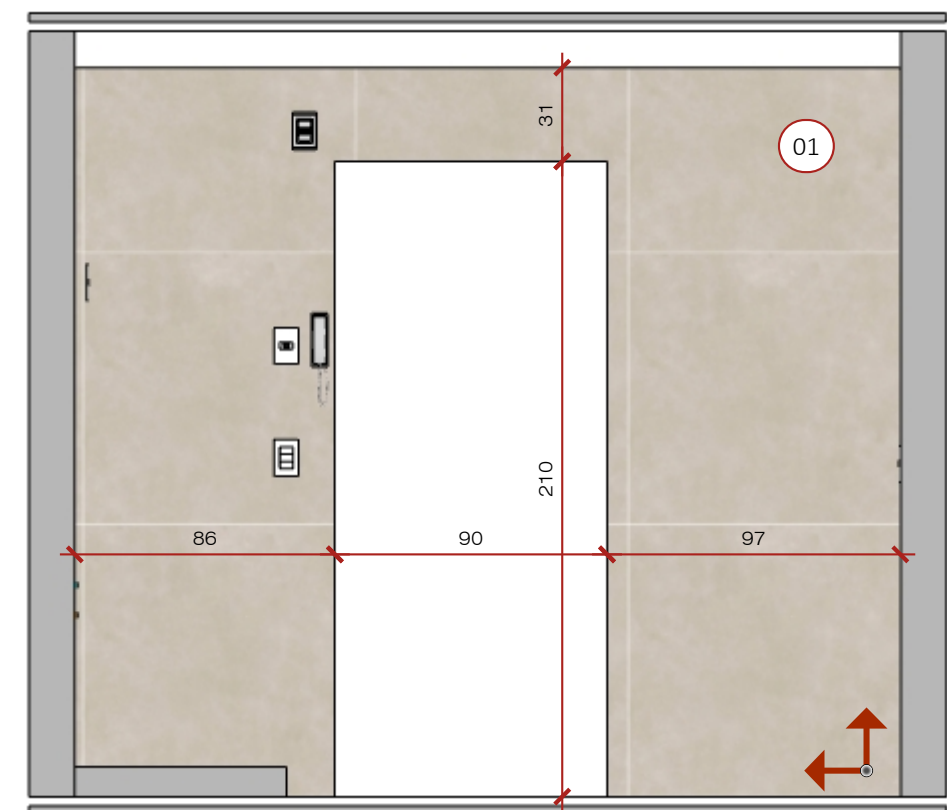

Vista B - Cozinha - Paginação
Esc: 1/25

Cozinha e Área de Serviço

Desenhista: Nathália Rodrigues

As imagens 3D são meramente ilustrativa.
Seguir orientações conforme detalhamento executivo.

Todas as medidas devem ser conferidas no local antes da execução.

Clientes:
Silvana e Hélio

Endereço:
SQS 106 Bloco H, Apartamento 601.
Asa Sul

Data:
27.08.2026

Arquiteto coordenador

Alisson Correia
Celular (61) 98303-0582


Arquiteta responsável

Aline Coutinho Molina
CAU - A108129-2
Celular (61) 99606-5747

Obs: Todas as medidas em centímetros

20

Aline Molina
arquitetura de interiores

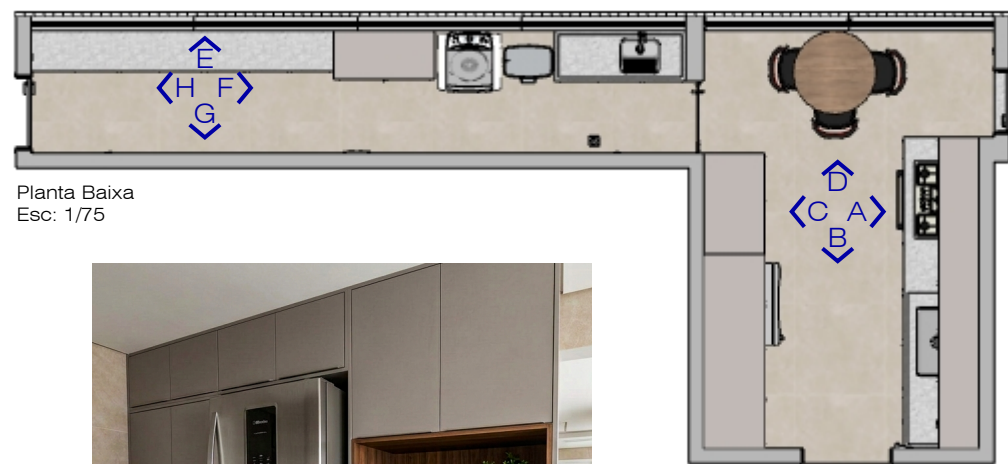

Planta Baixa
Esc: 1/75




Imagem 3D - Sem escala

Armário em MDF MDF Nude Vel Berneck.
Puxador: New Facetatto
Profundidade: 60cm


Nicho em MDF Noce Amêndoa Duratex.
Profundidade: 60cm

Armário (fazer módulo separado para sua retirada no futuro) em MDF Nude Vel Berneck.
Puxador: New Facetatto
Profundidade: 60cm


Armário em MDF MDF Nude Vel Berneck.
Puxador: New Facetatto
Profundidade: 60cm

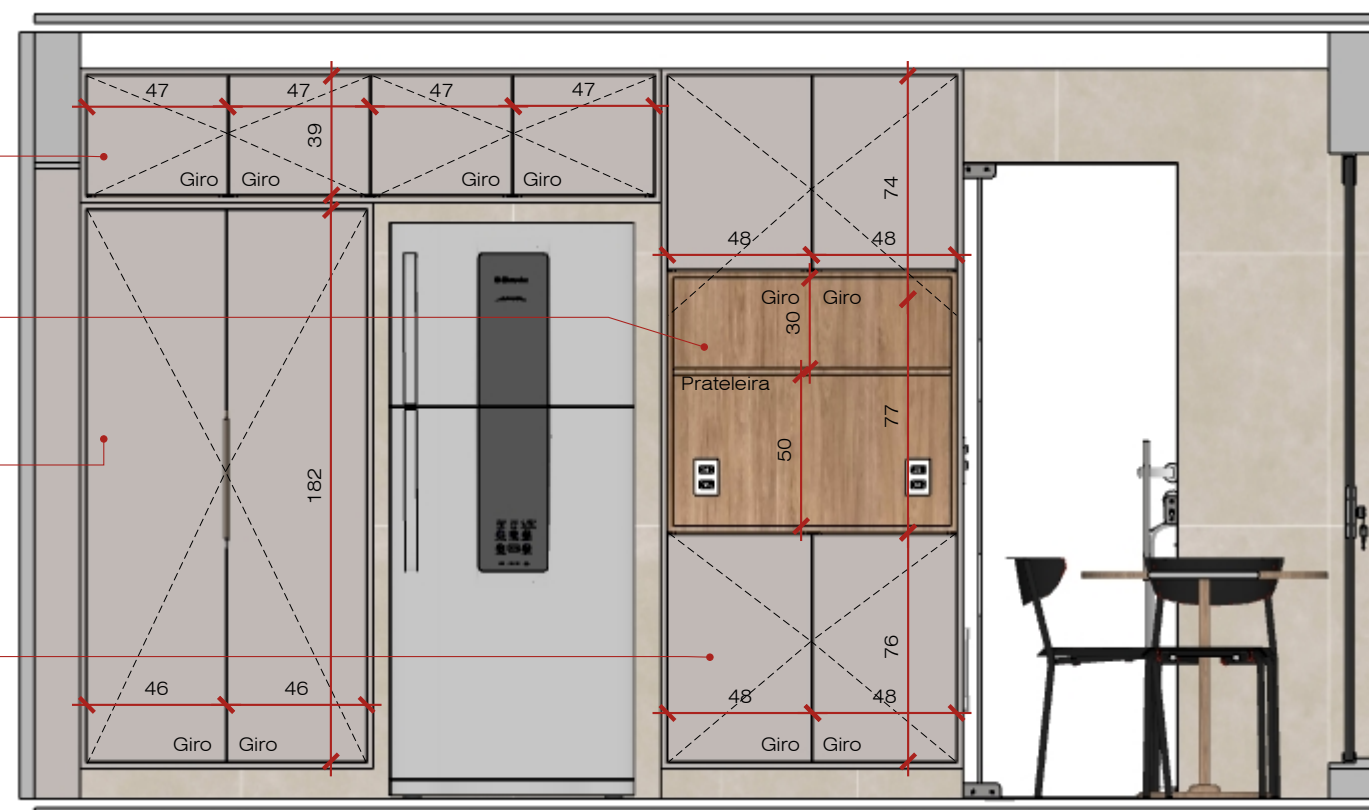

Vista C - Cozinha - Marcenaria Externa
Esc: 1/25

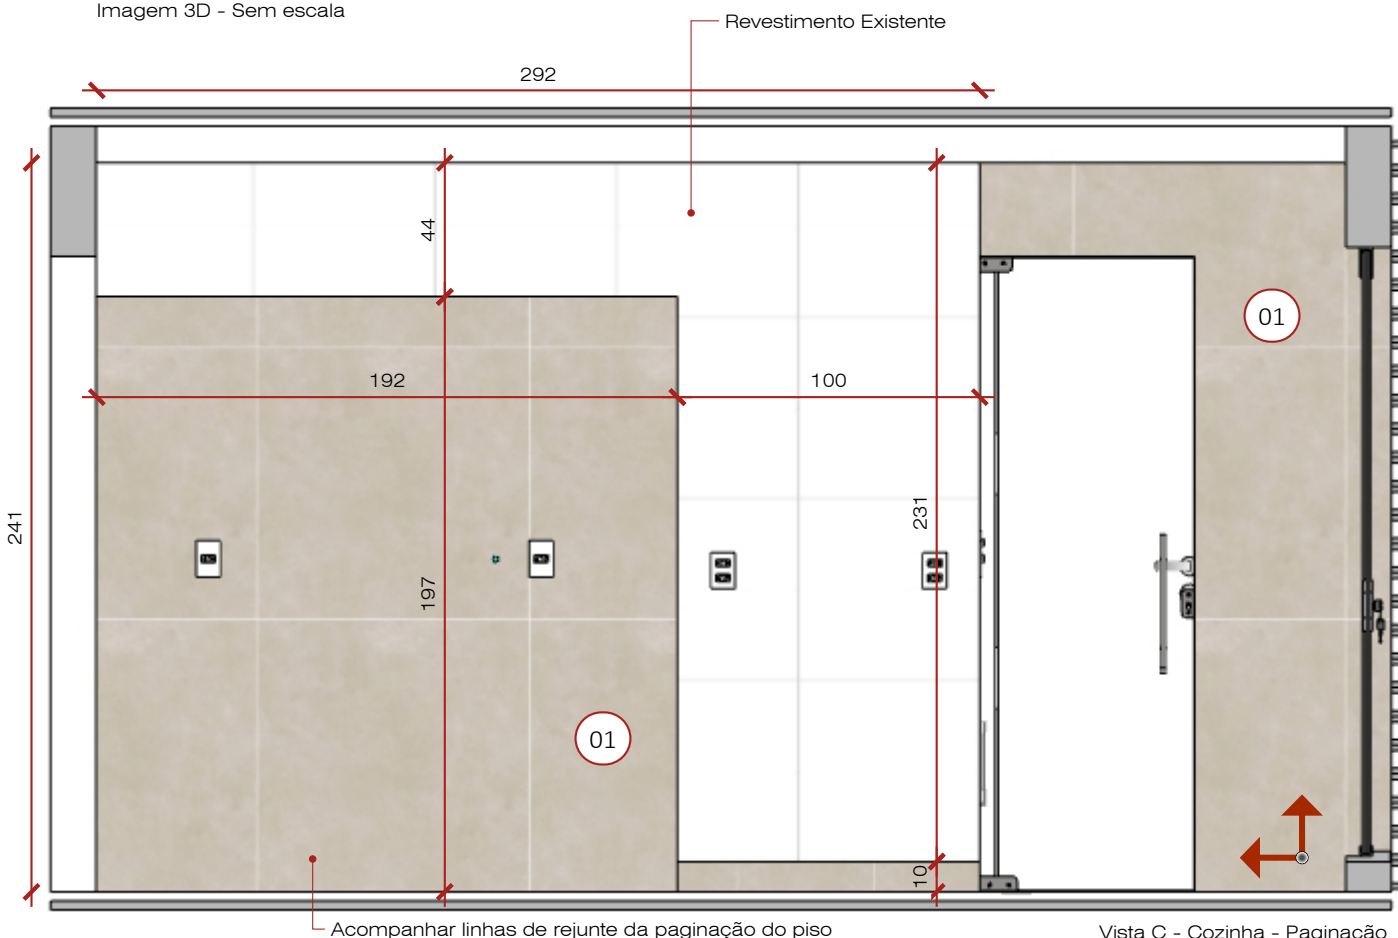

Vista C - Cozinha - Paginação
Esc: 1/25

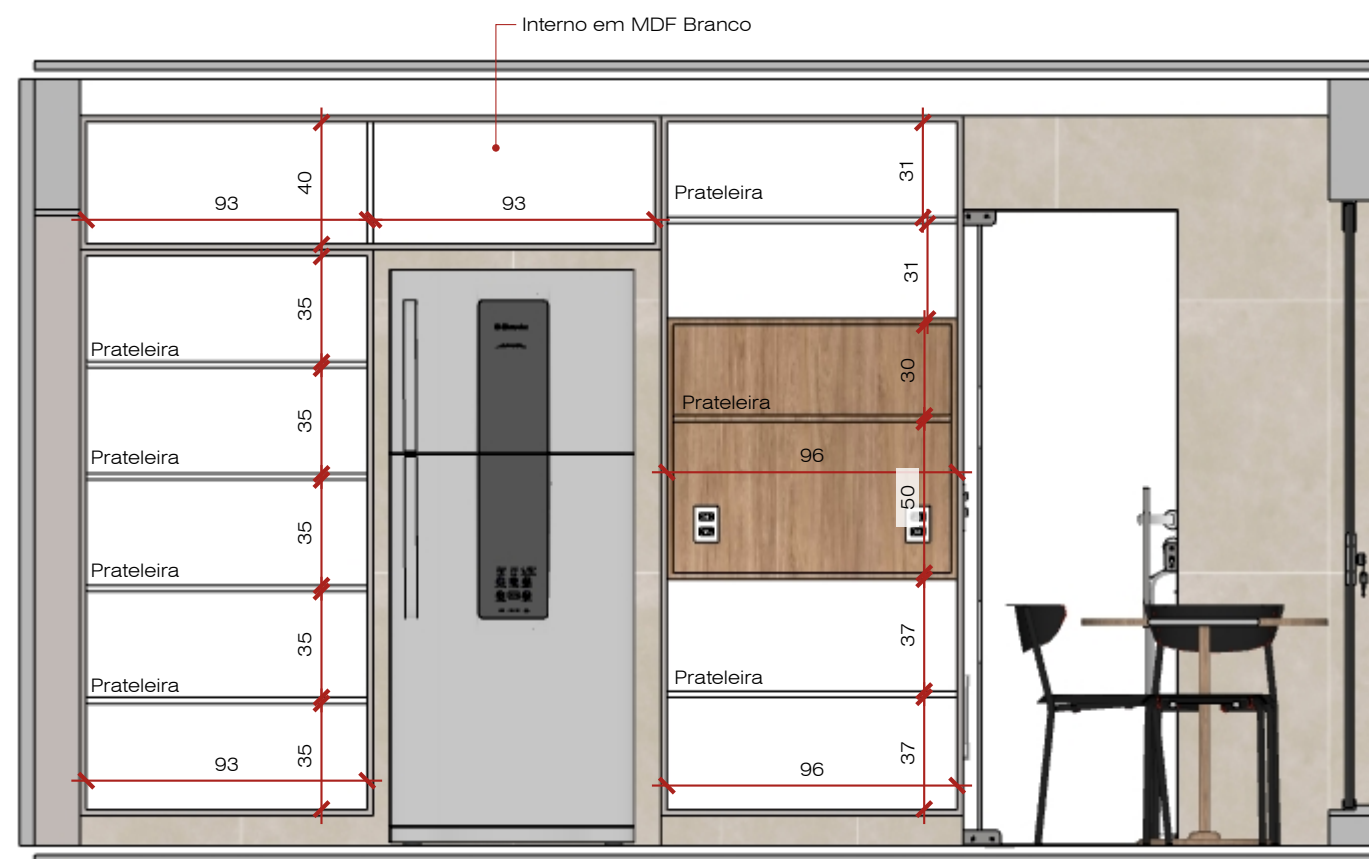

Vista C - Cozinha - Marcenaria Interna
Esc: 1/25

Cozinha e Área de Serviço

Desenhista: Nathália Rodrigues

As imagens 3D são meramente ilustrativa.
Seguir orientações conforme detalhamento executivo.

Todas as medidas devem ser conferidas no local antes da execução.

Clientes:
Silvana e Hélio

Endereço:
SQS 106 Bloco H, Apartamento 601.
Asa Sul

Data:
27.08.2026

Arquiteto coordenador

Alisson Correia
Celular (61) 98303-0582


Arquiteta responsável

Aline Coutinho Molina
CAU - A108129-2
Celular (61) 99606-5747


Obs: Todas as medidas em centímetros

21

Aline Molina
arquitetura de interiores

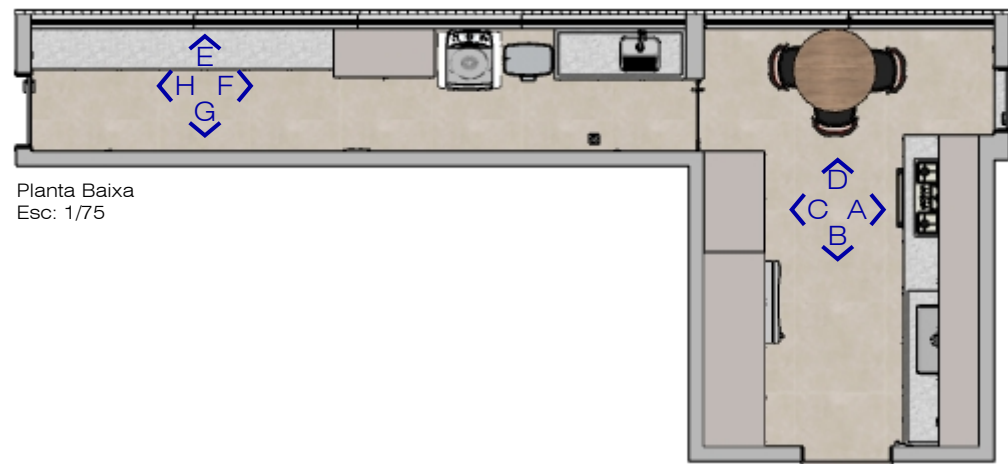

Planta Baixa
Esc: 1/75

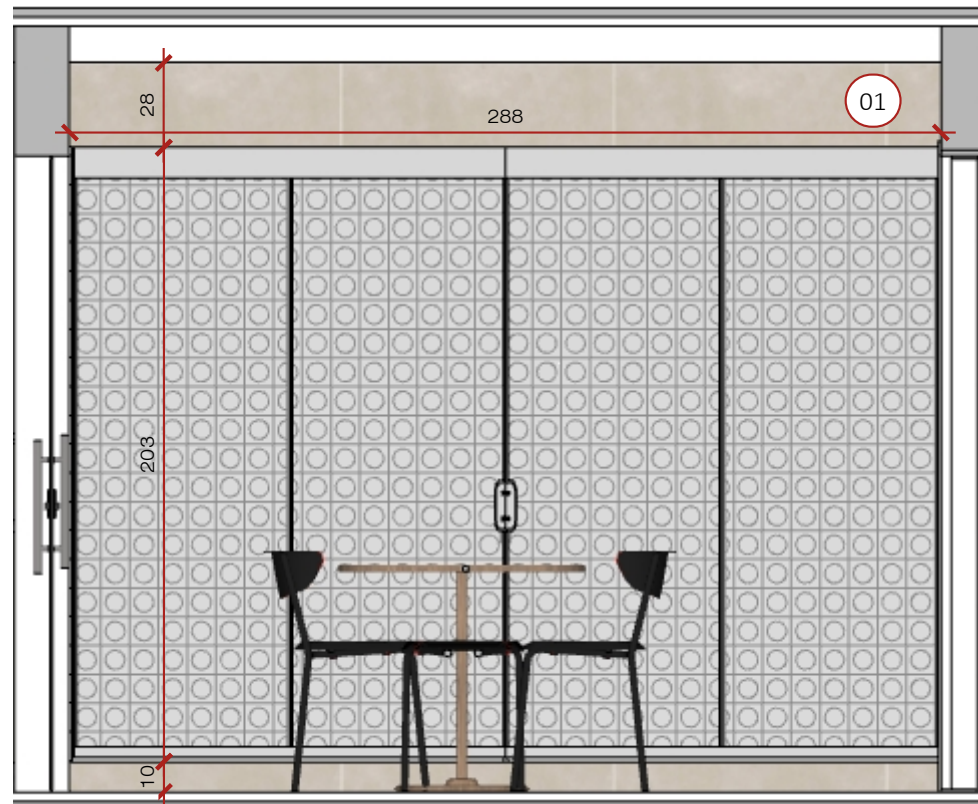


Vista D - Cozinha - Paginação
Esc: 1/25



Imagem 3D - Sem escala

Armário em MDF Nude Vel Berneck.
Puxador: New Facetatto
Profundidade: 40cm

Armário em MDF Nude Vel Berneck.
Puxador: New Facetatto
Profundidade: 48cm

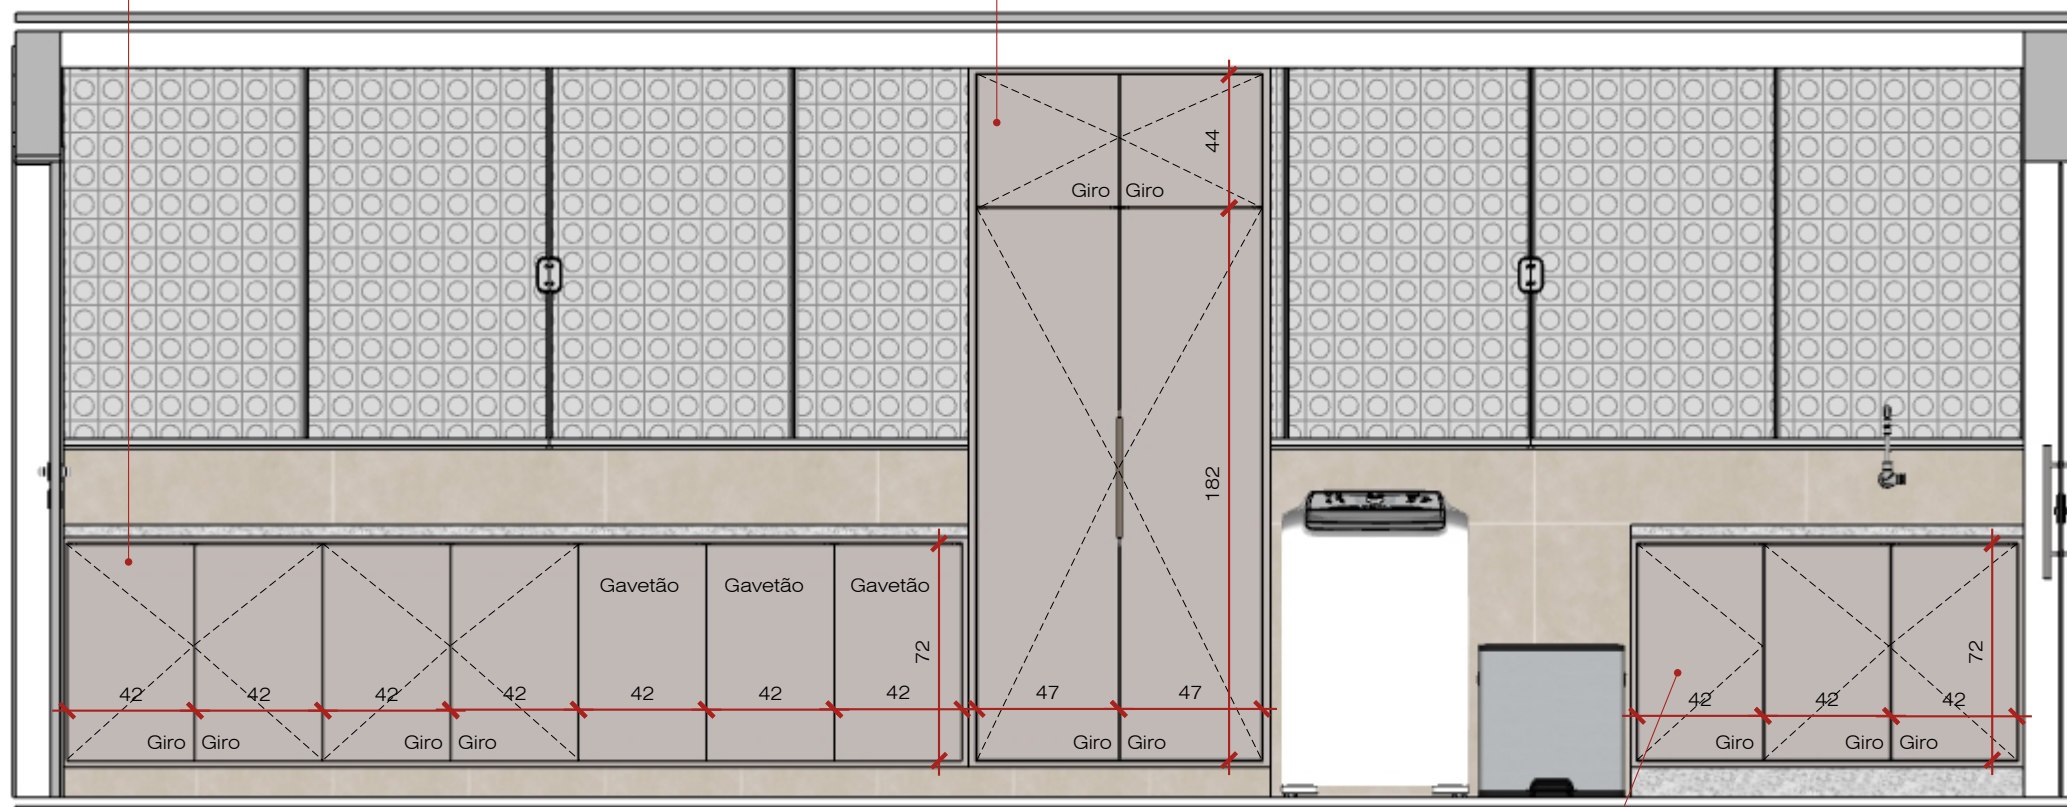

Armário em MDF Nude Vel Berneck.
Puxador: New Facetatto
Profundidade: 50cm

Vista E - Área de Serviço - Marcenaria Externa
Esc: 1/25



Imagem 3D - Sem escala

Cozinha e Área de Serviço

Desenhista: Nathália Rodrigues

As imagens 3D são meramente ilustrativa.
Seguir orientações conforme detalhamento executivo.

Todas as medidas devem ser conferidas no local antes da execução.

Clientes:
Silvana e Hélio

Endereço:
SQS 106 Bloco H, Apartamento 601.
Asa Sul

Data:
27.08.2026

Arquiteto coordenador

Alisson Correia
Celular (61) 98303-0582


Arquiteta responsável

Aline Coutinho Molina
CAU - A108129-2
Celular (61) 99606-5747


Obs: Todas as medidas em centímetros

22


Aline Molina
arquitetura de interiores

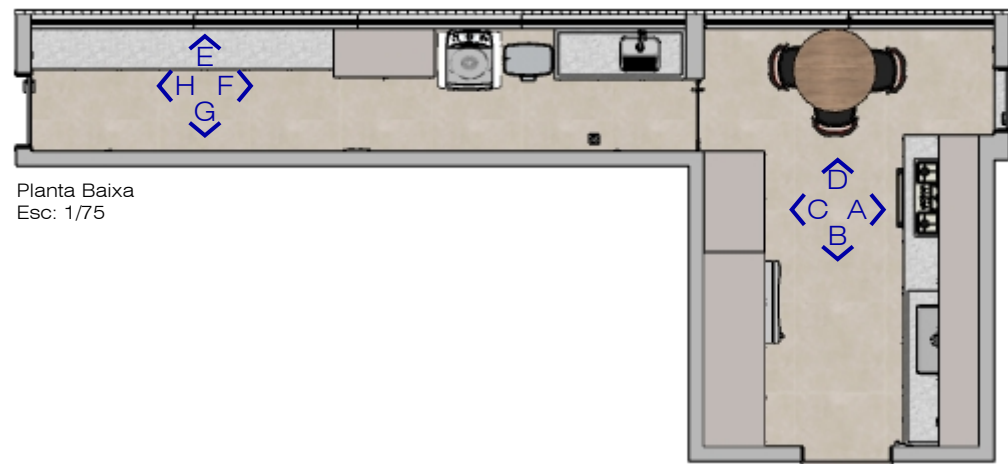

Planta Baixa
Esc: 1/75

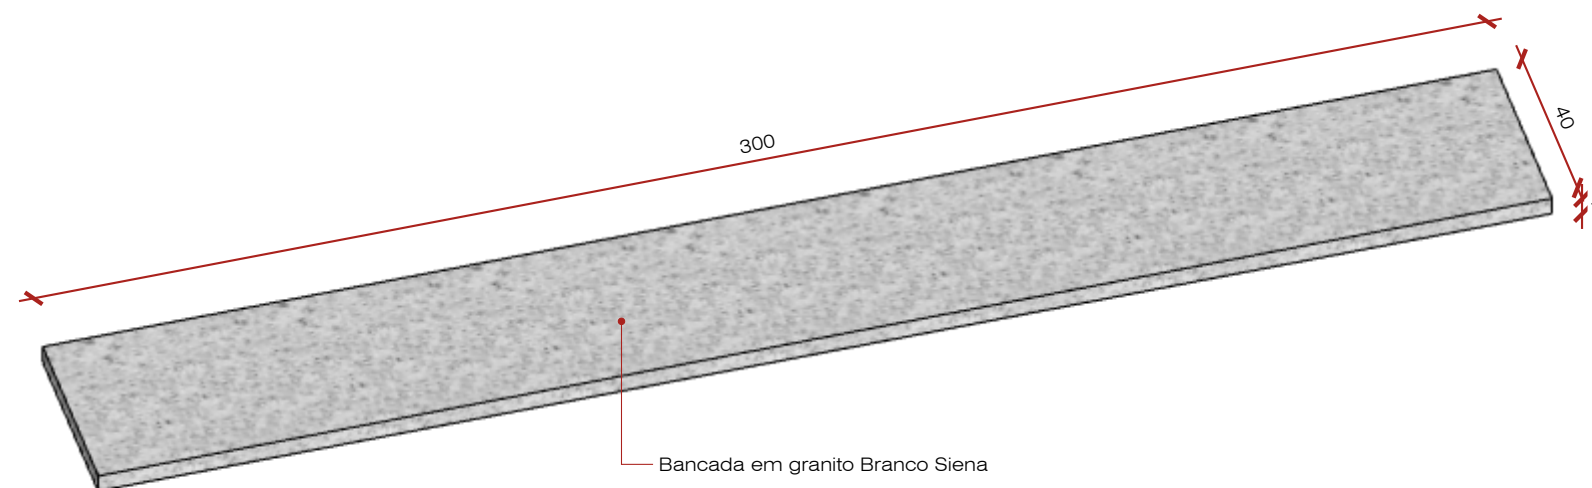


Vista E - Área de Serviço - Marmoraria
Esc: 1/15

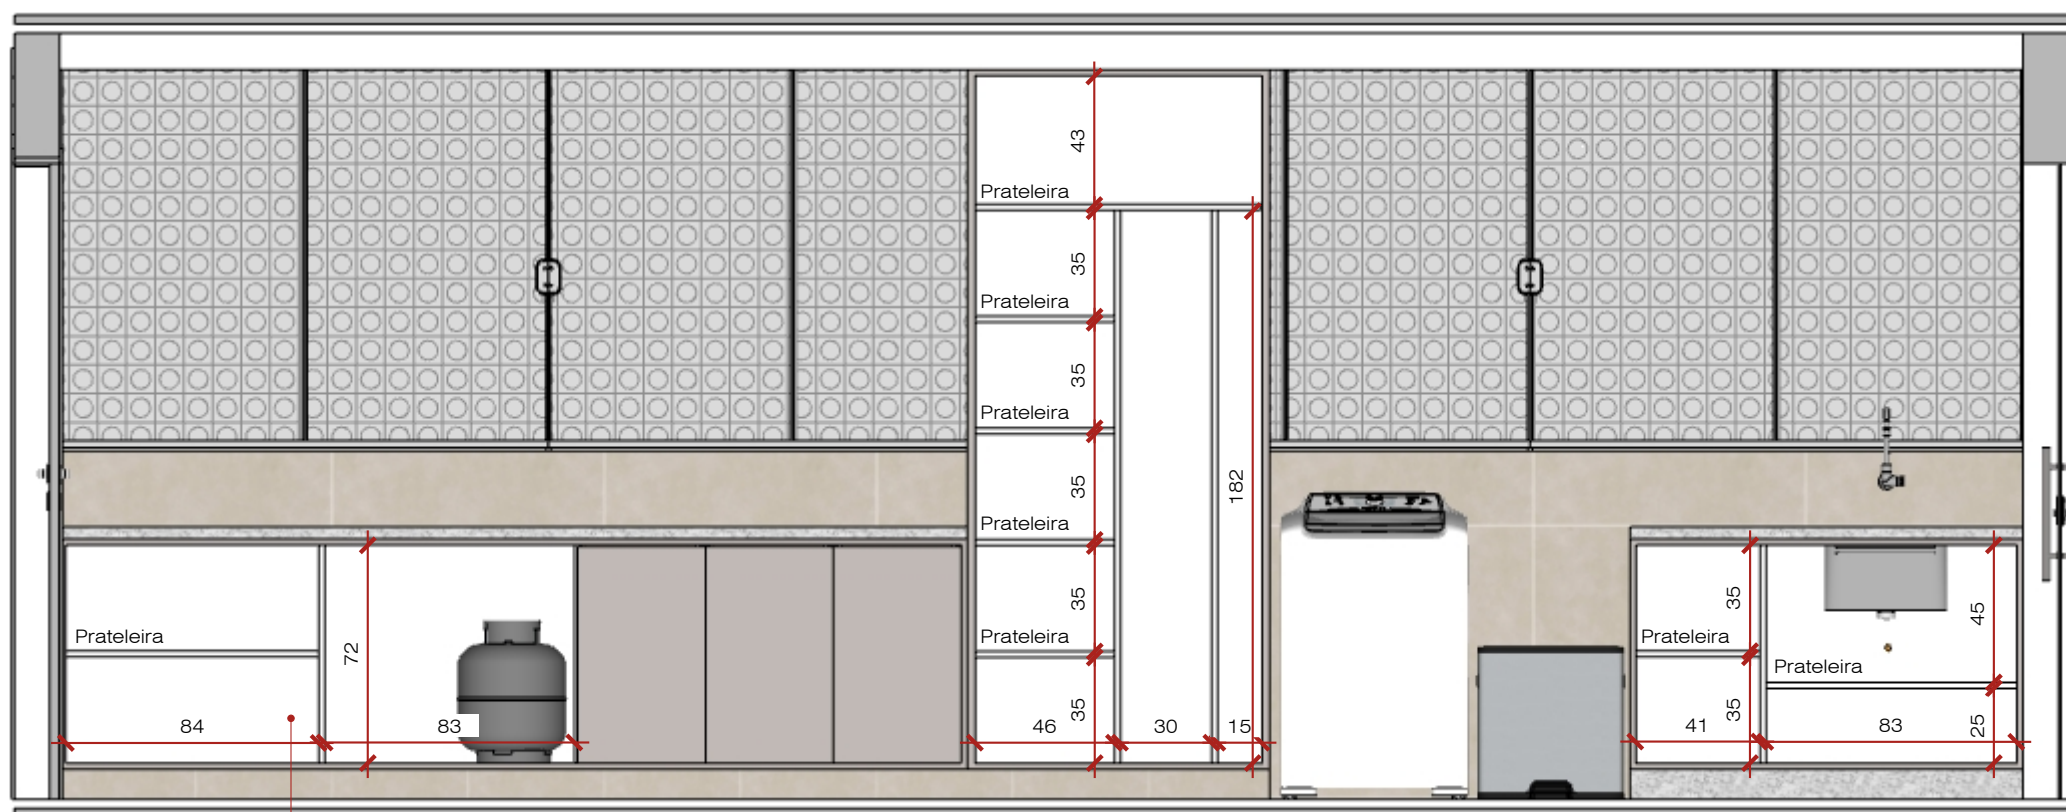


Interno em MDF Branco

Vista E - Área de Serviço - Marcenaria Interna
Esc: 1/25

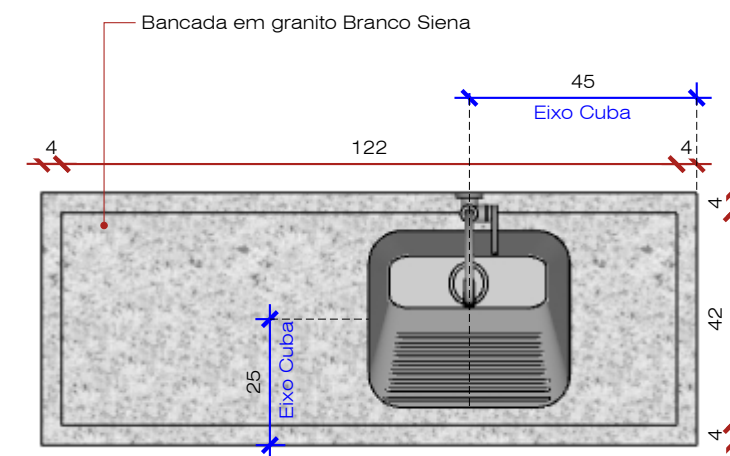

Vista E - Área de Serviço - Marmoraria
Esc: 1/15

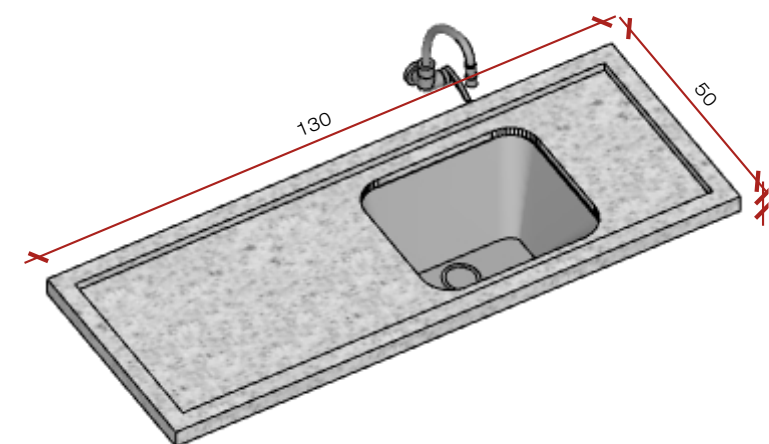

Vista E - Área de Serviço - Marmoraria
Esc: 1/15

Cozinha e Área de Serviço

Desenhista: Nathália Rodrigues

As imagens 3D são meramente ilustrativa.
Seguir orientações conforme detalhamento executivo.

Todas as medidas devem ser conferidas no local antes da execução.

Clientes:
Silvana e Hélio

Endereço:
SQS 106 Bloco H, Apartamento 601.
Asa Sul

Data:
27.08.2026

Arquiteto coordenador

Alisson Correia
Celular (61) 98303-0582


Arquiteta responsável

Aline Coutinho Molina
CAU - A108129-2
Celular (61) 99606-5747


Obs: Todas as medidas em centímetros

23

Aline Molina
arquitetura de interiores

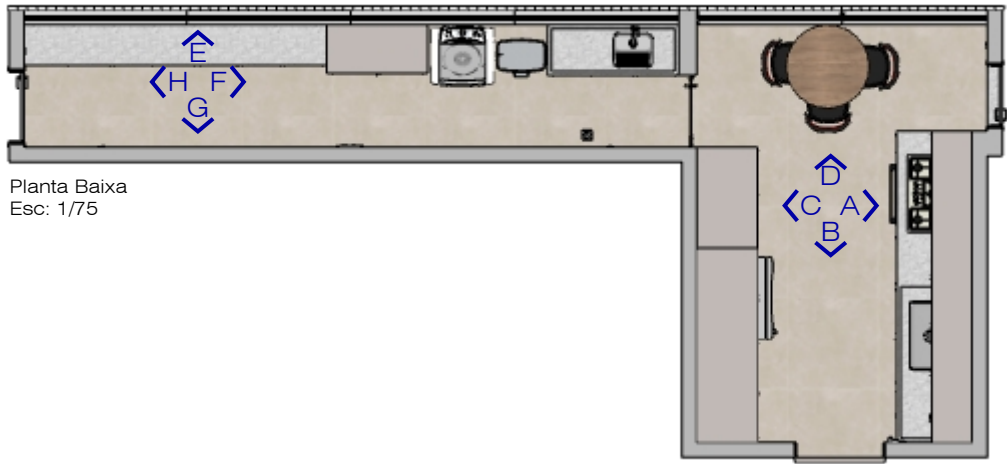


Planta Baixa
Esc: 1/75

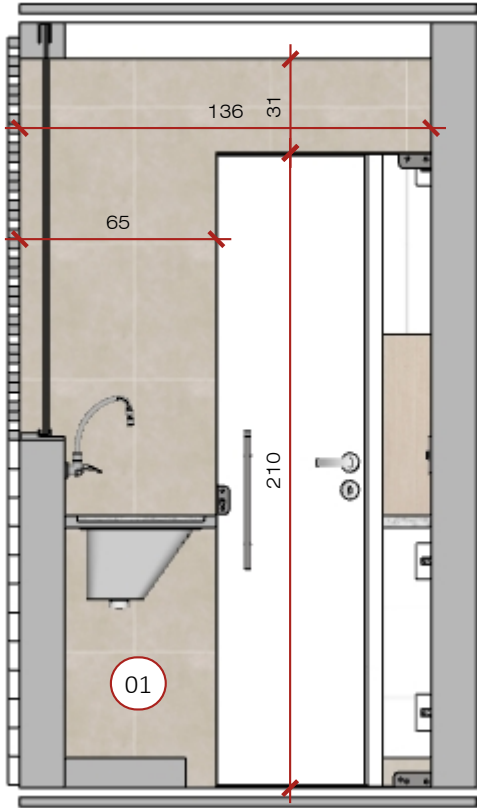

Vista F - Área de Serviço - Paginação
Esc: 1/25

Tabela de LOUÇAS E METAIS:

Item	Material	Ambiente
01	Misturador Monocomando Cozinha Parede Spice - Docol	Cozinha
02	Tanque de encaixe 40x35 Inox - Tramontina	Cozinha

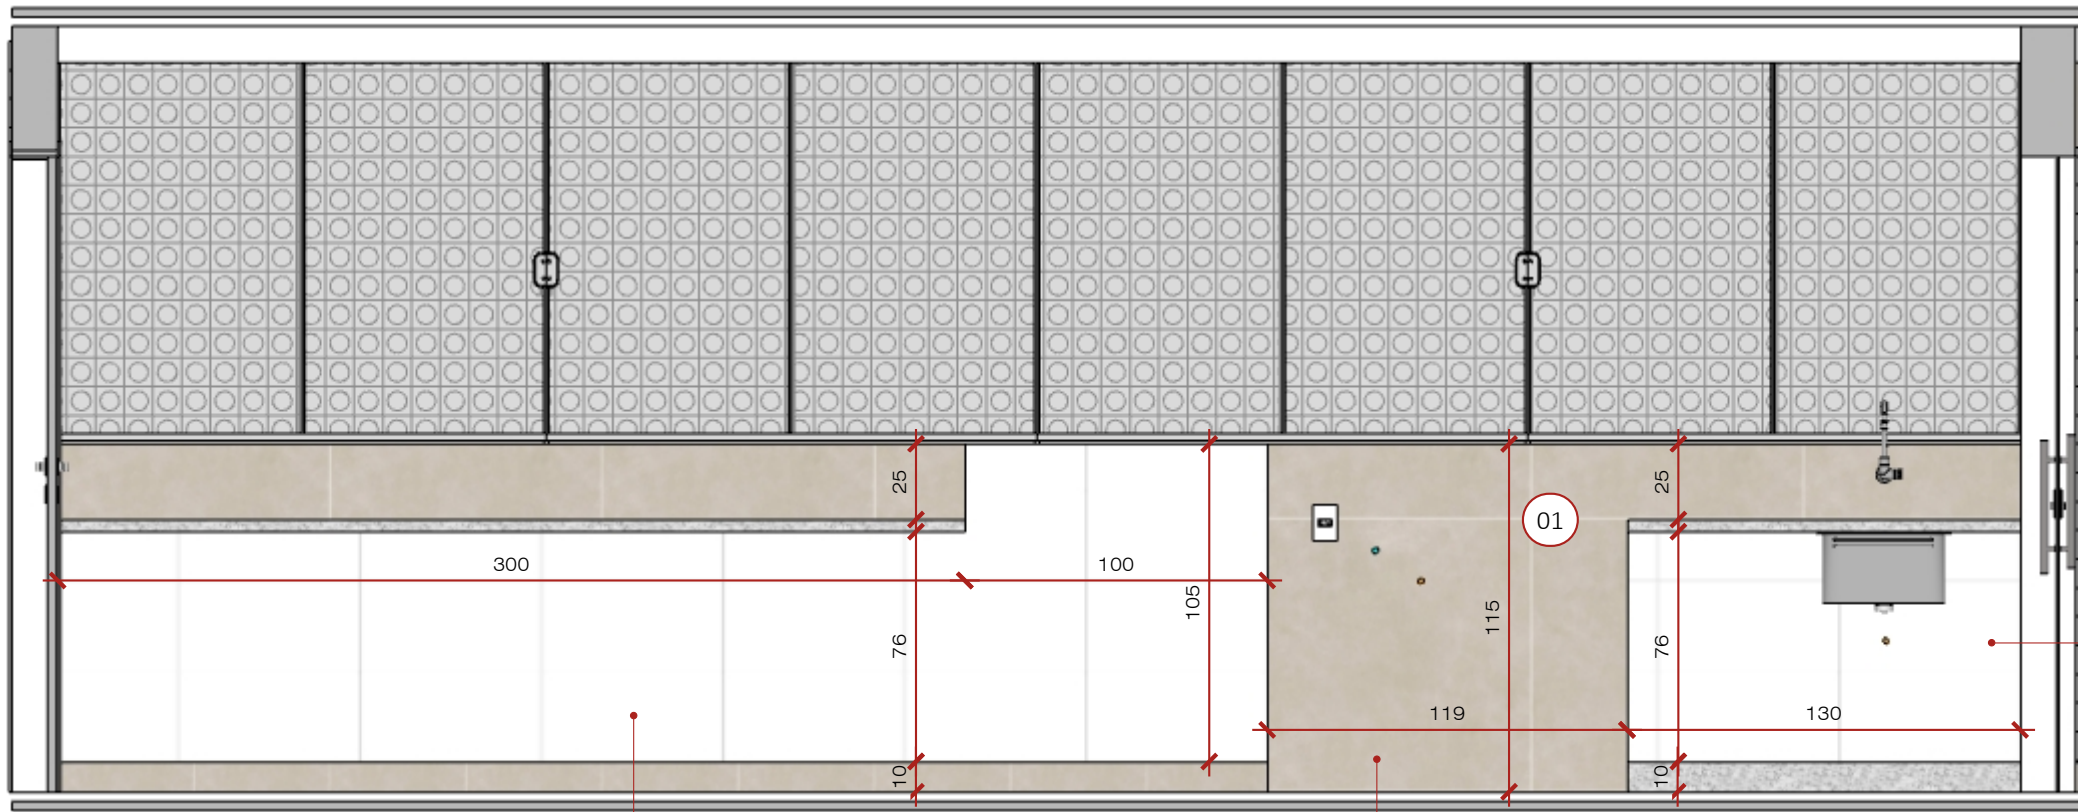

Vista E - Área de Serviço - Paginação
Esc: 1/25

Revestimento existente

Acompanhar linhas de rejunte da paginação do piso

Revestimento existente

Cozinha e Área de Serviço

Desenhista: Nathália Rodrigues

As imagens 3D são meramente ilustrativa.
Seguir orientações conforme detalhamento executivo.

Todas as medidas devem ser conferidas no local antes da execução.

Clientes:
Silvana e Hélio

Endereço:
SQS 106 Bloco H, Apartamento 601.
Asa Sul

Data:
27.08.2026

Arquiteto coordenador

Alisson Correia
Celular (61) 98303-0582


Arquiteta responsável

Aline Coutinho Molina
CAU - A108129-2
Celular (61) 99606-5747


Obs: Todas as medidas em centímetros

24

Aline Molina
arquitetura de interiores

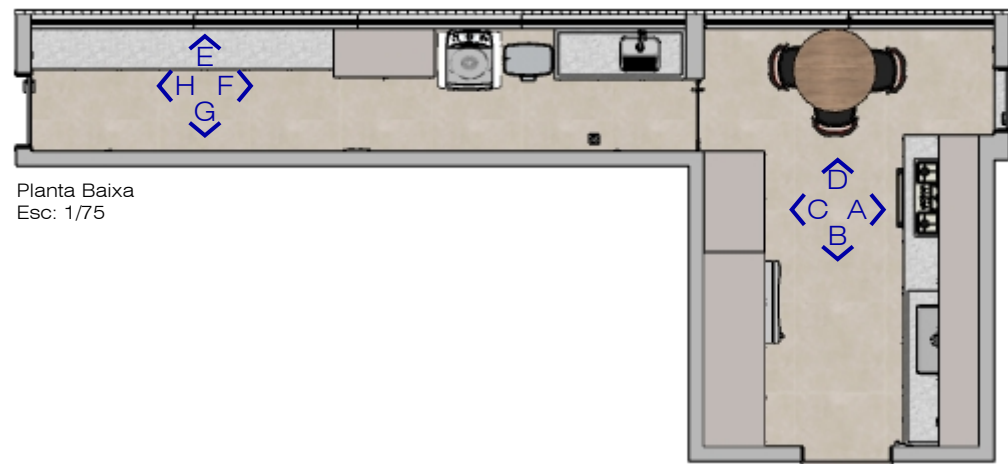

Planta Baixa
Esc: 1/75

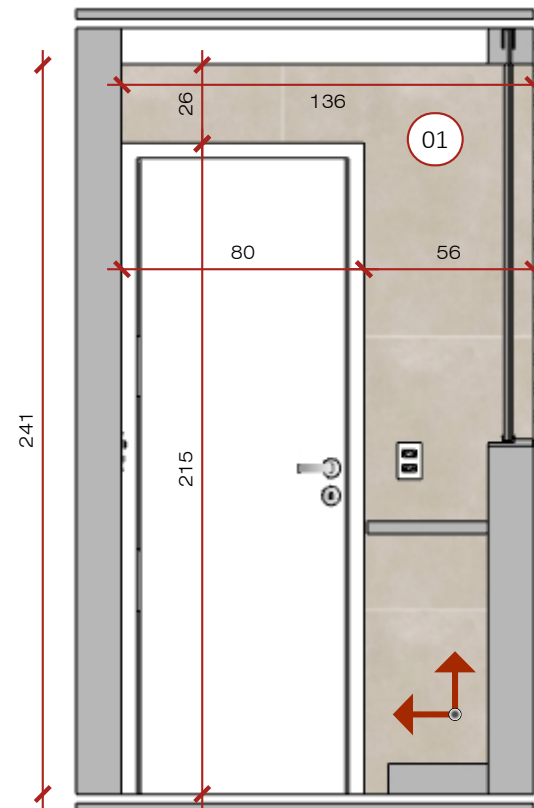

Vista H - Área de Serviço - Paginação
Esc: 1/25


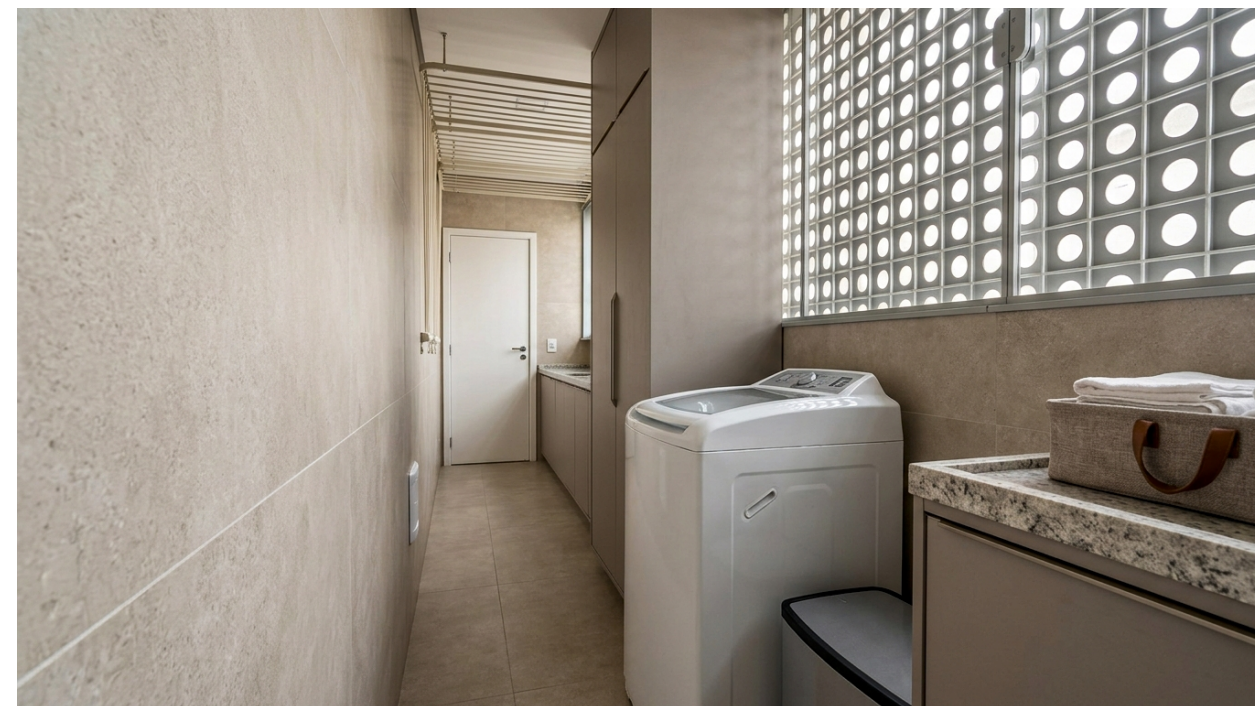


Imagem 3D - Sem escala

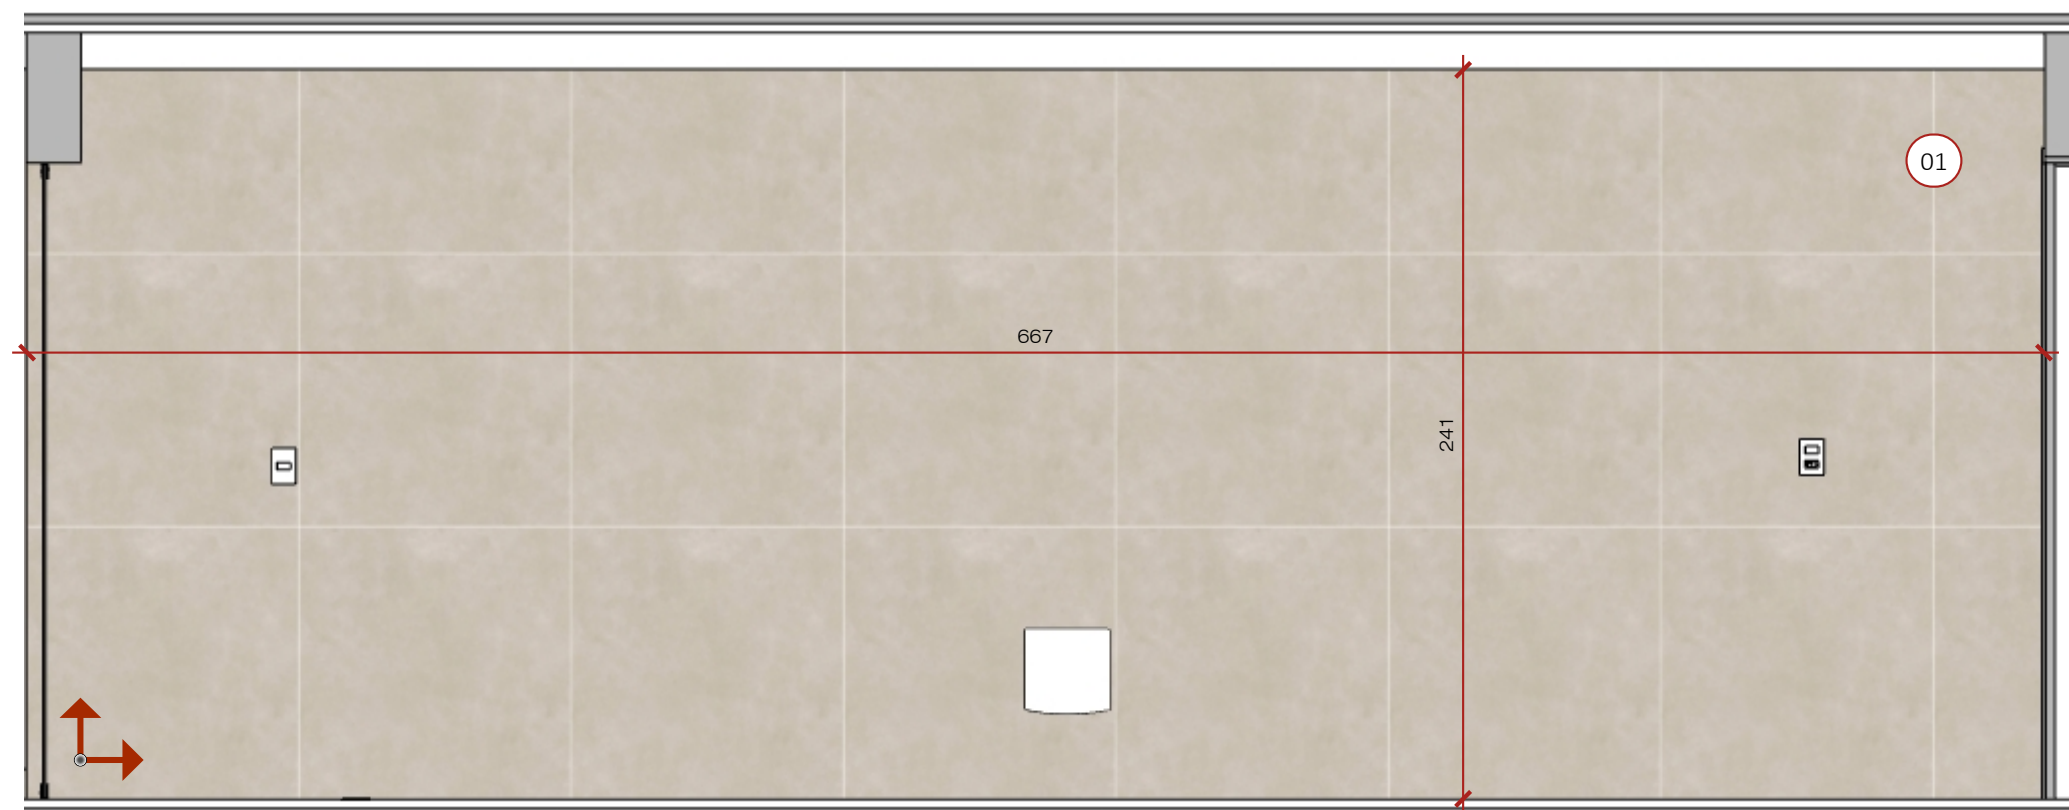

Vista E - Área de Serviço - Paginação
Esc: 1/25

Cozinha e Área de Serviço

Desenhista: Nathália Rodrigues

As imagens 3D são meramente ilustrativa.
Seguir orientações conforme detalhamento executivo.

Todas as medidas devem ser conferidas no local antes da execução.

Clientes:
Silvana e Hélio

Endereço:
SQS 106 Bloco H, Apartamento 601.
Asa Sul

Data:
27.08.2026

Arquiteto coordenador

Alisson Correia
Celular (61) 98303-0582

Arquiteta responsável

Aline Coutinho Molina
CAU - A108129-2
Celular (61) 99606-5747

Obs: Todas as medidas em centímetros

25

Aline Molina
arquitetura de interiores