


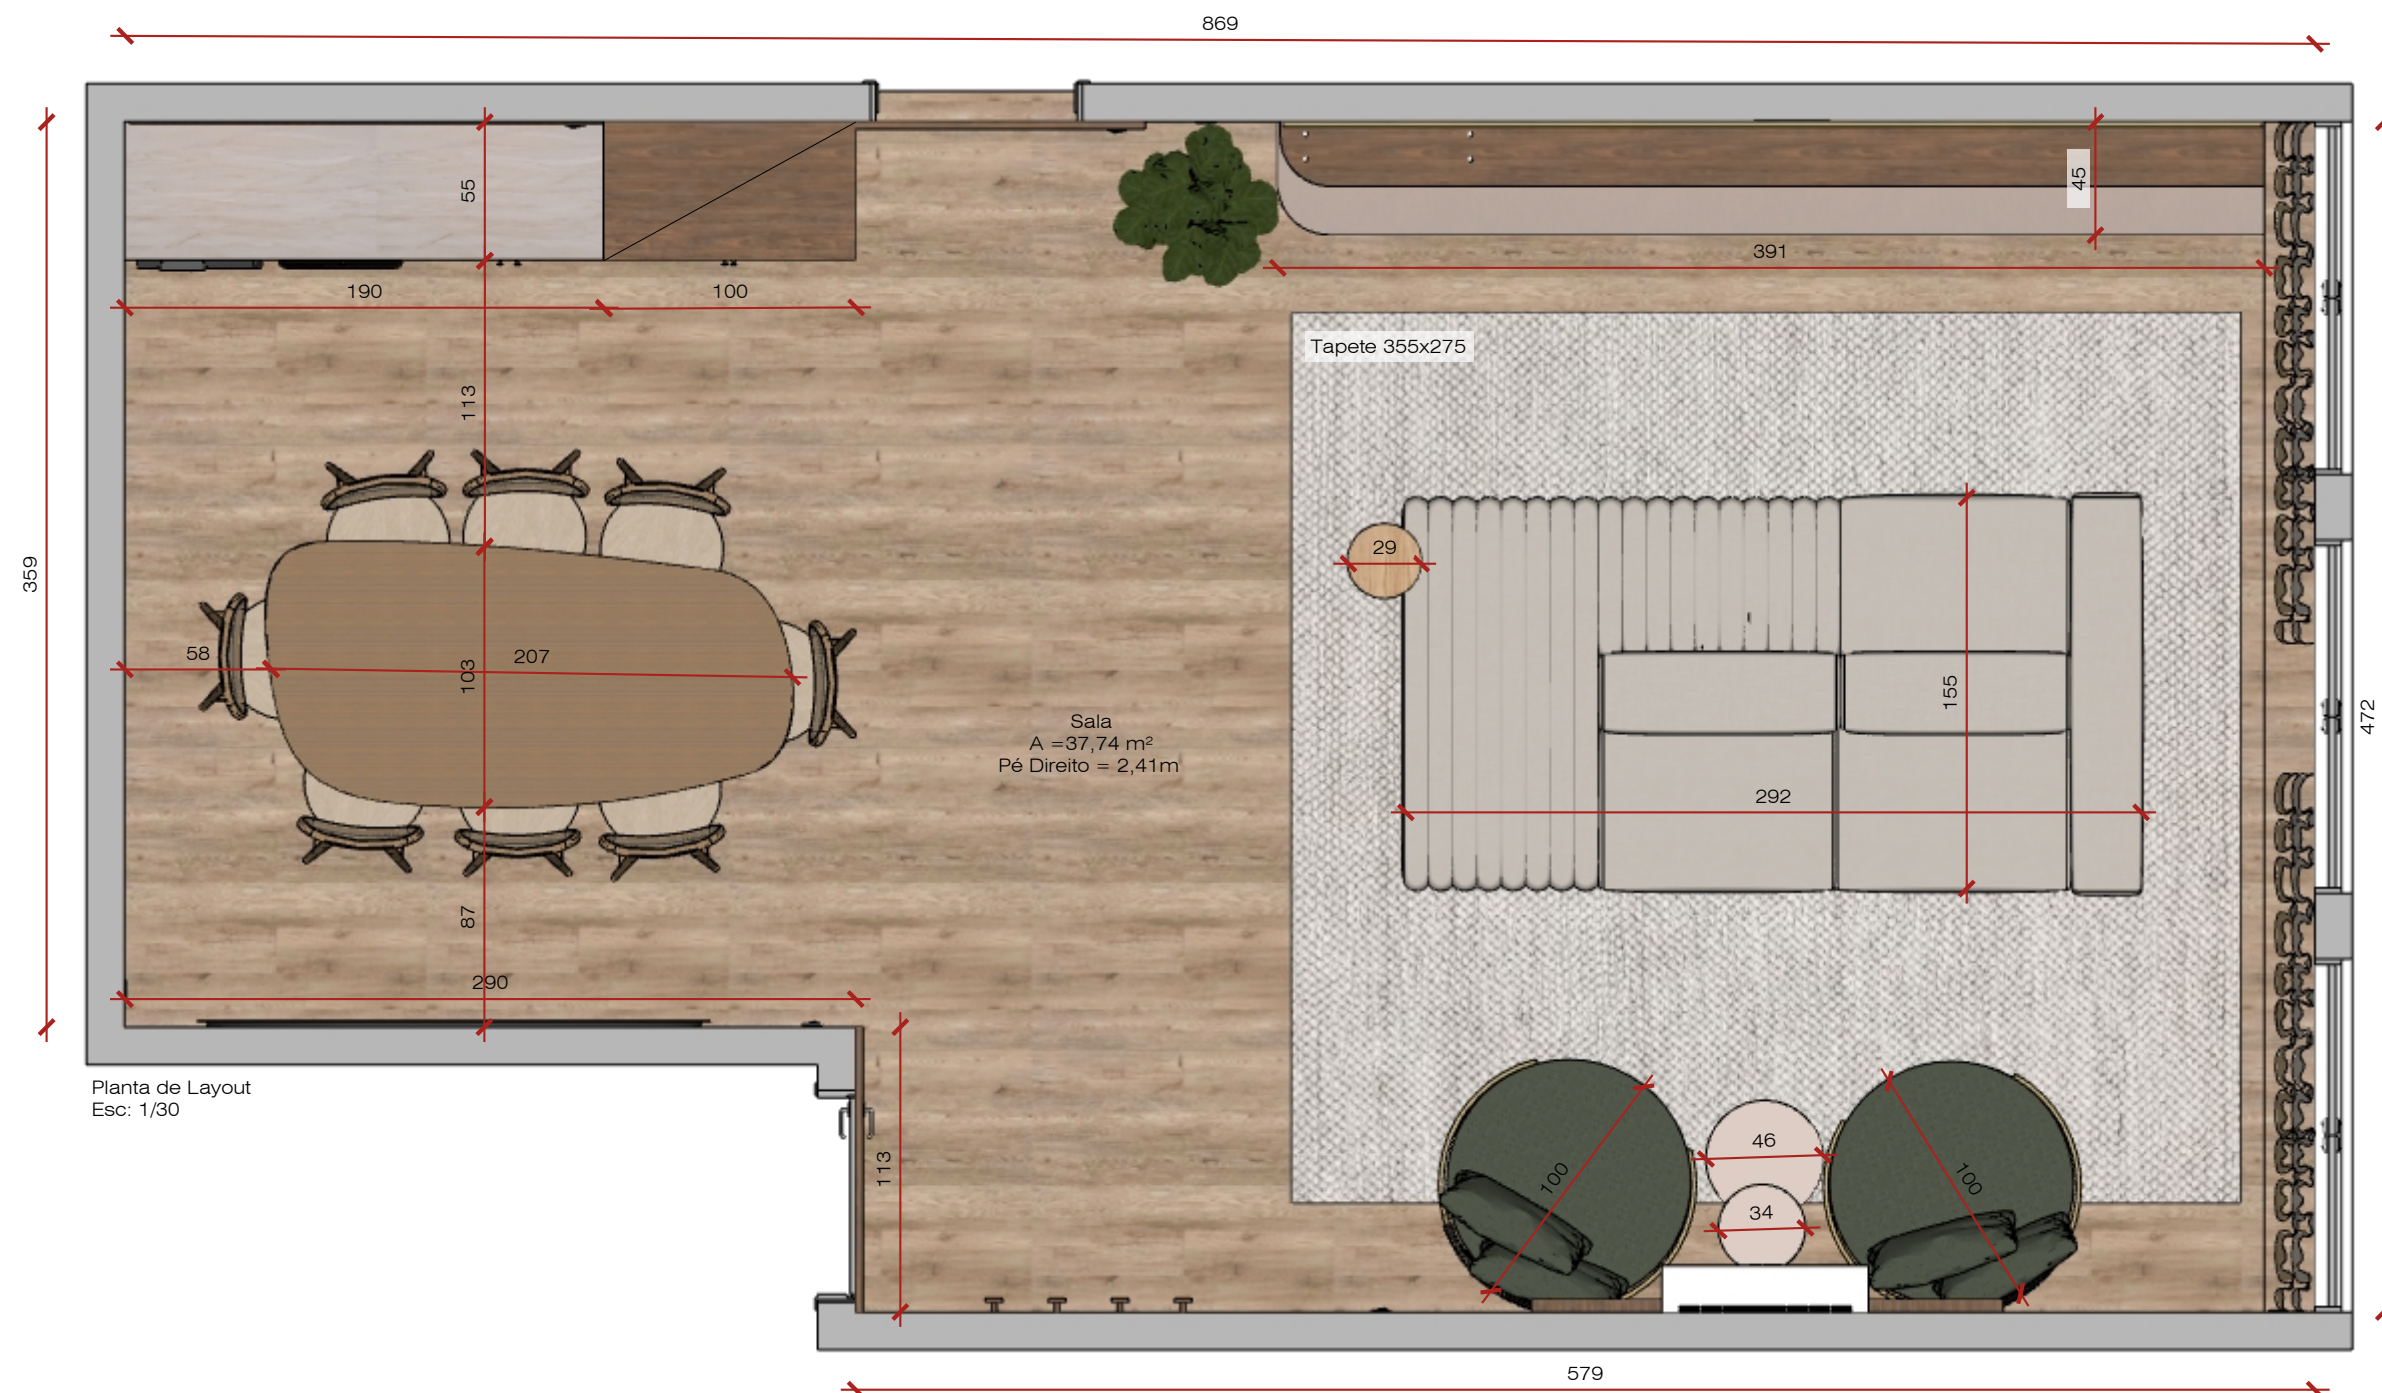

Sala

Desenhista: Nathália Rodrigues

As imagens 3D são meramente ilustrativa.
Seguir orientações conforme detalhamento executivo.

Todas as medidas devem ser conferidas no local antes da execução.

Clientes:
Silvana e Hélio

Endereço:
SQS 106 Bloco H, Apartamento 601.
Asa Sul.

Data:
26.08.2026

Arquiteto coordenador

Alisson Correia
Celular (61) 98303-0582

Arquiteta responsável

Aline Coutinho Molina
CAU - A108129-2
Celular (61) 99606-5747

Obs: Todas as medidas em centímetros


01

Aline Molina
arquitetura de interiores

- OBSERVAÇÕES GERAIS:
- 1) As cotas são referentes as medidas dos eixos dos pontos;
 - 2) Os números ao lado dos pontos são referentes as alturas dos mesmos;
 - 3) Toda vez que indicado para retirar algum ponto e ele for passagem (impossibilitando a retirada) inserir tampa cega;
 - 4) Nos locais onde possuem pontos de ar-condicionado criar duto para saída de água em um ralo mais próximo;
 - 5) Na origem do cabo colocar acabamento de quadro elétrico 30 x 30cm;
 - 6) Interligar com cano PVC Ø50mm para passagem do cabo HDMI;
 - 7) Interligar cabos de TV com mangueira pelo gesso ou pela parede para passagem do fio pela empresa contratada;
 - 8) Conferir no manual se o eletro precisa de disjuntor próprio / tomada de 20A;
 - 9) Esconder DRIVERS de acordo com a indicação da planta de iluminação.

LEGENDA:	
Simbologia	Descrição
	Tomada elétrica simples
	Tomada elétrica dupla
	Tomada elétrica tripla
	TV a Cabo
	Interruptor
	Rede
	Ar - Condicionado

LEGENDA:	
	Pontos existentes - MANTER
	Pontos existentes - EXCLUIR
	Pontos novos
	Pontos existentes - MODIFICAR ALTURA

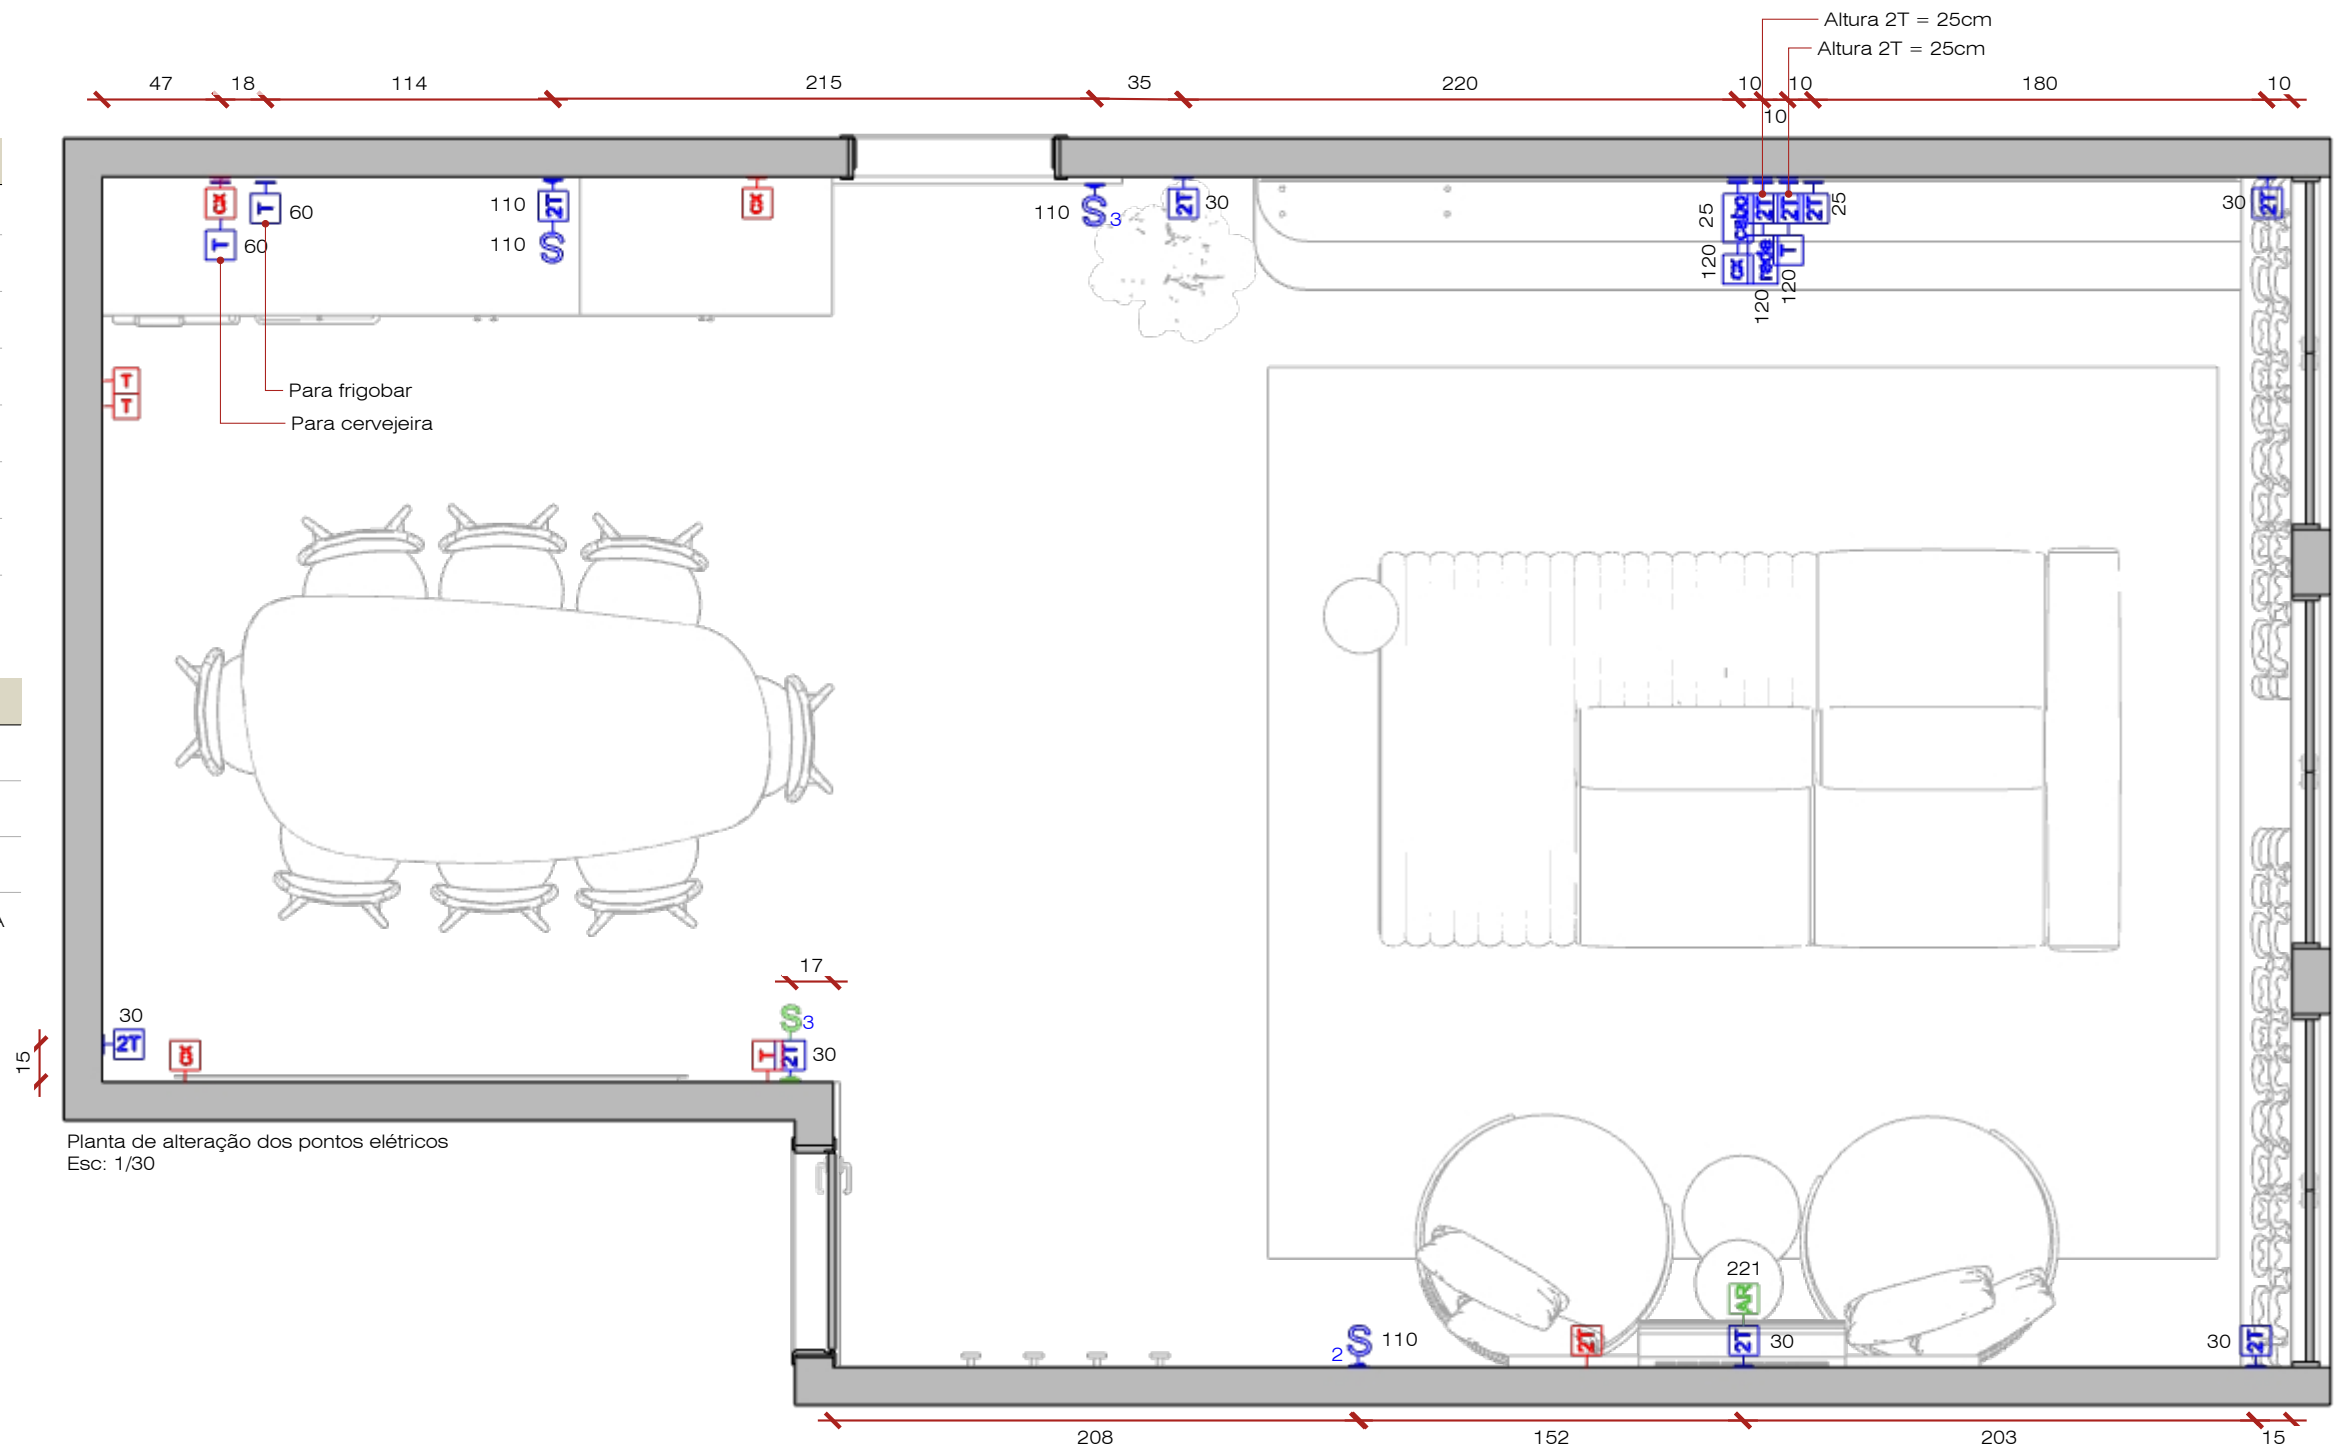

Sala

Desenhista: Nathália Rodrigues

As imagens 3D são meramente ilustrativa.
Seguir orientações conforme detalhamento executivo.

Todas as medidas devem ser conferidas no local antes da execução.

Clientes:
Silvana e Hélio

Endereço:
SQS 106 Bloco H, Apartamento 601.
Asa Sul.

Data:
26.08.2026

Arquiteto coordenador

Alisson Correia
Celular (61) 98303-0582


Arquiteta responsável

Aline Coutinho Molina
CAU - A108129-2
Celular (61) 99606-5747

Obs: Todas as medidas em centímetros

02

Aline Molina
arquitetura de interiores

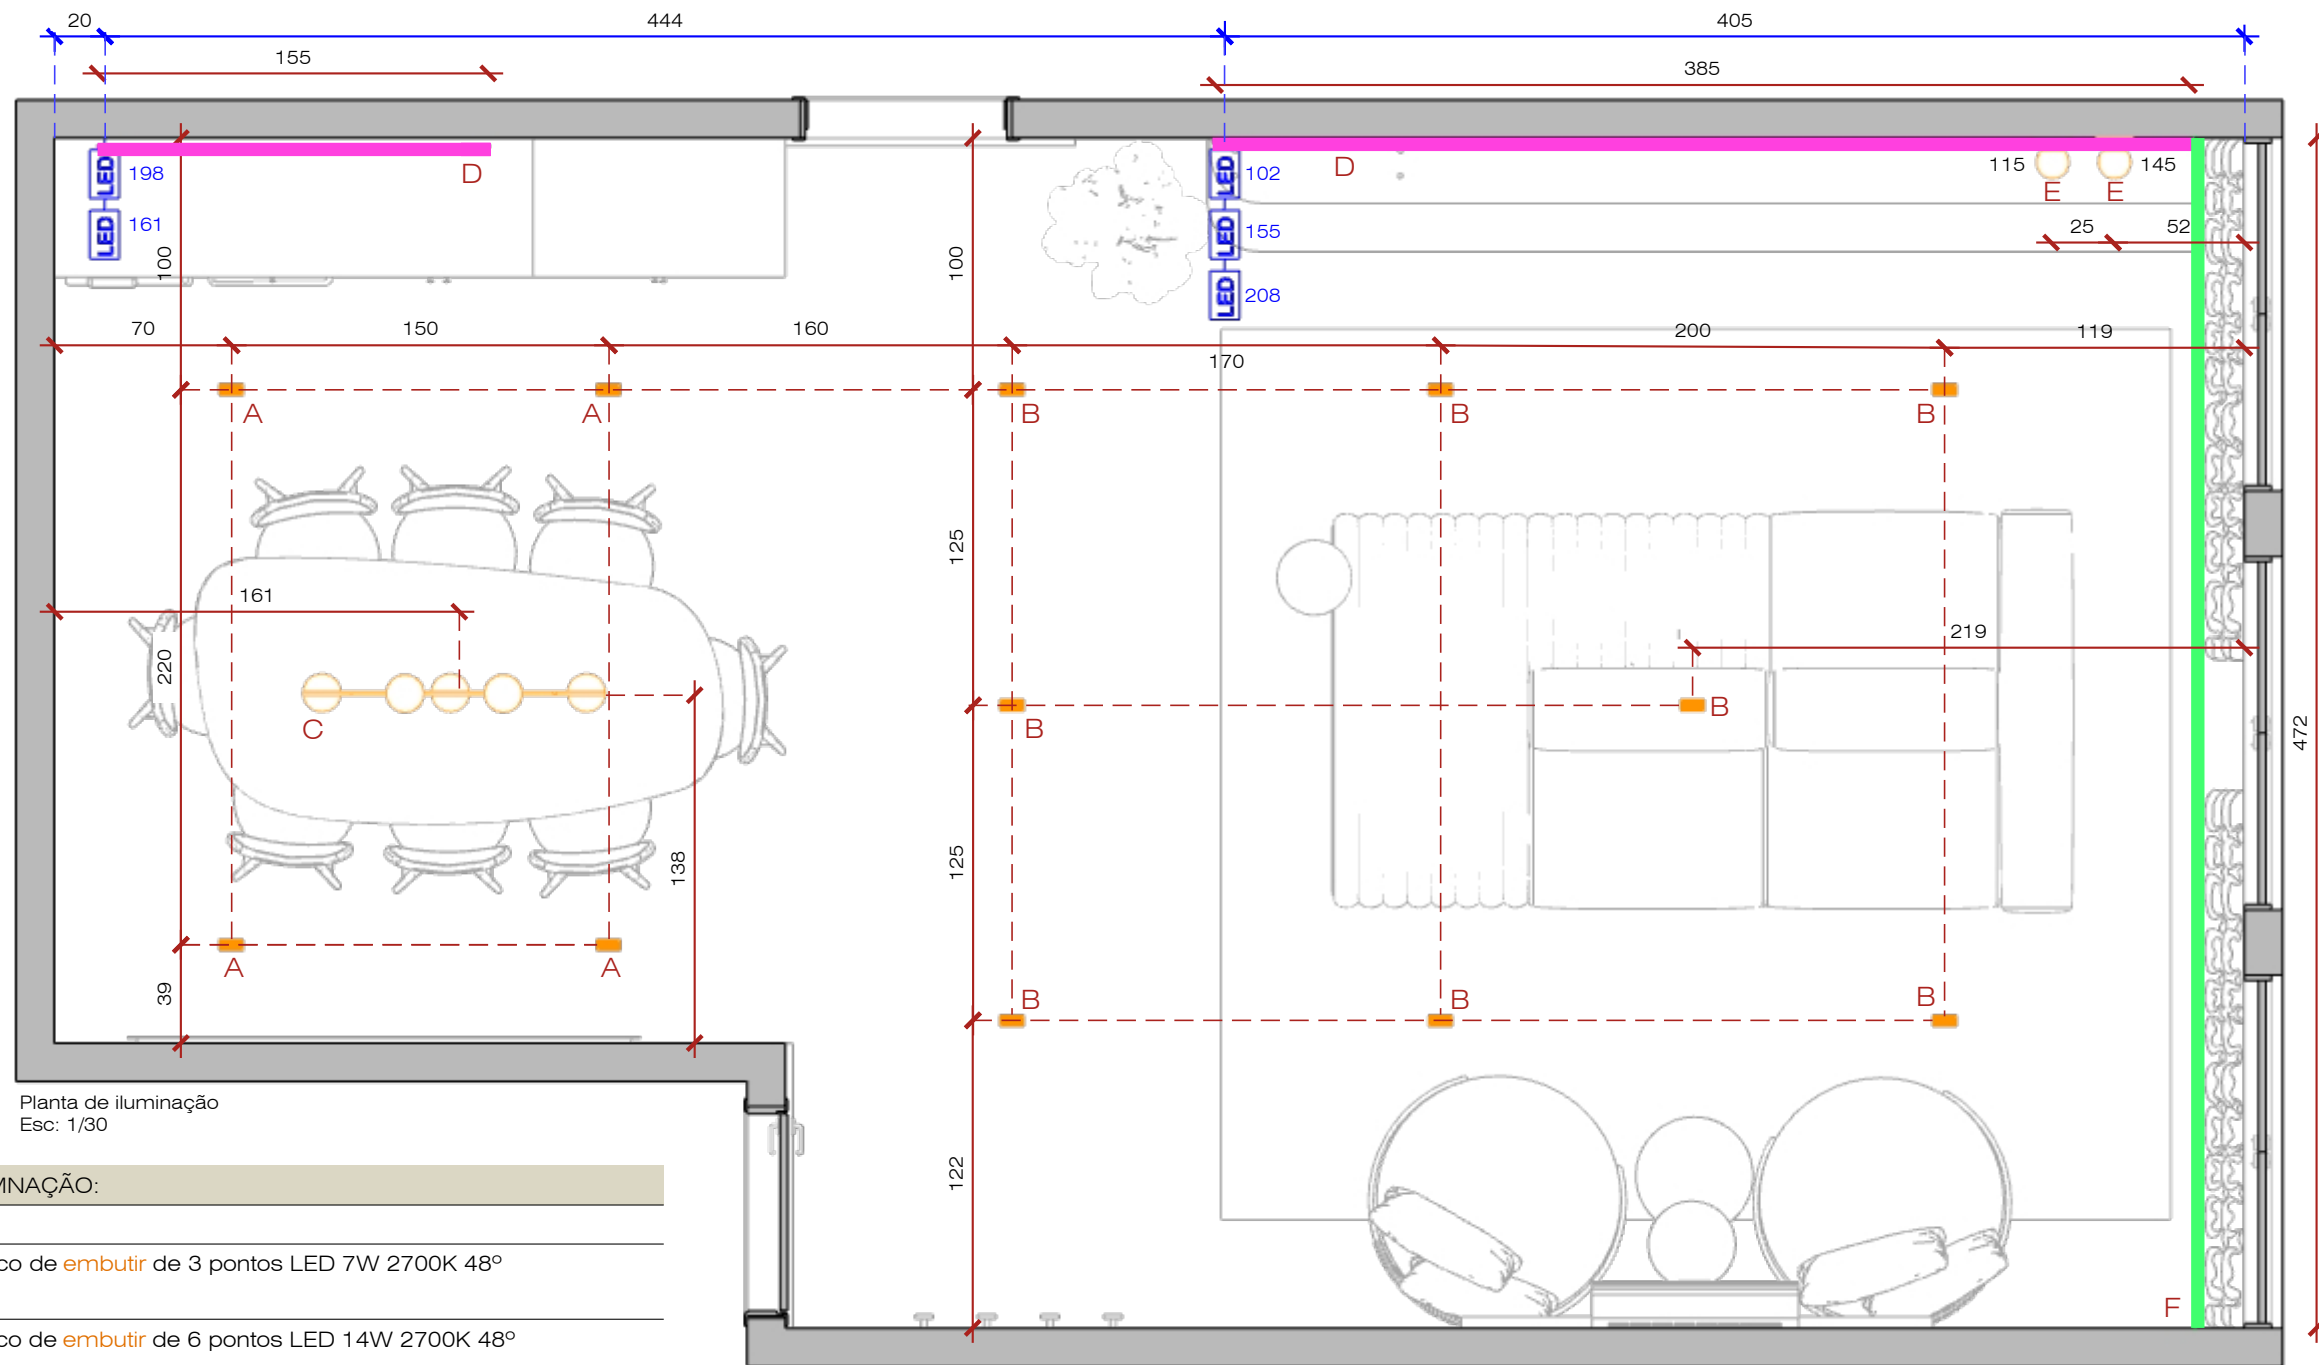

Planta de iluminação
Esc: 1/30

LEGENDA ILUMNAÇÃO:

Descrição

A - Interlight Picco de **embutir** de 3 pontos LED 7W 2700K 48°
4 unidades

B - Interlight Picco de **embutir** de 6 pontos LED 14W 2700K 48°
8 unidades

C - Pendente Kalida DNA Lustres
1 unidade

D - Perfil Baby de **sobrepôr** na cor branca com Fita de LED 8W 3000K

*Para instalar nas prateleiras ao lado da cristaleira
Quantidade: 110cm + 155cm

*Para instalar nas prateleiras da TV
Quantidade: 385cm + 80cm + 80cm

E - Arandela Kalida DNA Lustres 20 cm

2 unidades

F - Perfil de **sobrepôr** na cor branca com fita de LED 14W 3000K

*Para instalar no cortineiro
Quantidade: 472cm

Sala

Desenhista: Nathália Rodrigues

As imagens 3D são meramente ilustrativa.
Seguir orientações conforme detalhamento executivo.

Todas as medidas devem ser conferidas no local antes da execução.

Clientes:
Silvana e Hélio

Endereço:
SQS 106 Bloco H, Apartamento 601.
Asa Sul.

Data:
26.08.2026

Arquiteto coordenador

Alisson Correia
Celular (61) 98303-0582


Arquiteta responsável

Aline Coutinho Molina
CAU - A108129-2
Celular (61) 99606-5747

Obs: Todas as medidas em centímetros

03

Aline Molina
arquitetura de interiores

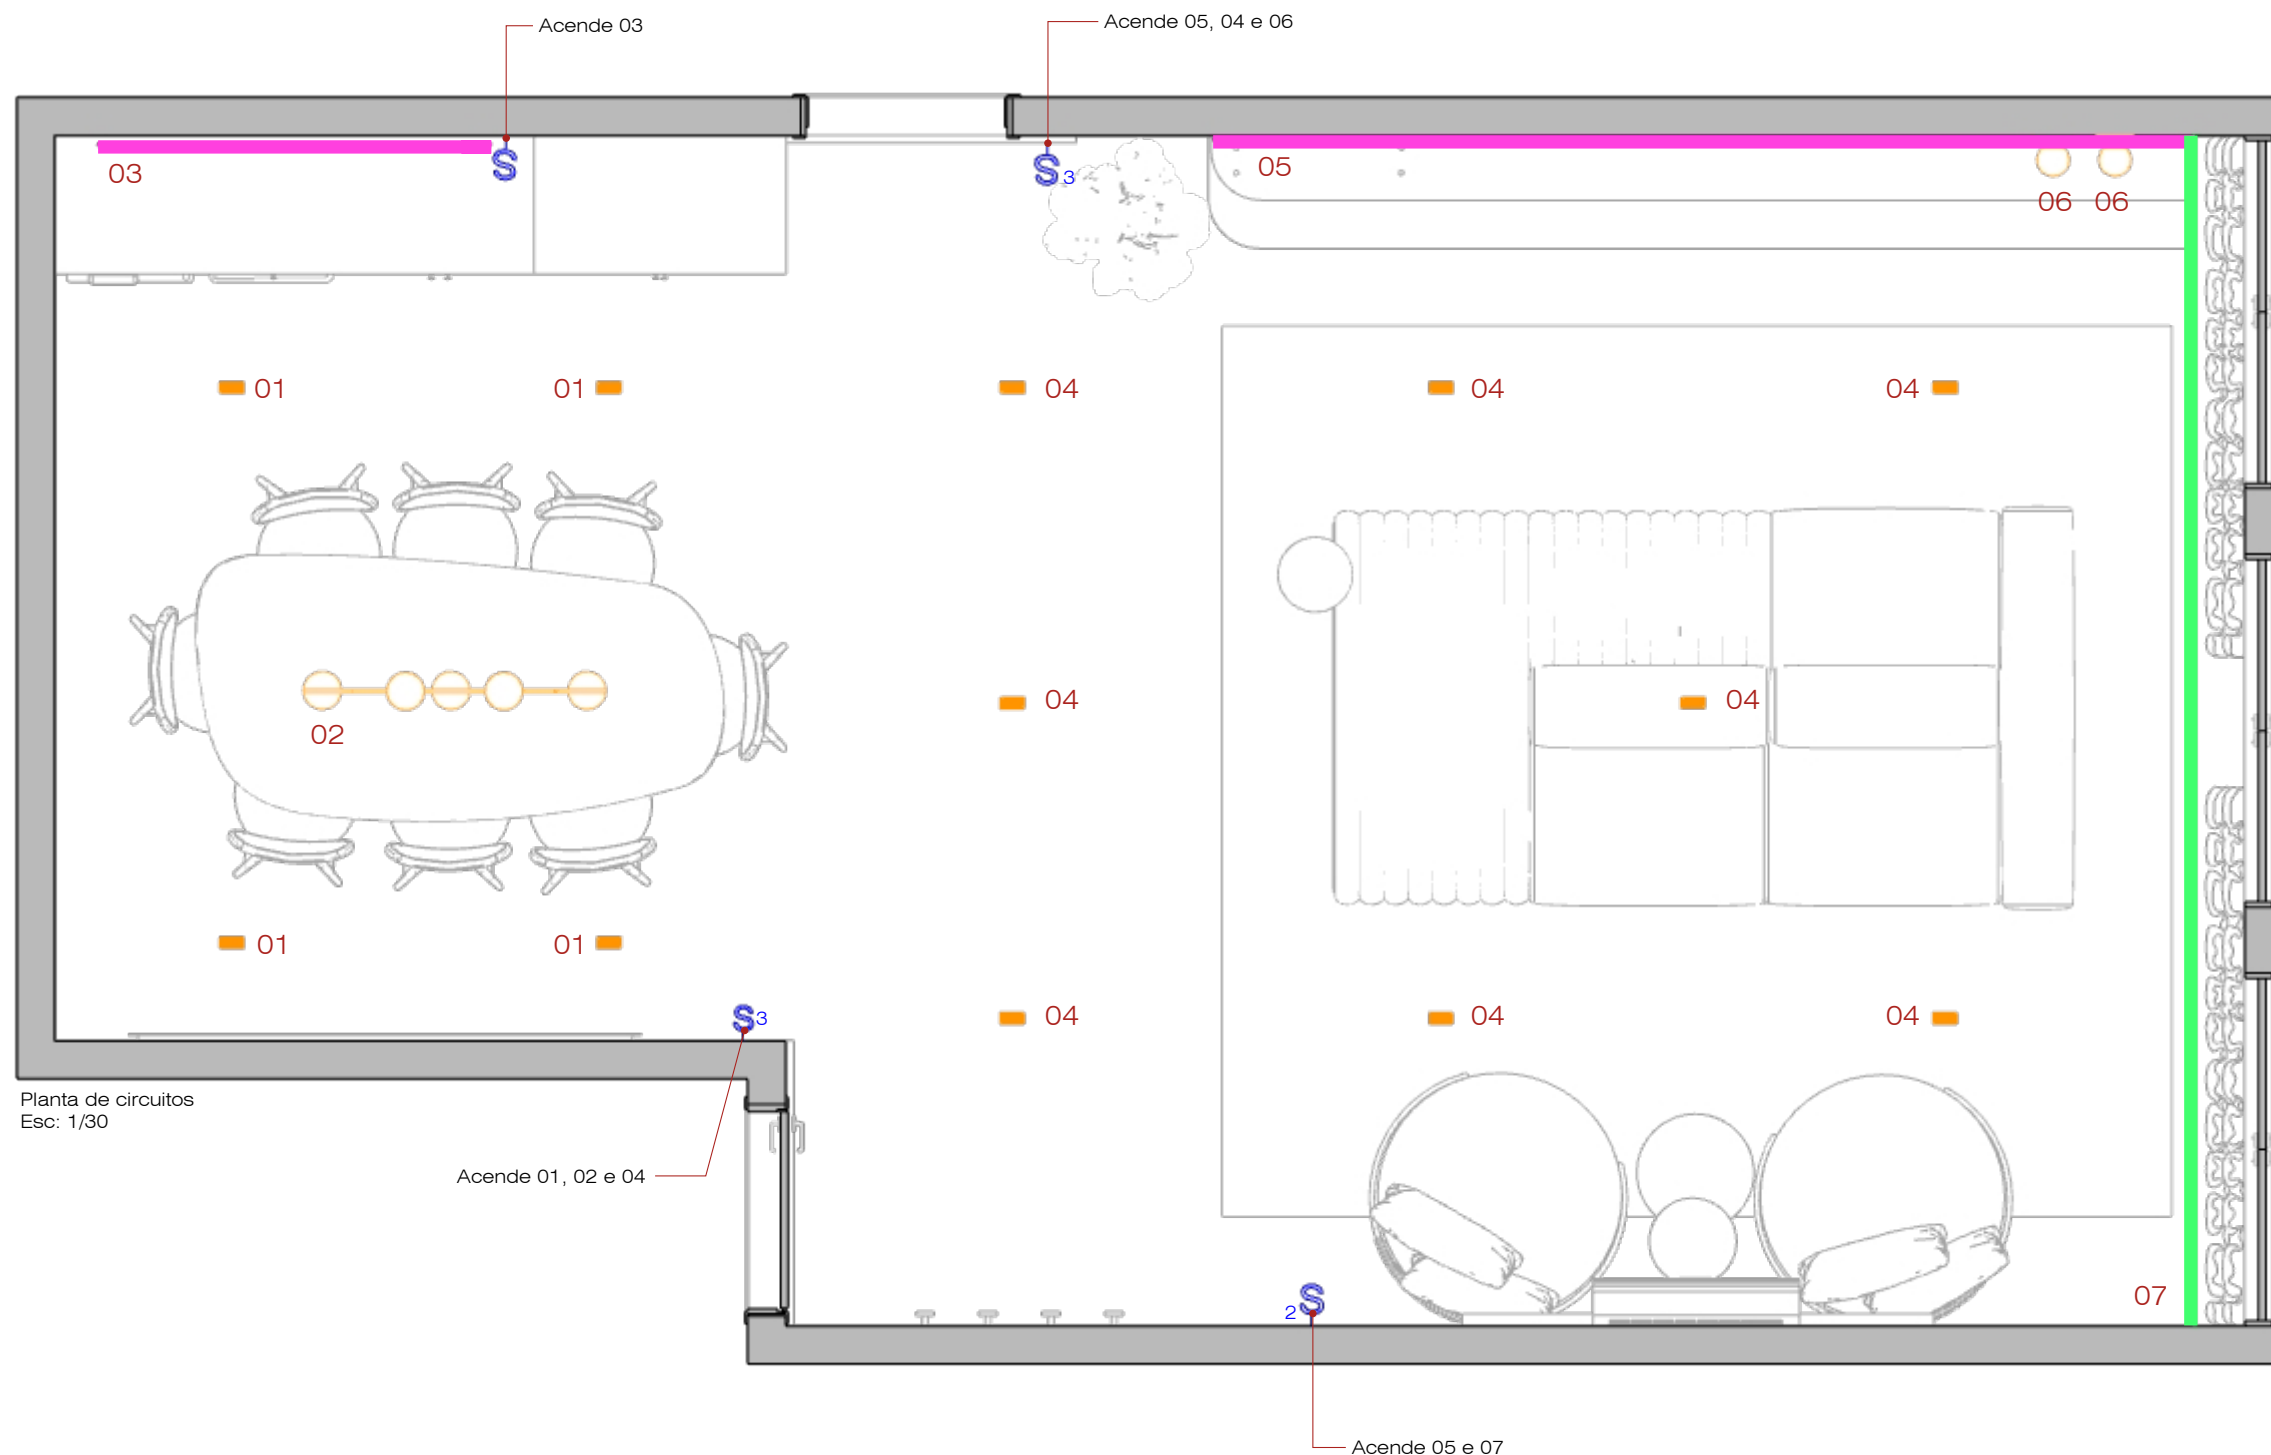

Sala

Desenhista: Nathália Rodrigues

As imagens 3D são meramente ilustrativa.
Seguir orientações conforme detalhamento executivo.

Todas as medidas devem ser conferidas no local antes da execução.

Clientes:
Silvana e Hélio

Endereço:
SQS 106 Bloco H, Apartamento 601.
Asa Sul.

Data:
26.08.2026

Arquiteto coordenador

Alisson Correia
Celular (61) 98303-0582


Arquiteta responsável

Aline Coutinho Molina
CAU - A108129-2
Celular (61) 99606-5747

Obs: Todas as medidas em centímetros

04

Aline Molina
arquitetura de interiores

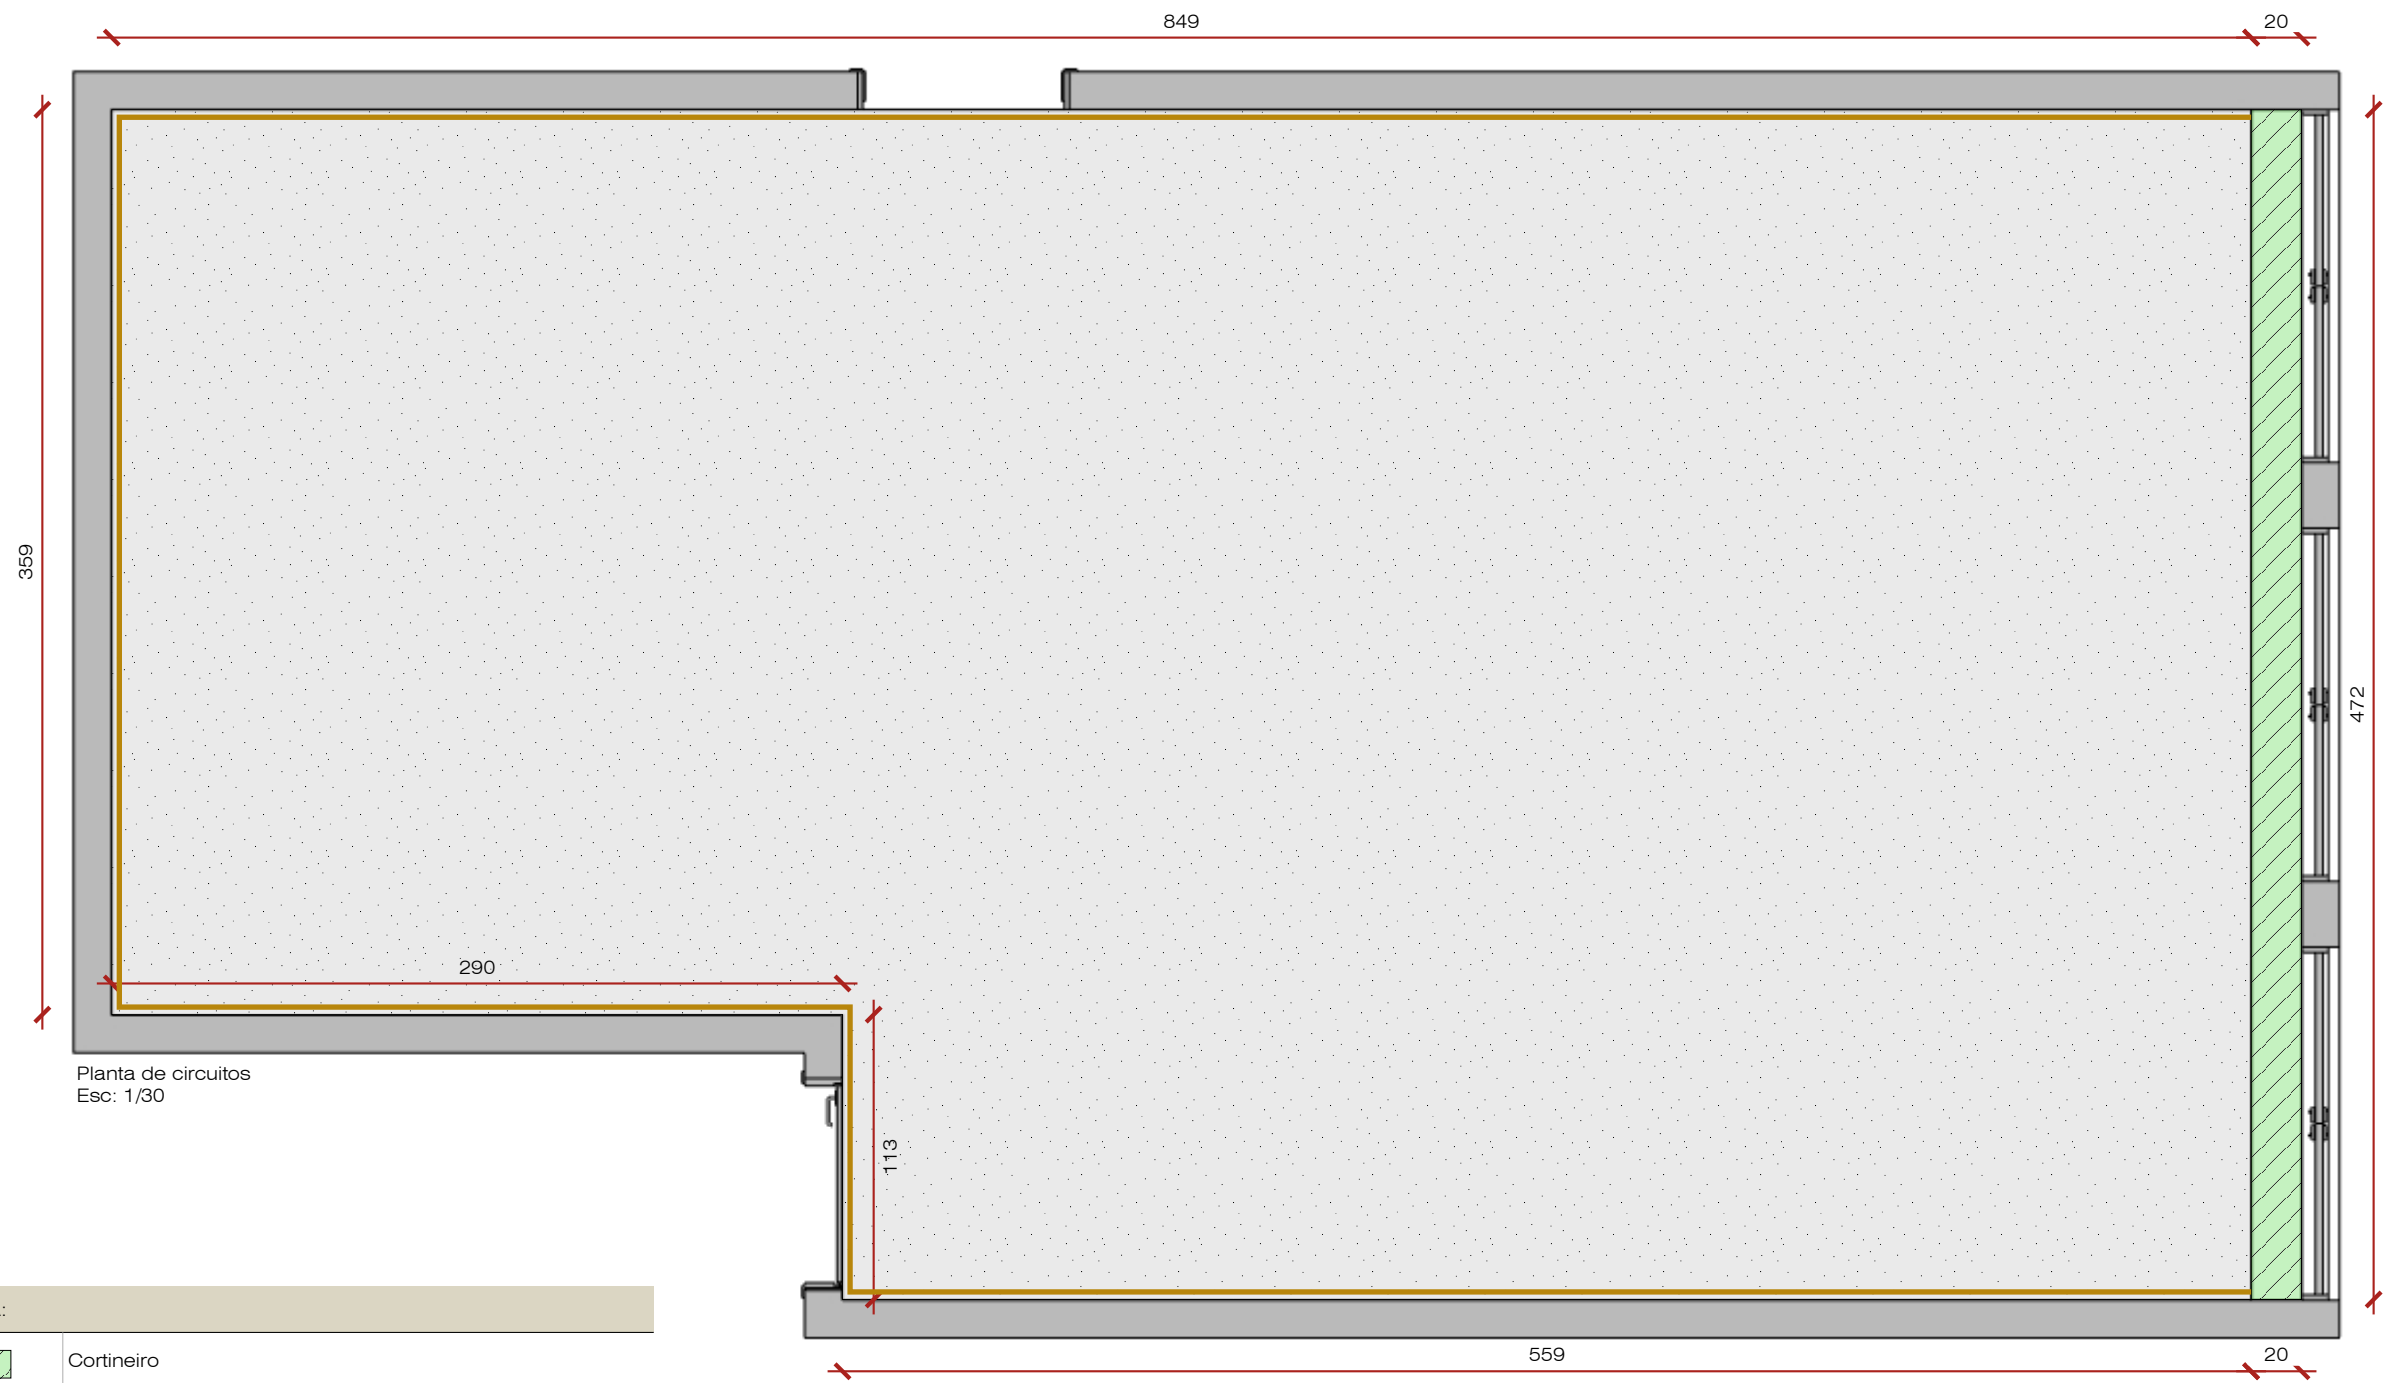

LEGENDA:	
	Cortineiro
	Rebaixo em gesso acartonado - Altura = 12cm
	Tabica - 21,70 metros lineares

Sala

Desenhista: Nathália Rodrigues

As imagens 3D são meramente ilustrativa.
Seguir orientações conforme detalhamento executivo.

Todas as medidas devem ser conferidas no local antes da execução.

Clientes:
Silvana e Hélio

Endereço:
SQS 106 Bloco H, Apartamento 601.
Asa Sul.

Data:
26.08.2026

Arquiteto coordenador

Alisson Correia
Celular (61) 98303-0582


Arquiteta responsável

Aline Coutinho Molina
CAU - A108129-2
Celular (61) 99606-5747

Obs: Todas as medidas em centímetros

05

Aline Molina
arquitetura de interiores

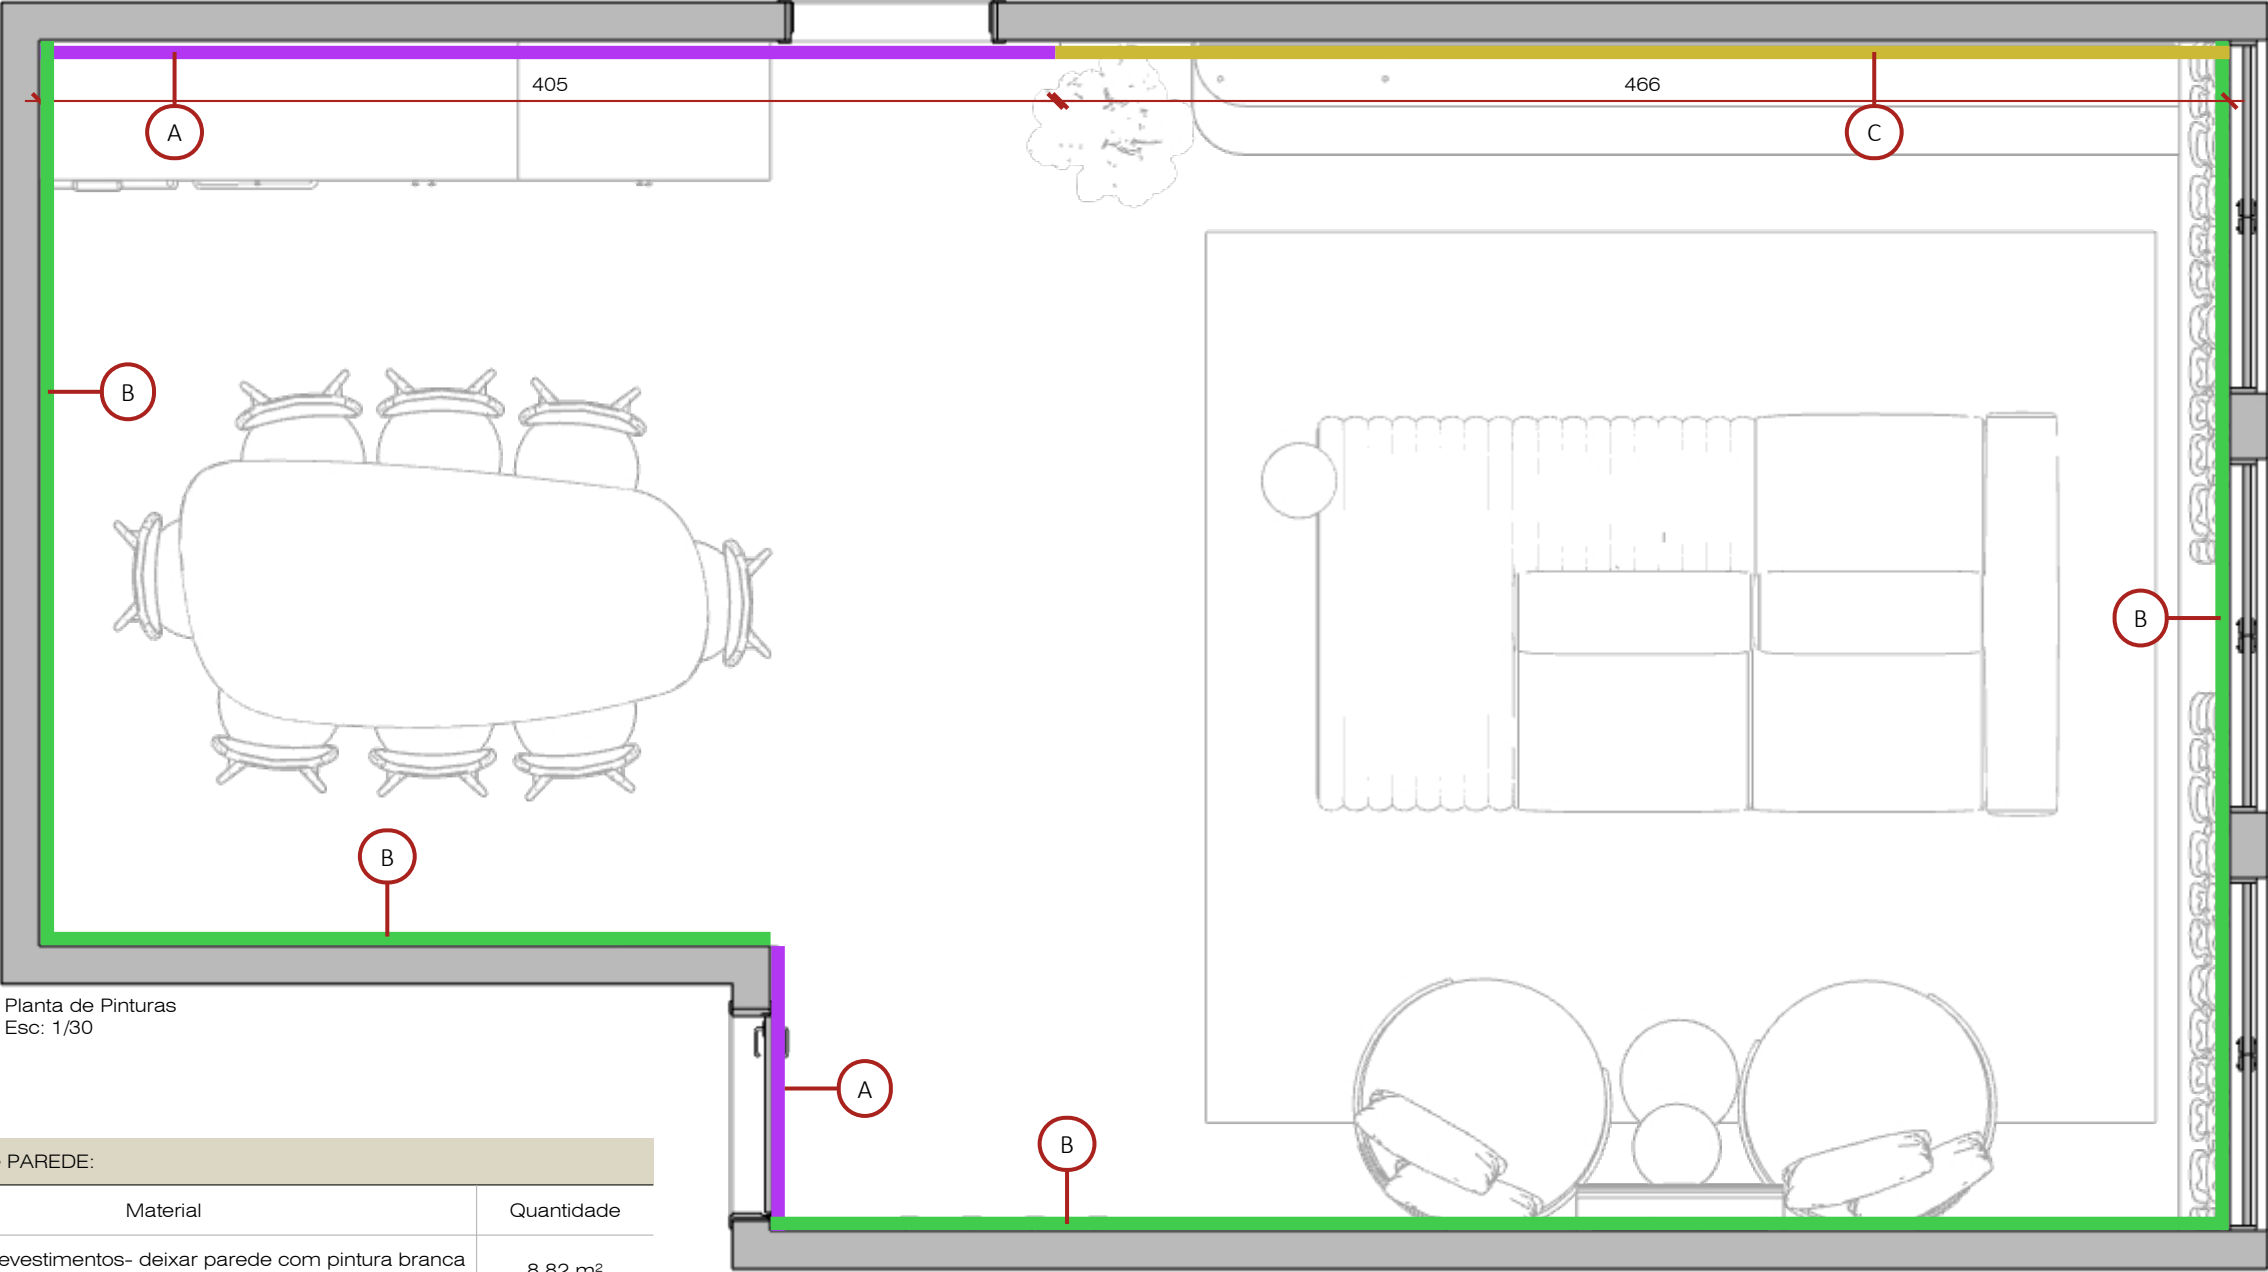

Planta de Pinturas
Esc: 1/30

Tabela de acabamentos de PAREDE:		
Item	Material	Quantidade
A	Marcenaria e revestimentos- deixar parede com pintura branca fosca	8,82 m²
B	Pintura Velvet com poucas manchas: base na cor Feijão Fradinho Sherwin-Williams com acabamento fosco	36,92 m²
C	Textura Fulget - deixar parede na massa lixada : 10% de malha na cor bege + 10% de malha na cor palha + 80% de malha na cor branca	11,38 m²

Tabela de acabamentos de TETO:		
Ambiente	Material	Quantidade
Sala	Pintura Branca Fosca	36,80 m²

Sala

Desenhista: Nathália Rodrigues

As imagens 3D são meramente ilustrativa.
Seguir orientações conforme detalhamento executivo.

Todas as medidas devem ser conferidas no local antes da execução.

Clientes:
Silvana e Hélio

Endereço:
SQS 106 Bloco H, Apartamento 601.
Asa Sul.

Data:
26.08.2026

Arquiteto coordenador

Alisson Correia
Celular (61) 98303-0582


Arquiteta responsável

Aline Coutinho Molina
CAU - A108129-2
Celular (61) 99606-5747




Obs: Todas as medidas em centímetros

06


Aline Molina
arquitetura de interiores

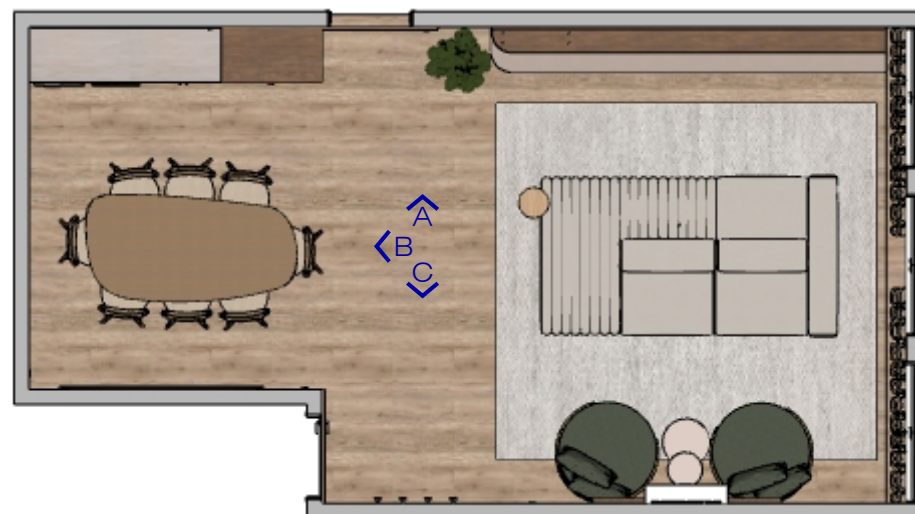


Planta Baixa
Esc: 1/75

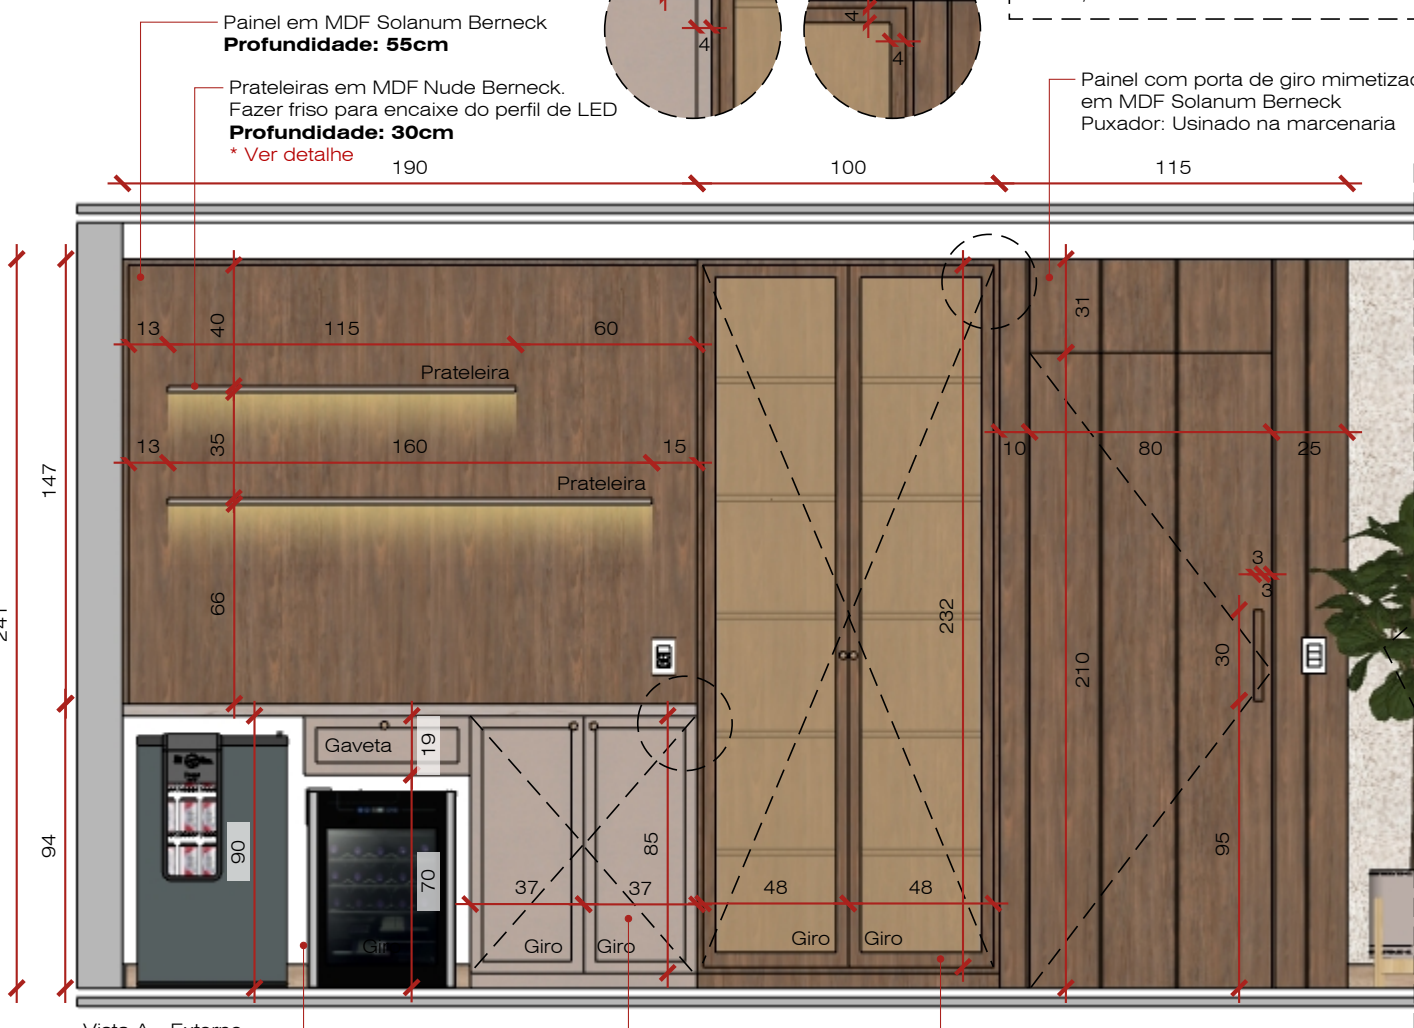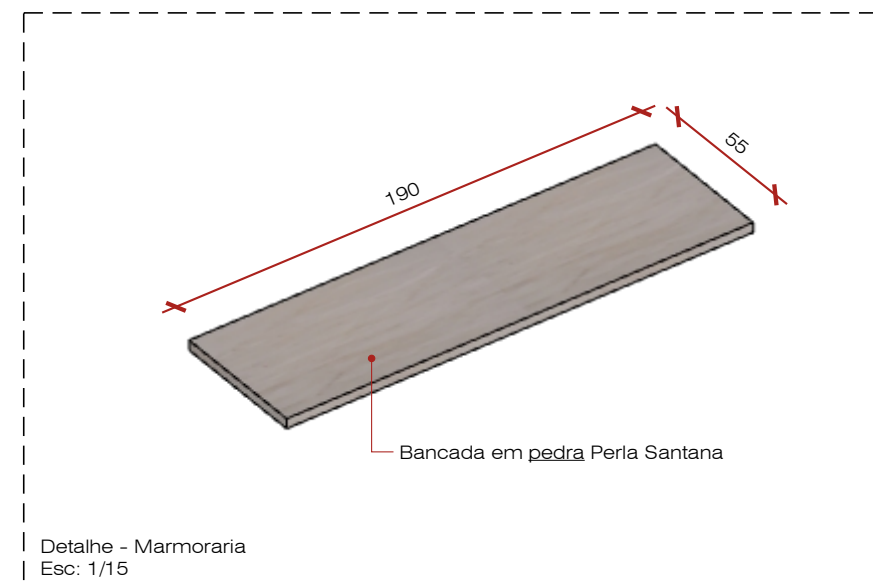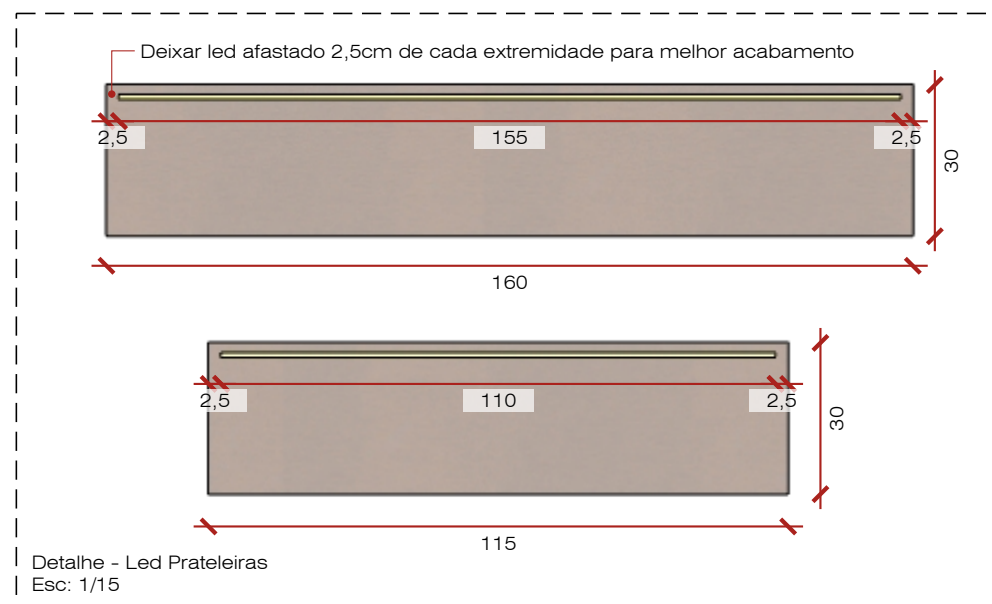

Vista A - Externo
Esc: 1/25

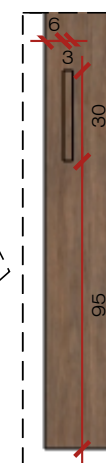

Det. puxador verso da porta
Esc: 1/25

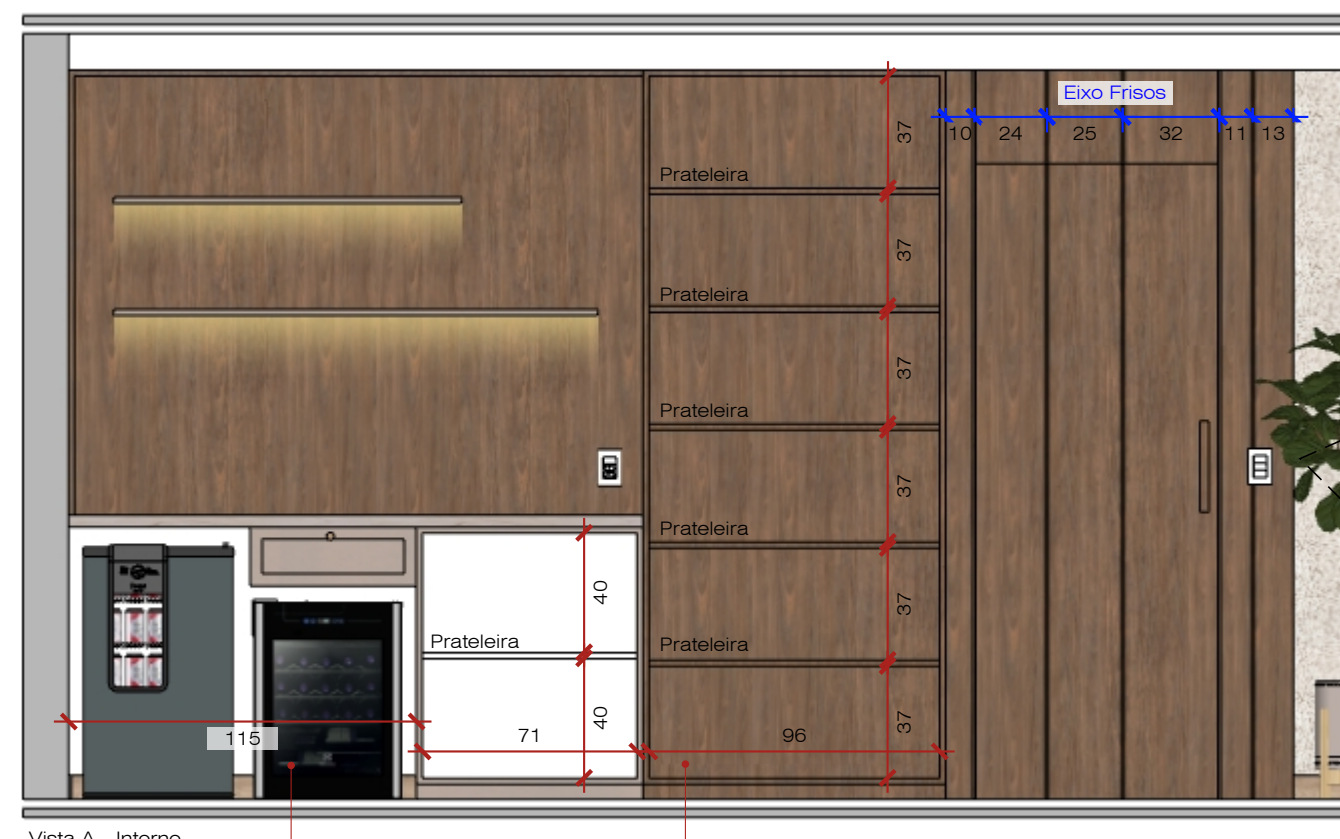

Vista A - Interno
Esc: 1/25

Sala

Desenhista: Nathália Rodrigues

As imagens 3D são meramente ilustrativa.
Seguir orientações conforme detalhamento executivo.

Todas as medidas devem ser conferidas no local antes da execução.

Clientes:
Silvana e Hélio

Endereço:
SQS 106 Bloco H, Apartamento 601.
Asa Sul.

Data:
26.08.2026

Arquiteto coordenador

Alisson Correia
Celular (61) 98303-0582


Arquiteta responsável

Aline Coutinho Molina
CAU - A108129-2
Celular (61) 99606-5747


Obs: Todas as medidas em centímetros

07

Aline Molina
arquitetura de interiores

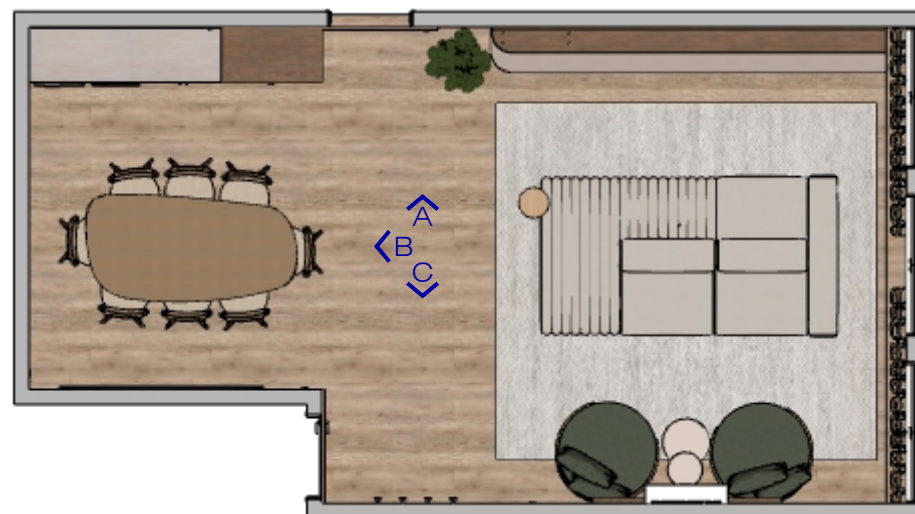


Planta Baixa
Esc: 1/75

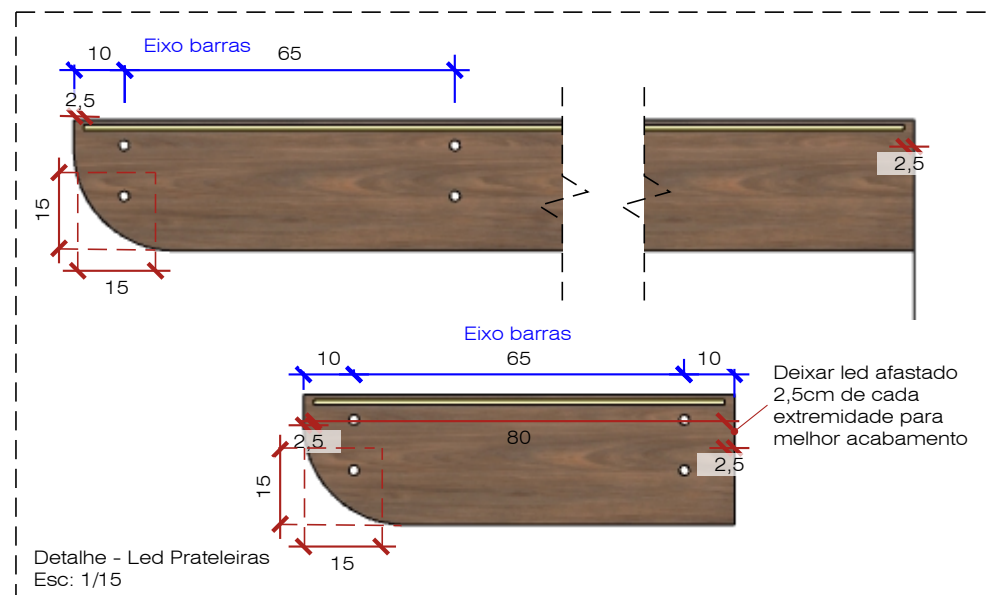

Detalhe - Led Prateleiras
Esc: 1/15




Imagem 3D - Sem escala

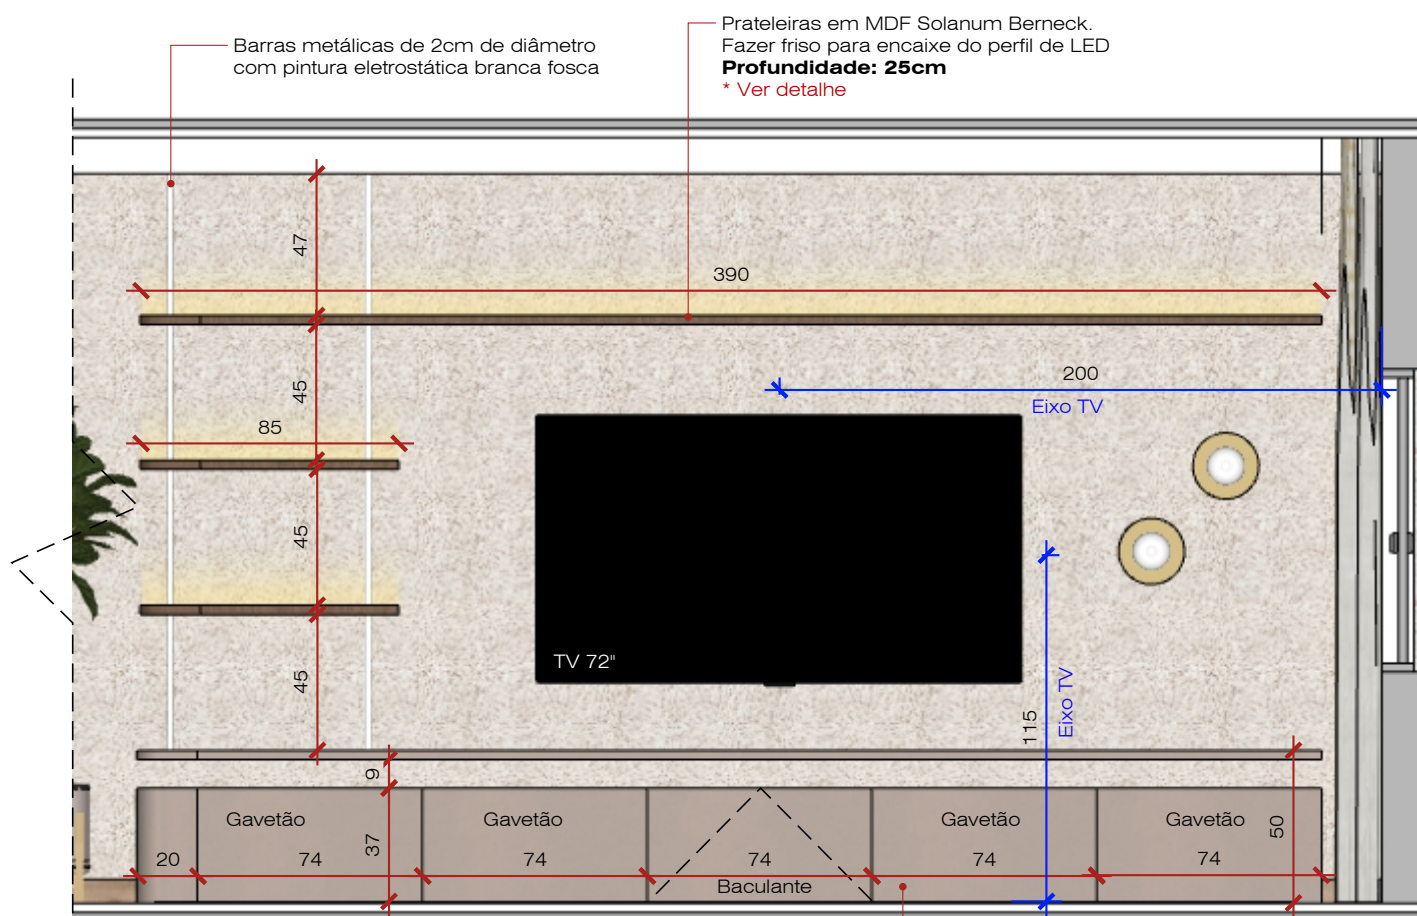

Vista A - Externo
Esc: 1/25

Módulo em MDF Nude Berneck.
Profundidade: 45cm
Puxador: Transpasse de 1cm para puxar

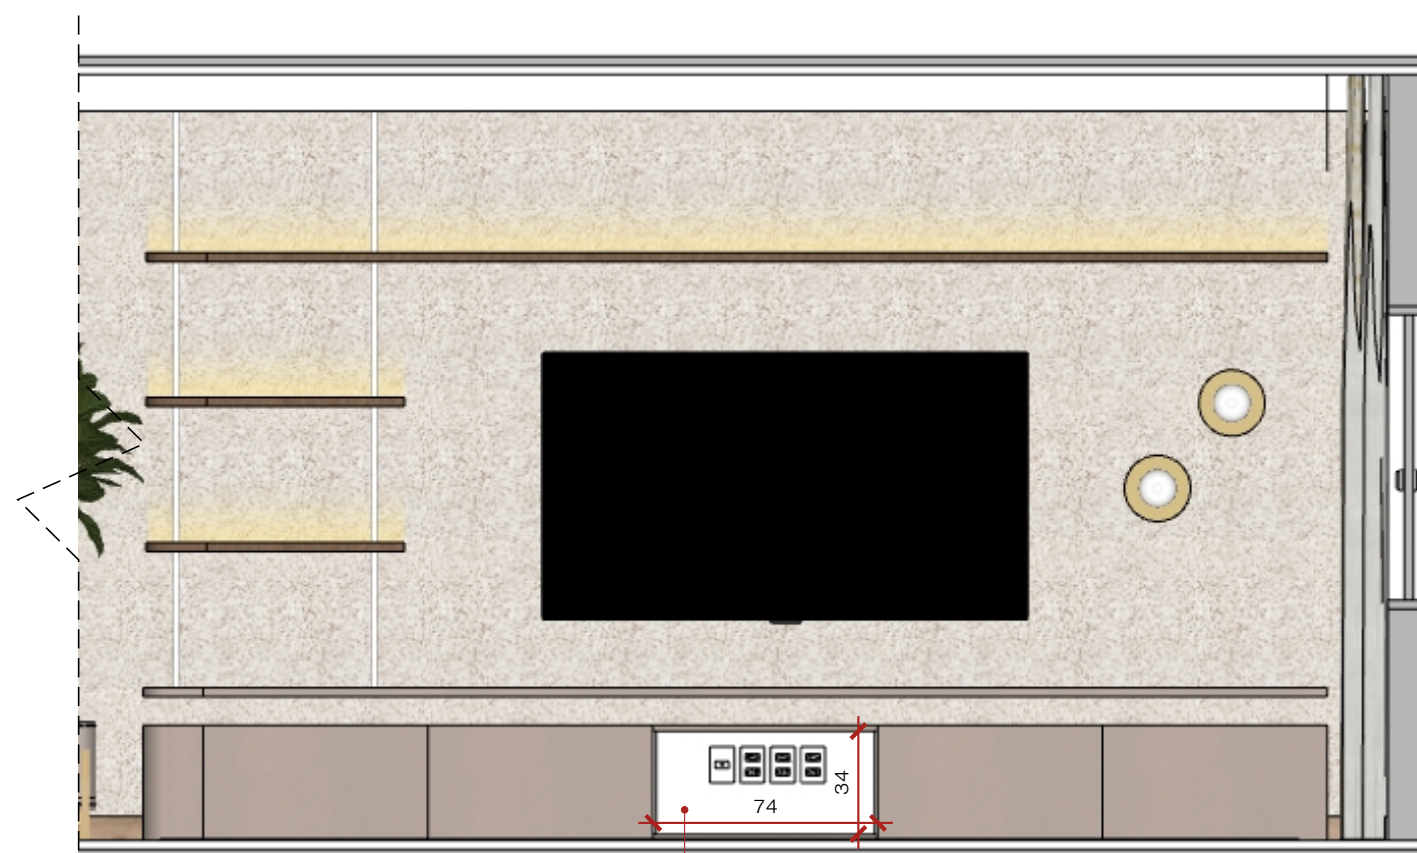

Vista A - Interno
Esc: 1/25

Interno em MDF branco

Sala

Desenhista: Nathália Rodrigues

As imagens 3D são meramente ilustrativa.
Seguir orientações conforme detalhamento executivo.

Todas as medidas devem ser conferidas no local antes da execução.

Clientes:
Silvana e Hélio

Endereço:
SQS 106 Bloco H, Apartamento 601.
Asa Sul.

Data:
26.08.2026

Arquiteto coordenador

Alisson Correia
Celular (61) 98303-0582


Arquiteta responsável

Aline Coutinho Molina
CAU - A108129-2
Celular (61) 99606-5747

Obs: Todas as medidas em centímetros


08

Aline Molina
arquitetura de interiores

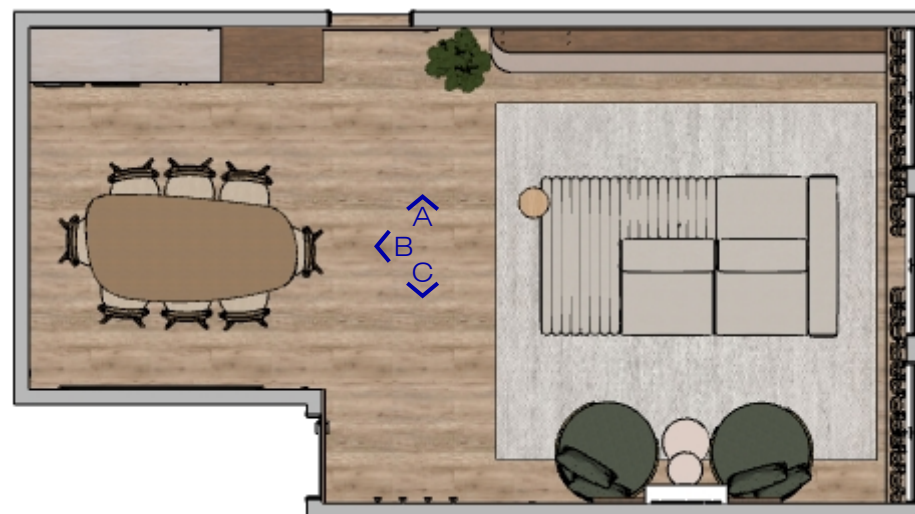

Planta Baixa
Esc: 1/75

Painel com porta de giro mimetizada em
MDF Solanum Berneck.
*Encaixar maçaneta com fechadura

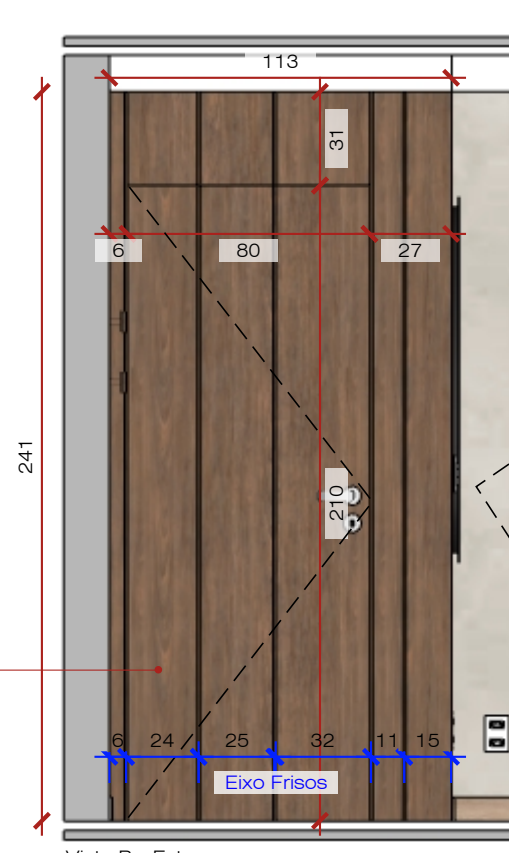


Vista B - Externo
Esc: 1/20



Imagem 3D - Sem escala



Imagem 3D - Sem escala

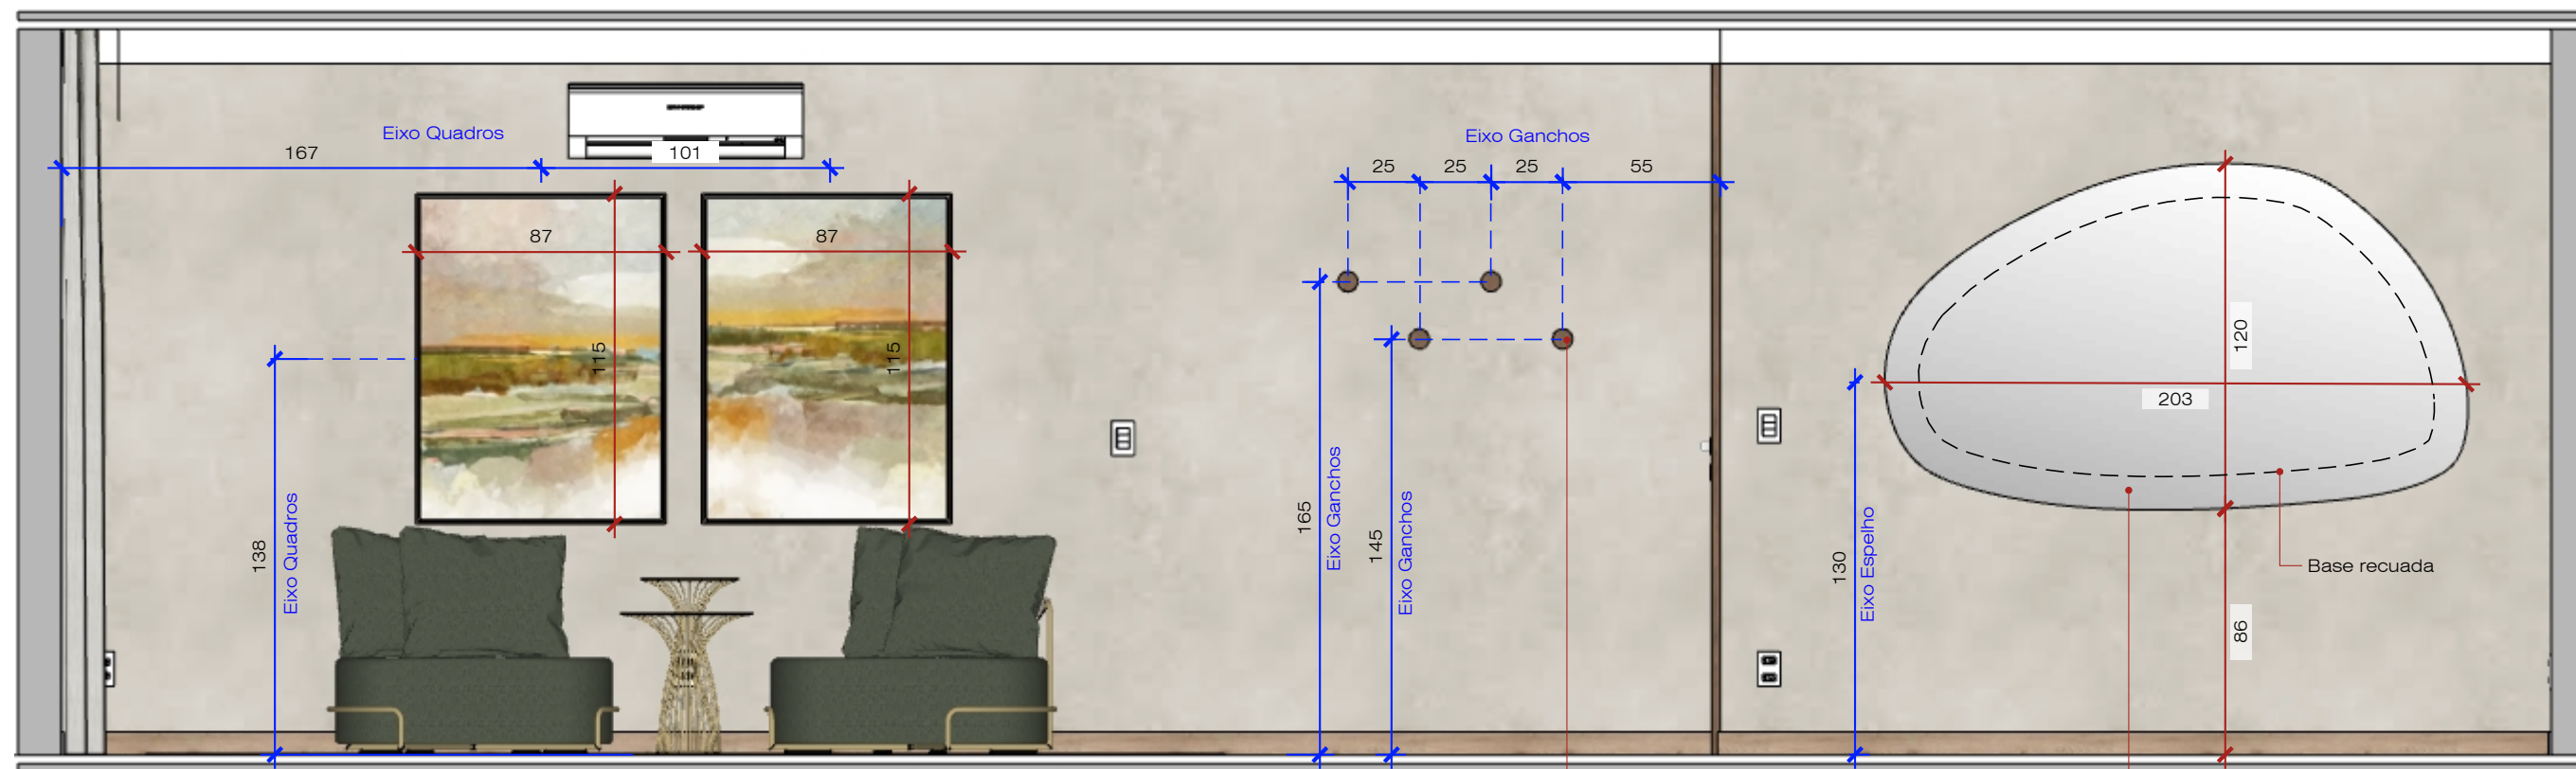

Vista C - Externo
Esc: 1/25

Sala

Ganchos em MDF Solanum Berneck

Espelho Prata Orgânico Flutuante

Base recuada

Desenhista: Nathália Rodrigues

As imagens 3D são meramente ilustrativa.
Seguir orientações conforme detalhamento executivo.

Todas as medidas devem ser conferidas no local antes da execução.

Clientes:
Silvana e Hélio

Endereço:
SQS 106 Bloco H, Apartamento 601.
Asa Sul.

Data:
26.08.2026

Arquiteto coordenador

Alisson Correia
Celular (61) 98303-0582

Arquiteta responsável

Aline Coutinho Molina
CAU - A108129-2
Celular (61) 99606-5747

Obs: Todas as medidas em centímetros

09

Aline Molina
arquitetura de interiores