


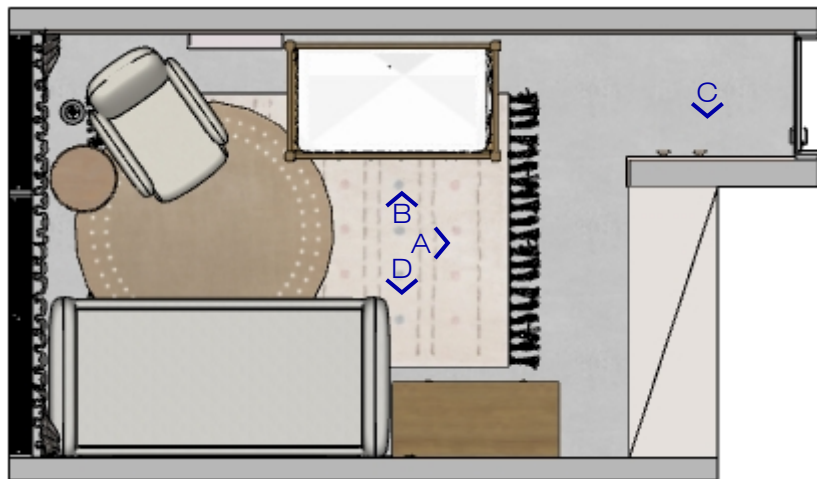

Planta de Layout
Esc: 1/50



Quarto Maria

Desenhista: Brenda Mesquita

As imagens 3D são meramente ilustrativa.
Seguir orientações conforme detalhamento executivo.

Todas as medidas devem ser conferidas no local antes da execução.

Clientes:
Paula e Gabriel

Endereço:
SQN 108, Bloco G, Apt. 508

Data:
26.08.2026

Arquiteto coordenador


Alisson Correia
Celular (61) 98303-0582

Arquiteta responsável


Aline Coutinho Molina
CAU - A108129-2
Celular (61) 99606-5747

04


Aline Molina
arquitetura de interiores

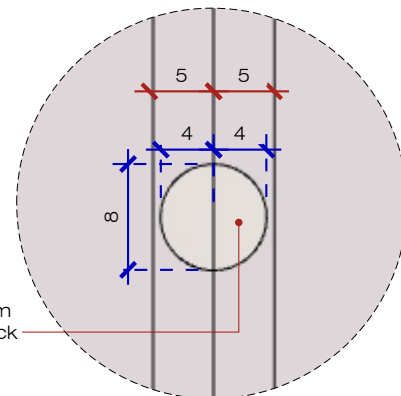

DET - Puxador cava roupeiro
Esc: 1/5

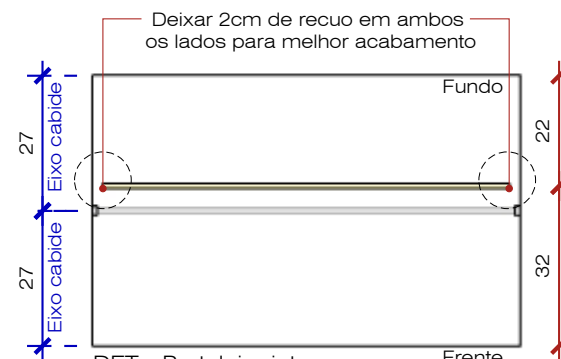


DET - Prateleira interna
Esc: 1/15

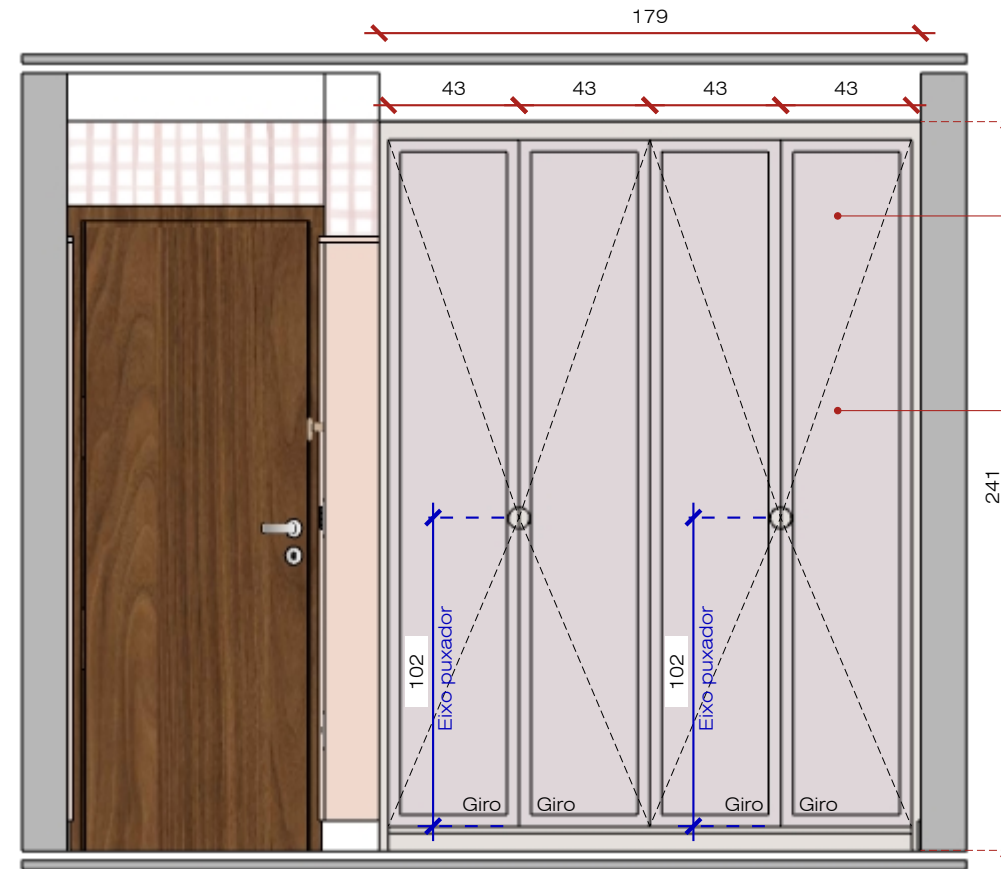

Vista A - Marcenaria
Esc: 1/25

Roupeiro com portas com acabamento em MDF Rosa infinito Duratex e tamponamento em MDF Metallic Suede Berneck
Profundidade: 59cm
Puxador: Cava na marcenaria
***Ver detalhe**

Portas em estilo provençal com molduras de 5cm
***Ver detalhe**

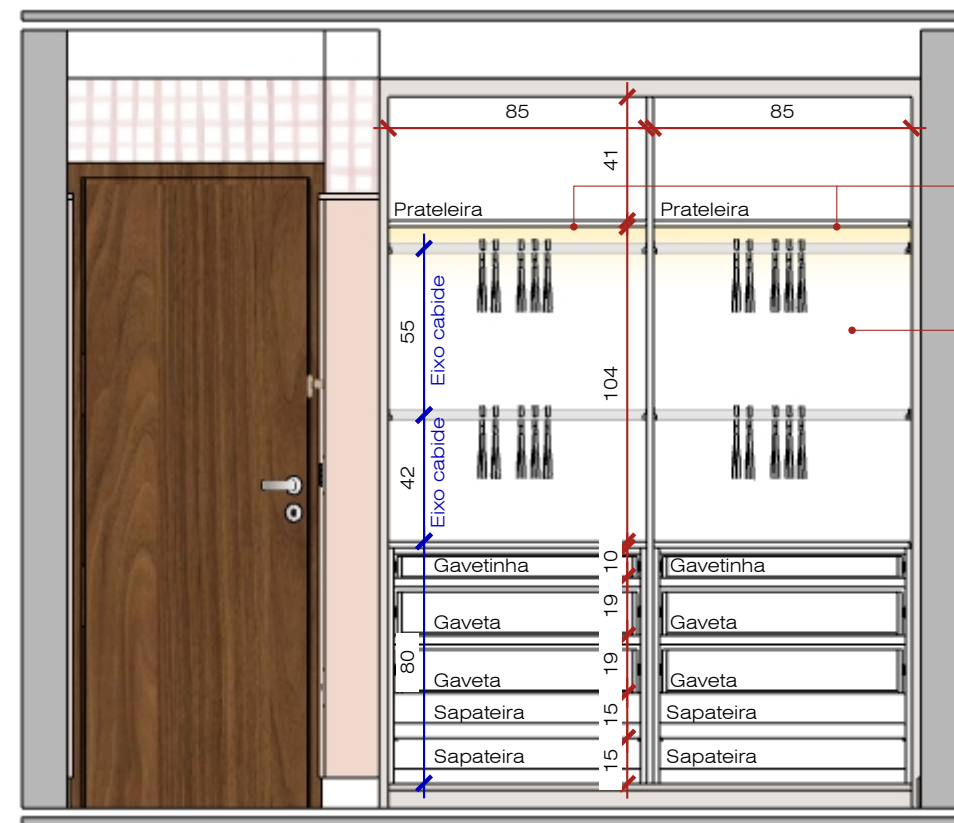

Vista A - Marcenaria interna
Esc: 1/25

Prateleira iluminada
***Ver detalhe**


Acabamento interno em MDF Branco

PROJETO EM
NÃO EXECUTAR
DESENVOLVIMENTO


Obs: Todas as medidas em centímetros




Planta de Layout
Esc: 1/50

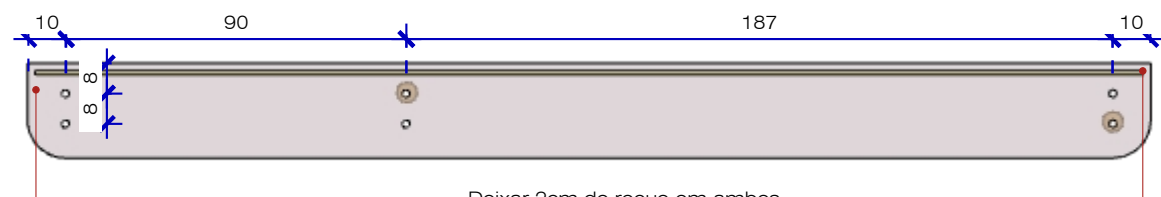

Deixar 2cm de recuo em ambos os lados para melhor acabamento

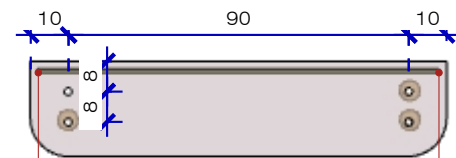


Deixar 2cm de recuo em ambos os lados para melhor acabamento


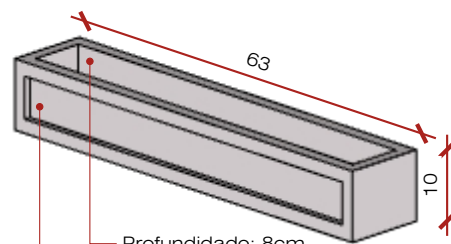


Profundidade: 8cm

Frete provençal com moldura de 2cm

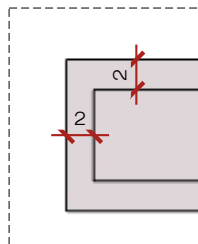


Boisiere Santa Luzia com pintura na cor Praia do Ponta do Mel - Sherwin Williams
***Ver detalhe abaixo**

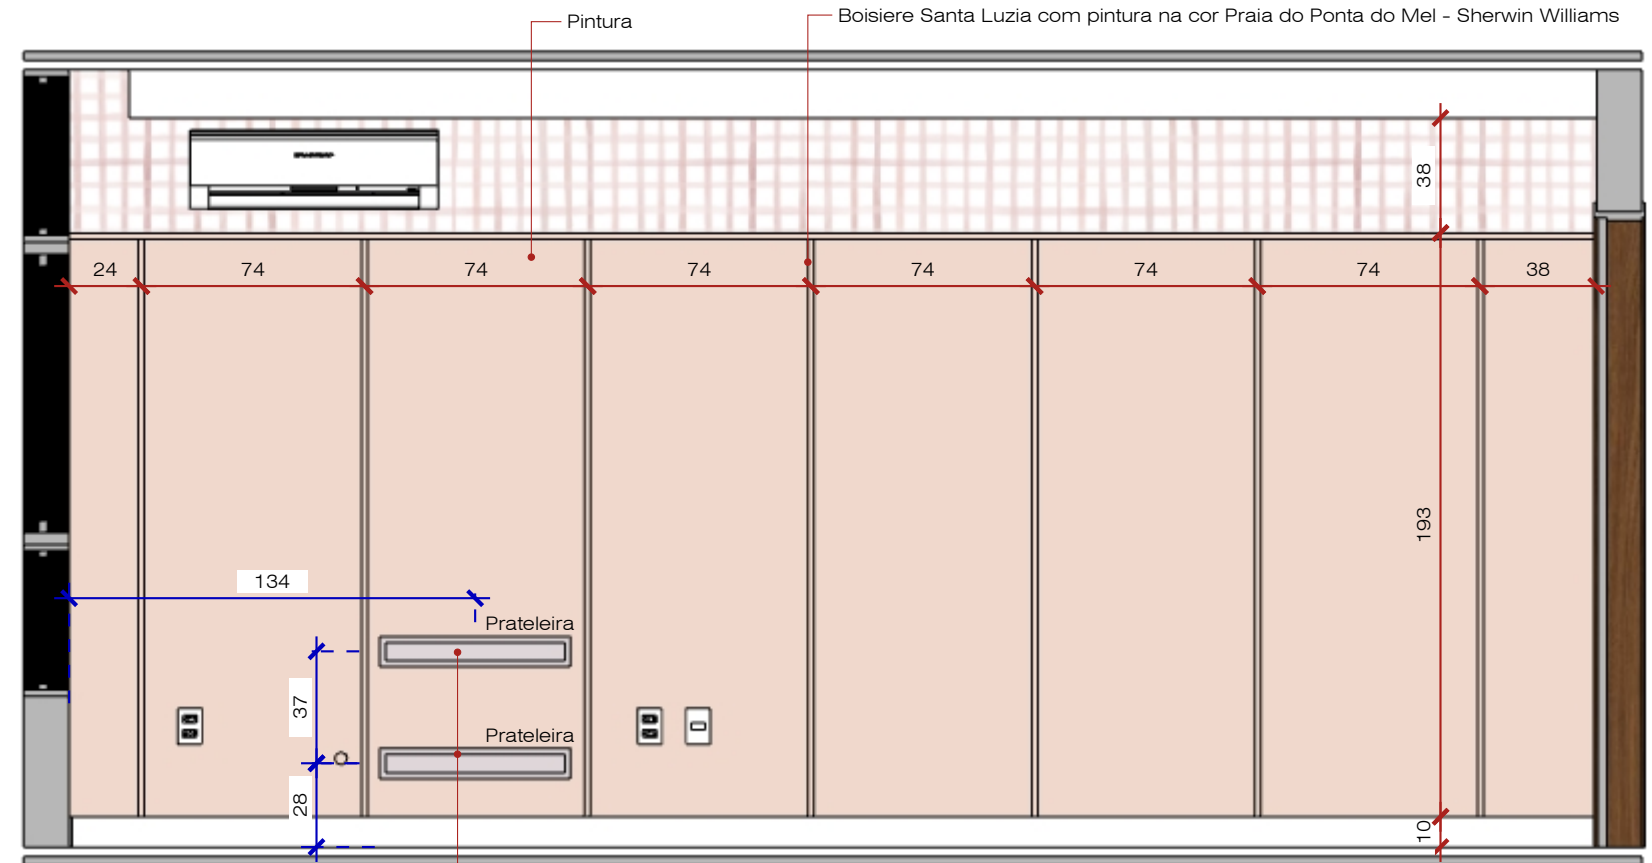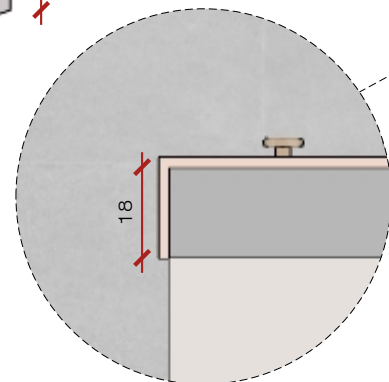

Vista B - Boisiere
Esc: 1/25

Prateleiras com acabamento em MDF Rosa infinito Duratex
***Ver detalhe**


Esferas decorativas em madeira maciça
Quantidade: 6 unidades
***Solicitar aos clientes**

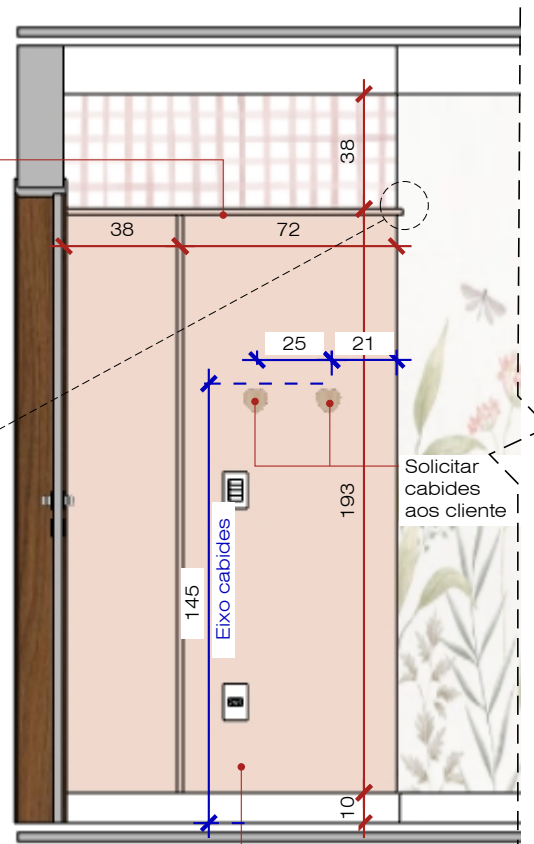

Vista C - Boisiere
Esc: 1/25

Pintura

Solicitar cabides aos cliente

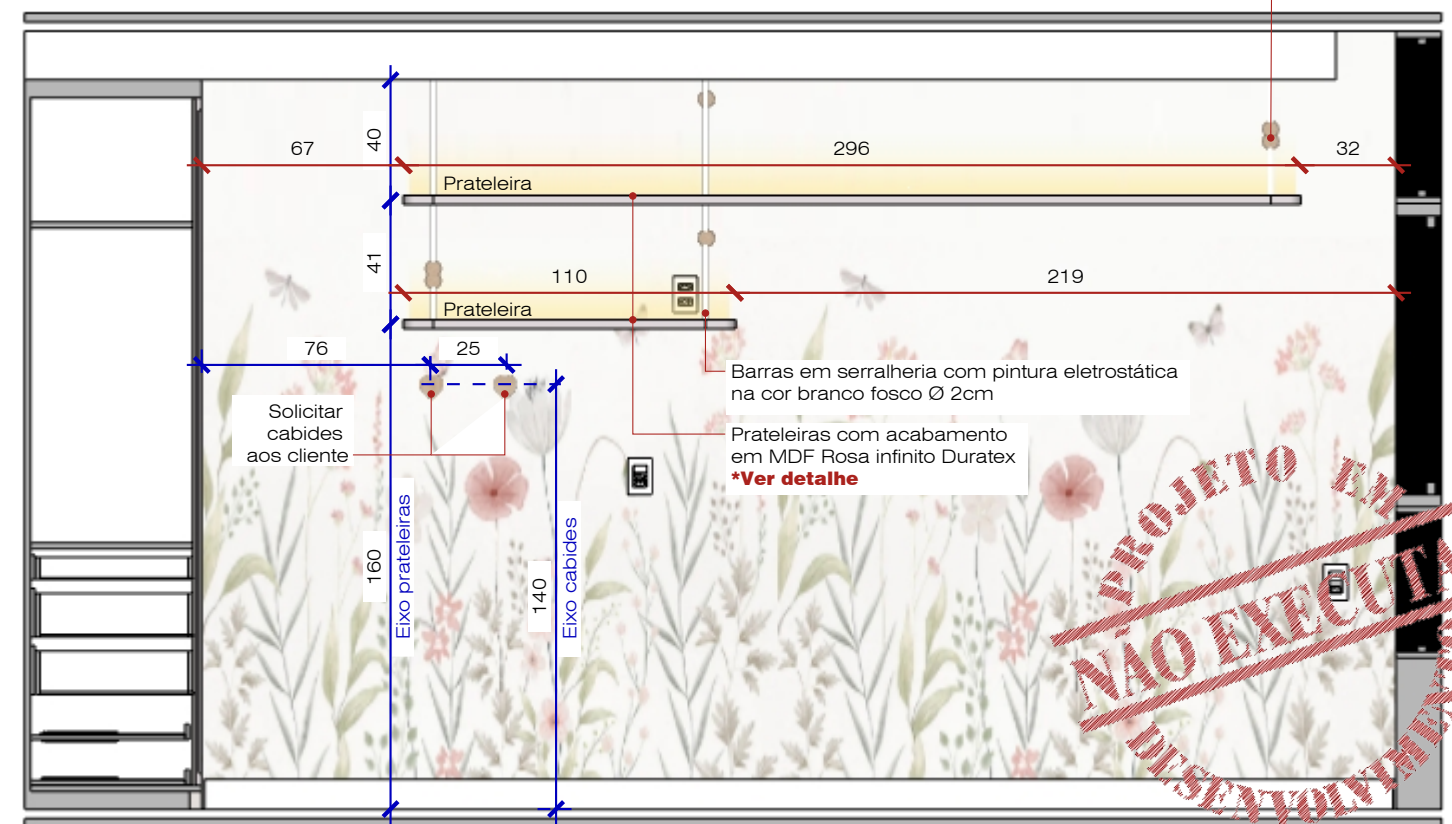

Vista D - Marcenaria e Paginação
Esc: 1/25

Barras em serralheria com pintura eletrostática na cor branco fosco Ø 2cm

Prateleiras com acabamento em MDF Rosa infinito Duratex
***Ver detalhe**



Quarto Maria

Desenhista: Brenda Mesquita

As imagens 3D são meramente ilustrativa.
Seguir orientações conforme detalhamento executivo.

Todas as medidas devem ser conferidas no local antes da execução.

Clientes:
Paula e Gabriel

Endereço:
SQN 108, Bloco G, Apt. 508

Data:
26.08.2026

Arquiteto coordenador

Alisson Correia
Celular (61) 98303-0582

Arquiteta responsável

Aline Coutinho Molina
CAU - A108129-2
Celular (61) 99606-5747

05

Aline Molina
arquitetura de interiores

Obs: Todas as medidas em centímetros